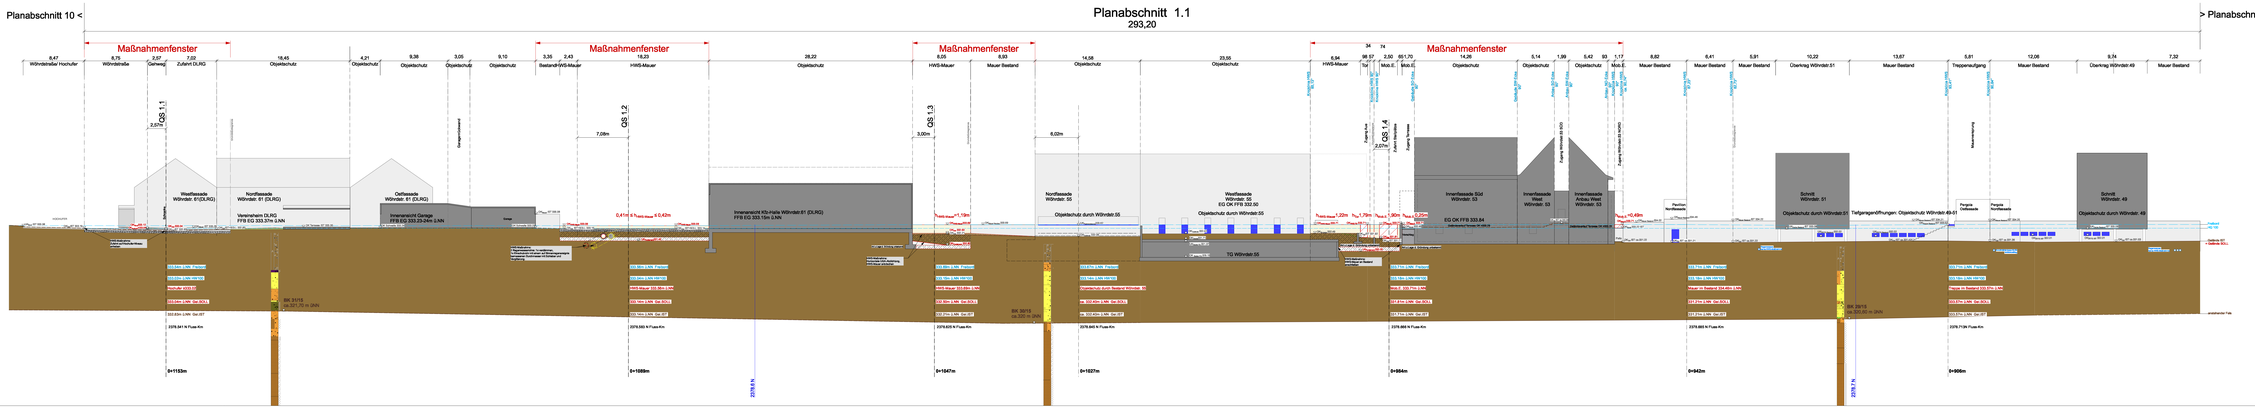

LEGENDE

Legende zu den Bohrprofilen

	Kurzzeichen nach DIN 4023 und DIN 21920	Farbe nach DIN 4023
Kies	G	
Sand	S	
Schluff	U	
Ton	T	

Die schematische Darstellung der eingezeichneten Flächen erfolgt auf Grundlage der Empfehlung aus dem ATV Merkblatt und dem DWA Merkblatt-Merkblatt ohne Anspruch auf Vollständigkeit und Richtigkeit.

integrierter mobiler Objektschutz im Bestand

neues mobiles Element in Fertigstellung

neues dauerhaftes Element / Tor

Vertraulichkeitsvermerk:

Wasserwirtschaftsamt Regensburg

STADT REGENSBURG

Index	Änderung	gezeichnet am	Name	geprüft am	Name
a					
b					
c					

Übersichtslageplan

Vorhaben: Hochwasserschutz Regensburg Abschnitt H Unterer Wöhrd

PLANFESTSTELLUNG

Gemeinde: Regensburg

Landkreis/ Stadt: Freistaat Bayern, Wasserwirtschaftsamt

Vorhabensträger: Landshuter Straße 59, 9093 Regensburg

Maßstab: M 1:200

Planinhalt: Planabschnitt (PA) 1.1
Längsbebauung Nordufer
Wöhrdeltal- 61 (DLRG) bis 49

Planung: Arbeitsgemeinschaft TEAM 3

Plan-Grundlage: 36200-G-B 1.2.1

Anlage: B 1.2.1 Blatt: G

Plan-Nr.: RB-H-PA1.1 LA-200

Vorhabensnummer: 51.90000010

Leitplanung: Amt (SPA) 51-WB

Höhenbezug: Digitalnivellier Höhenlinie des Bayerischen Landesamtes für Vermessung und Geoinformation (BLVGeo) LDBV

erstellt:	12/2021	bearb.:	
gem.:	02/2025	geänd.:	JR
geprüft:	02/2025	gesch.:	MWA

Datum: 30.04. 2025 Unterschrift Vorhabensträger

Datum: 30.05. 2025 Unterschrift Vorhabensträger