


Planabschnitt 1.2 <

Planabschnitt 1.3

> Planabschnitt 2

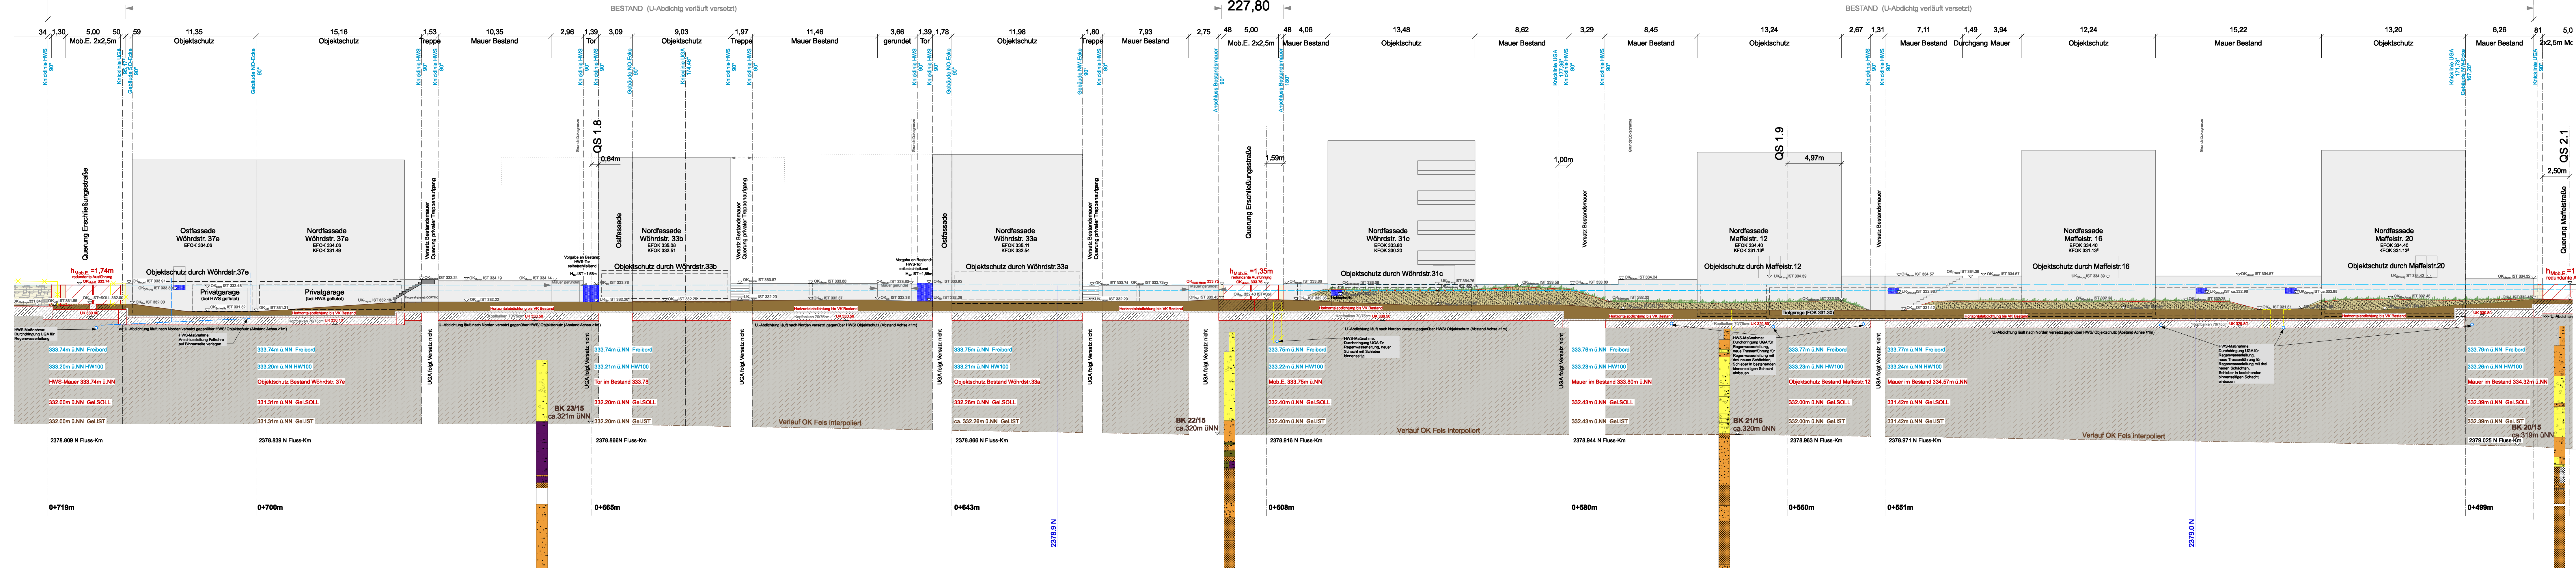

LEGENDE

Symbol	Bedeutung
[Symbol]	Höhe im Bestand
[Symbol]	Höhe in der Planung
[Symbol]	Mob. E. > 2,5m
[Symbol]	HWS-Mauer
[Symbol]	Geländeauftrag
[Symbol]	Geländeauftrag
[Symbol]	Boden im Bestand / Wiederauftrag
[Symbol]	Untergrundabdichtung
[Symbol]	Gründung
[Symbol]	Abbruchmaßnahmen

Symbol	Bedeutung
[Symbol]	Kies
[Symbol]	Sand
[Symbol]	Schluff
[Symbol]	Ton

Symbol	Bedeutung
[Symbol]	Integration mobiler Objektschutz im Bestand
[Symbol]	neues mobiles Element in Fensteröffnung
[Symbol]	neues druckfestes Fenster / Tür

Legende zu den Bohrprofilen

Symbol	Bedeutung
[Symbol]	Kurzzeichen nach DIN 4023
[Symbol]	Zeichen nach DIN 4023 und DIN 21920
[Symbol]	Farbe nach DIN 4023

Die schematische Darstellung der abgewinkelten Fassaden erfolgte auf Grundlage der Fotoabwicklung aus dem VOF-Verfahren und dient allein der Veranschaulichung ohne Anspruch auf Vollständigkeit und Maßhaltigkeit.

Vermehrte Genehmigungsbehörde:

Wasserwirtschaftsamt Regensburg

STADT REGENSBURG

Index

Überstaltungsplan

Vorhaben:

Landkreis / Stadt:

Vorhabenträger:

Maßstab:

Planinhalt:

Lagebezug:

Höhenbezug:

Planung:

30.04.2025

26.05.2025