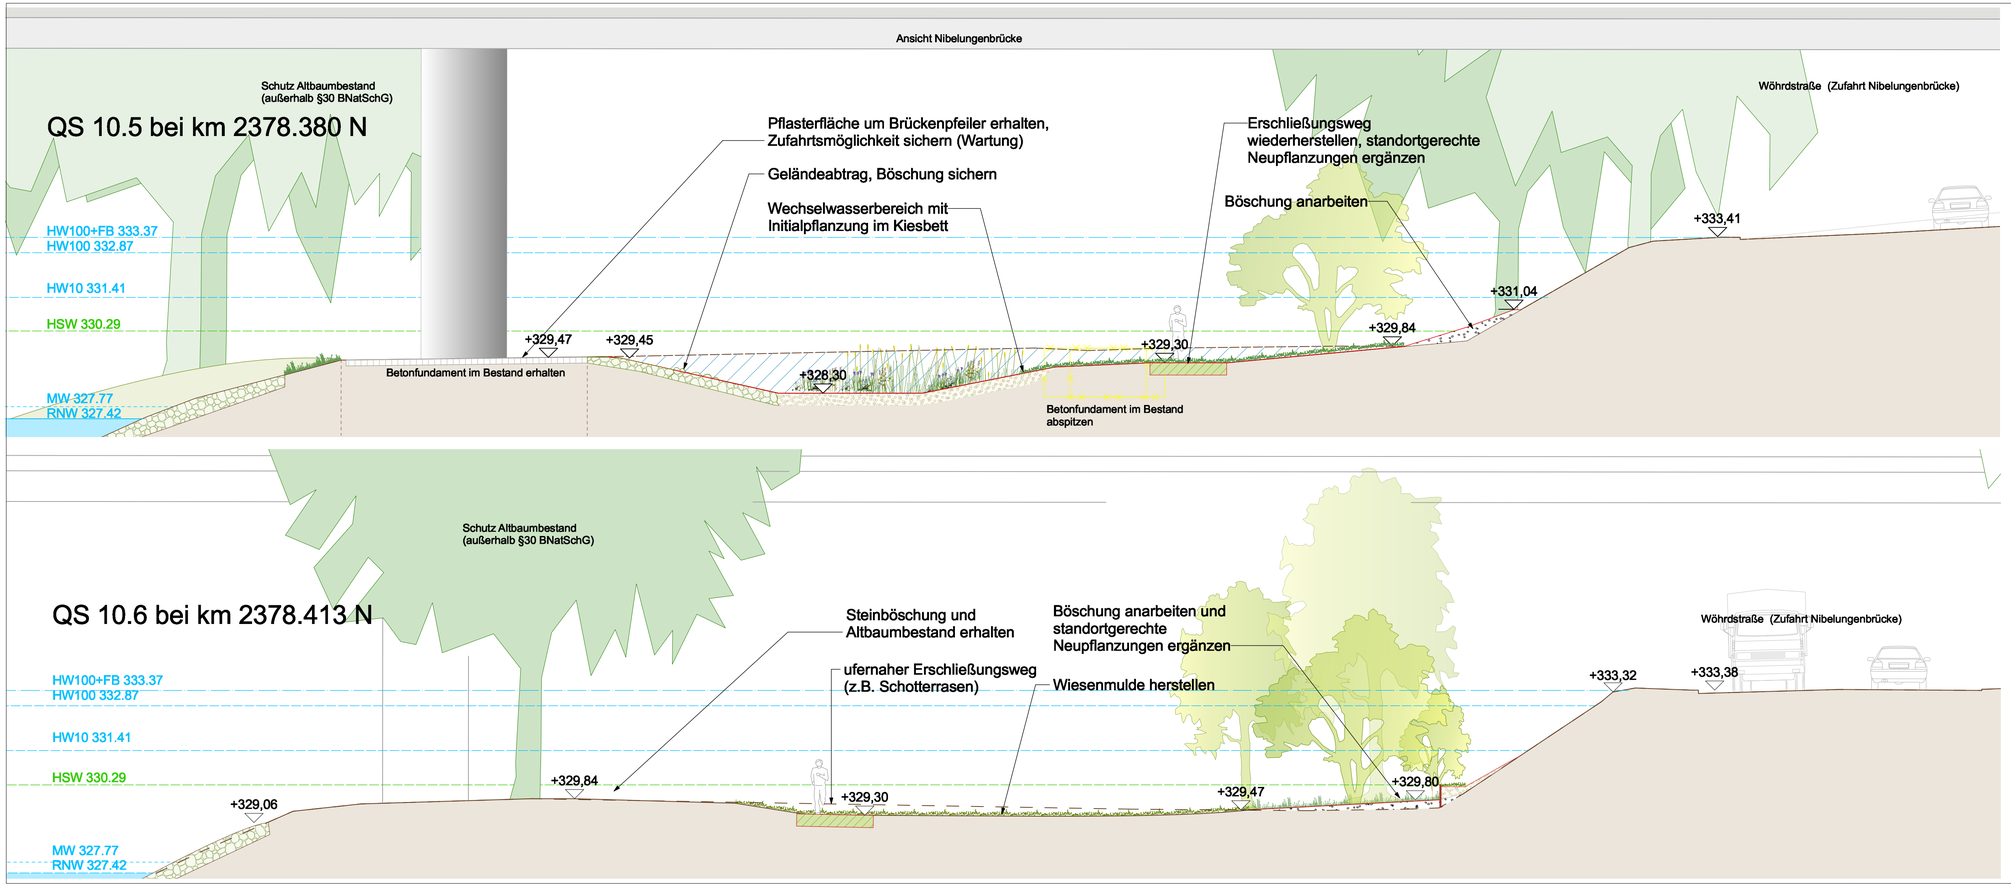

Legende

- +326,53 Höhenkote in müNN
- Mittelwasserlinie/ Röhrrichtzone
- Niedrigwasserzone
- Geländeverlauf im Bestand
- geplanter Geländeverlauf unterhalb Bestand (Abtrag)
- Geplanter Geländeverlauf oberhalb Bestand (Auftrag)
- Räumung
- geschotterter Erschließungsweg
- Sand-/ Kiesschüttung
- Steinschüttung/ Steinschlag
- Böschung im Bestand/ neu
- Baumbestand/ Neupflanzung

Vermerke Genehmigungsbehörde :

Wasserwirtschaftsamt Regensburg

STADT REGENSBURG

Index	Bemerkung	geändert am	Name	geprüft am	Name
c					
b					
a					

Übersichtslageplan

Vorhaben : Hochwasserschutz Regensburg
Abschnitt H Unterer Wöhrd
PLANFESTSTELLUNG

Landkreis/ Stadt : Regensburg

Vorhabenträger : Freistaat Bayern, Wasserwirtschaftsamt Landshuter Straße 59, 9053 Regensburg

Plan-Code : 36200-G-10.1.3

Anlage : B10.1.3 Phase : G

Plan-Nr. : RB-H-QS10.5/6_100

Vorhabenkennzeichen: G11 36200001015

Maßstab : 1:100

Planinhalt : Planabschnitt (PA)10
Querschnitte 10.5/ 10.6.

Lagebezug: GK4 (EPSG 31468)

Höhenbezug: Regensburger Höhennetz aus 1927 in m ü.NN(# DHHN12/ 92/ 2016 des LSBV)

Planung : Arbeitsgemeinschaft TEAM 3

schönig plan INGENIEURGESELLSCHAFT mbH
archiscape architekten und landschaftsarchitekten
tgm Landschaftsarchitekten

entw. :	3/2024	team 3
gez. :	4/2025	LB
gepr. :	5/2025	WWA

30.04. 2025 Datum — Unterschrift Entwurfsverfasser

26.06. 2025 Datum — Unterschrift Vorhabenträger