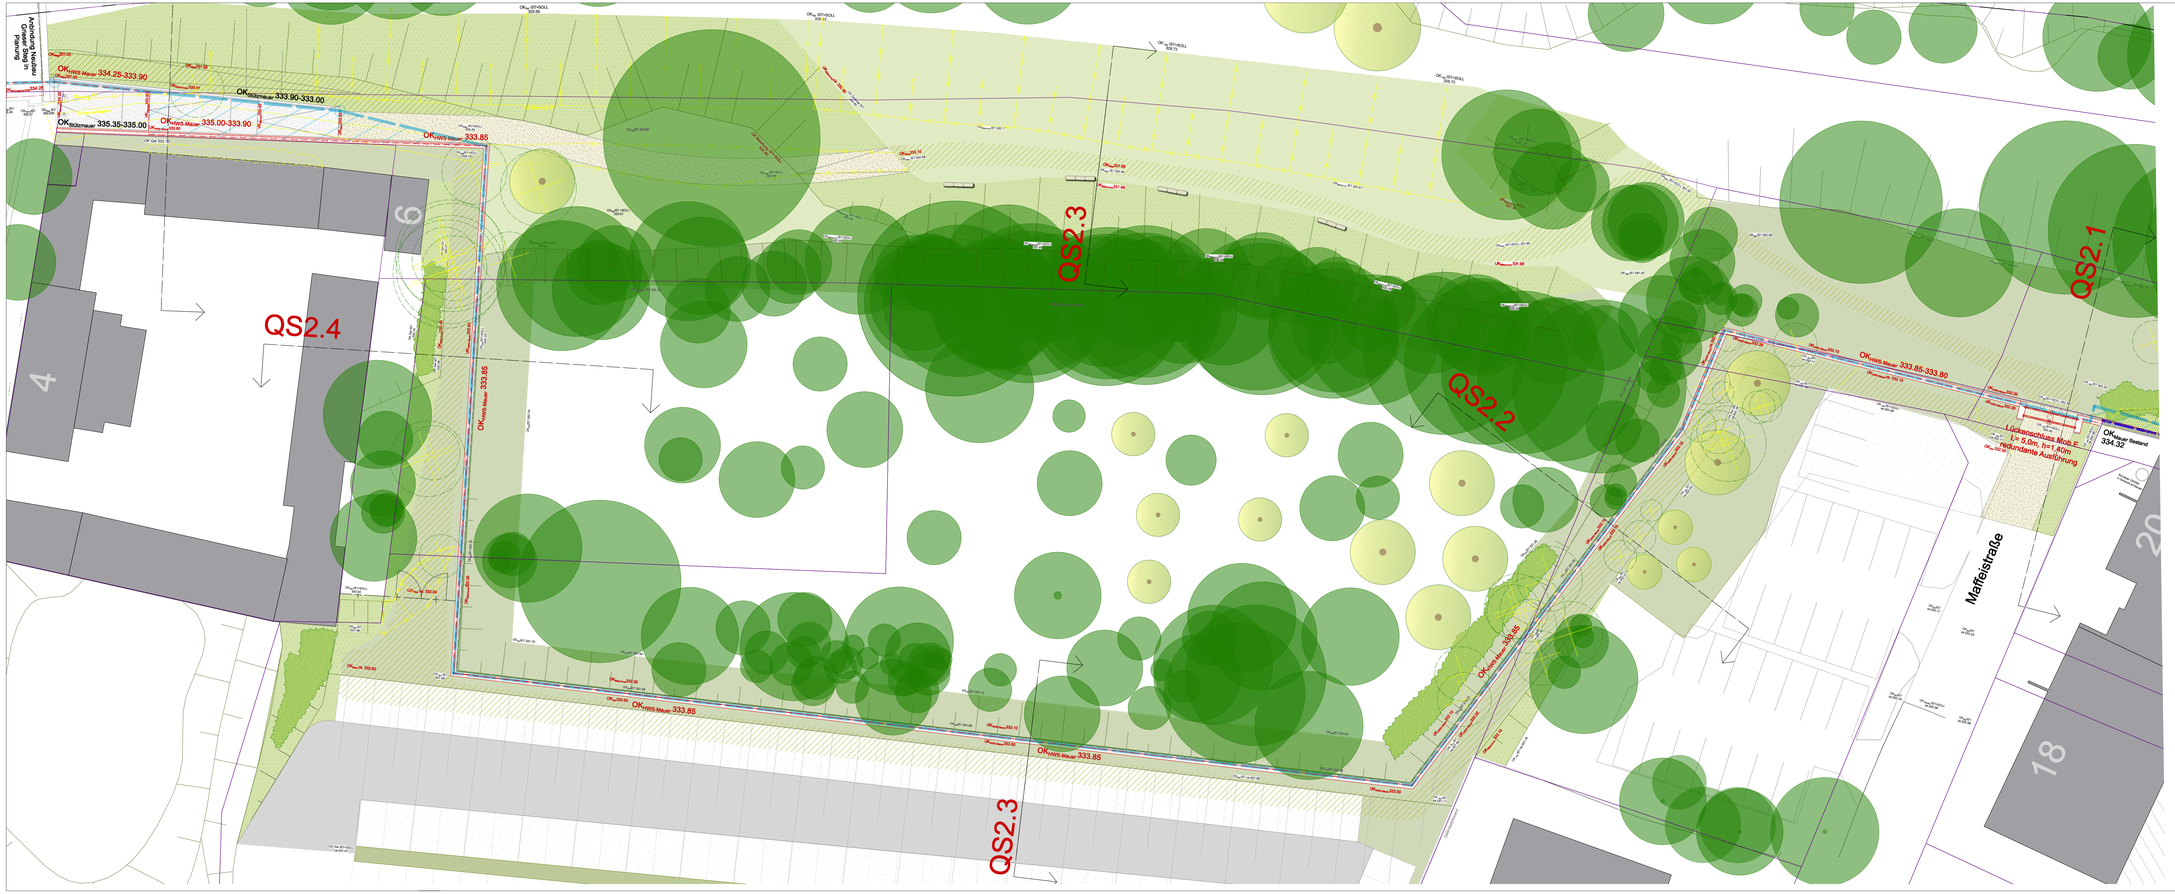

LEGENDE

- Flurstücksgrenze
- Gehölzbestand, Erhalt
- Straßenbaum Hecke im Bestand, Erhalt
- 333.80 Höhe im Bestand
- Böschung im Bestand
- Asphaltbelag im Bestand
- Schotter im Bestand [Wasserdurchlässig]
- ungebundener Belag [Schotter] im Bestand
- Abbruch
- Gebäude im Bestand
- Tiefgarage im Bestand
- Denkmal im Bestand
- Extensive Wiese im Bestand [Wasserdurchlässig]
- Ufermauer, saniert
- Mauer im Bestand
- Gehölzstandort, Erstfall
- Neupflanzung Gehölze Standort verschieben
- Neupflanzung Strauch / Hecke Standort verschieben
- 333.80 geplante Höhe
- Böschung, neu
- neuer Pflasterbelag gebunden, geschnitten/ bahnauen
- neuer Pflasterbelag, gebunden, Spitzkopf Reihenfuge
- neue Schotterdecke/ wassergebundene Decke
- Rasengittersteine, neu
- Schotterrasen, neu (Befahrbarkeit)
- Wiese mit hohem Blütenanteil (Gräser/ Staude), neu
- wechselfeuchte Wiese, neu
- extensiv gepflegte Wiese, neu
- intensiv gepflegte Wiese, neu
- Wasserbaustein/ Trockenmauer, neu
- Achse mobiler HWS (Mobile Elemente)
- mobiler HWS (Teil- abschnitt Mob.E.)
- stationäre HWS (Stahlbetonwand)
- stationäre HWS mit aufgesetzten mobilen Elementen
- Achse vertikale Untergrundabdichtung
- horizontale Untergrundabdichtung
- geöffnetes/ eingetiefter Hitz-Schutz
- Integration bestehender mobiler Versuchbau
- PKW-Stellplatz neu
- behindertengerecht
- neue Treppenanlage
- Sonitstein, neu
- Sitzbank, neu
- Stockstahlquader, neu
- Poller, neu
- Einfriedung, Zaunanlage
- Sitzmauer, neu
- Handlauf Geländer, neu
- offene Straßenentwässerungsrinne, neu
- Rinne mit Abdeckung, neu
- Straßenablauf, neu
- Schacht, neu

N

Vermerke Genehmigungsbehörde :

Wasserwirtschaftsamt Regensburg

STADT REGENSBURG

Index	Bemerkung	gezeichnet am	Name	geprüft am	Name
c					
b					
a					

Übersichtslageplan

Vorhaben :	Hochwasserschutz Regensburg Abschnitt H Unterer Wöhrd PLANFESTSTELLUNG	Plan-Code :	36200-G-B 2.0.0
		Anlage : B 2.0.0	Phase : G
Landkreis/ Stadt :	Regensburg	Plan-Nr. :	RB-H-LP 2-200
Vorhabensträger :	Freistaat Bayern, Wasserwirtschaftsamt Landshuter Straße 59, 9053 Regensburg	Vorhabensnummer/nen:	01.36200/0015
Maßstab : M 1:200	Planinhalt : Planabschnitt (PA) 2 Lageplanausschnitt Jacobi-Gelände Maffeistr. 20 bis Proskestr. 4	Lagebezug :	GKX (ETRS3 31468)
		Höhenbezug :	Regensburger Höhenmeter: dus 1857 m n. (LNA)/ DHHN12 BZ 2016 (bis LDBV)
Planung :	Arbeitsgemeinschaft TEAM 3	erbr. : 3/2024	team 3
		gez. : 4/2025	UB
		gepr. : 5/2025	WWA

SCHÖNBERGER INGENIEURGESELLSCHAFT mbH | ARCHISCAPE ARCHITEKTEN | TTT. Landschaftsarchitekten

30.04. 2025		26.05. 2025	
Datum	Unterschrift Entwurfsverfasser	Datum	Unterschrift Vorhabensträger