


QS 2.1 bei km 2379.034

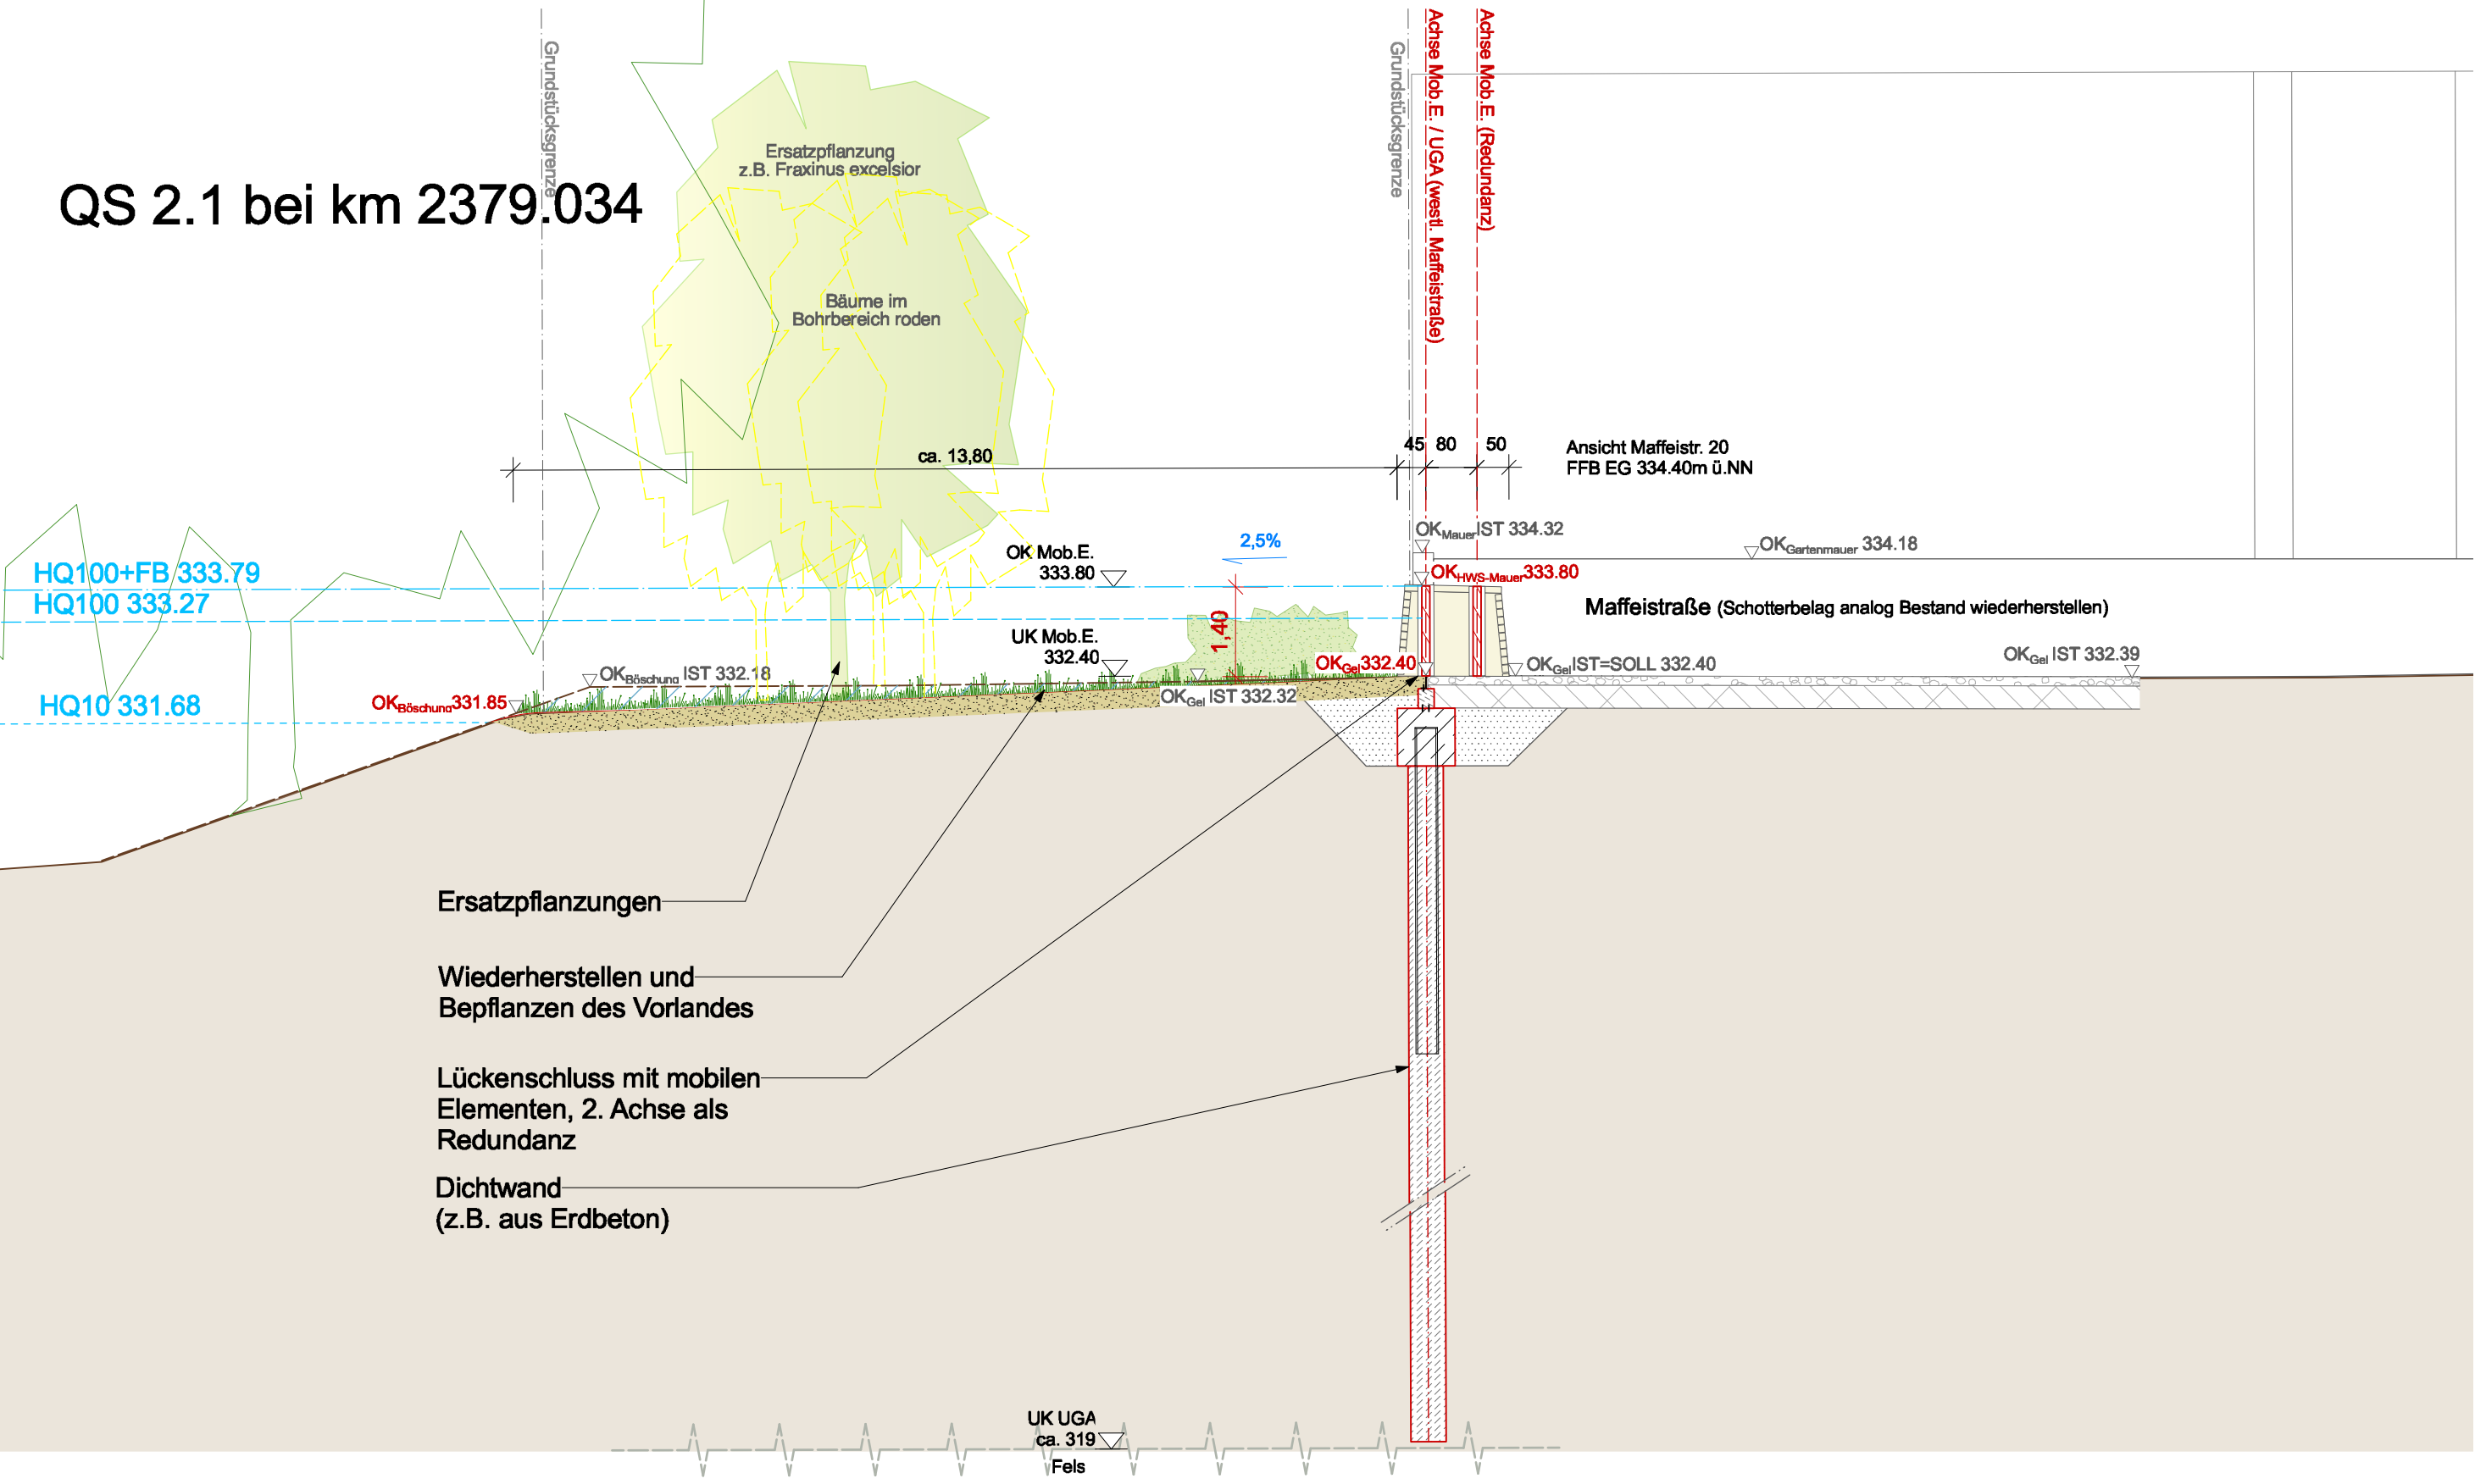


Ersatzpflanzungen

Wiederherstellen und
Bepflanzen des Vorlandes

Lückenschluss mit mobilen
Elementen, 2. Achse als
Redundanz

Dichtwand
(z.B. aus Erdbeton)

LEGENDE

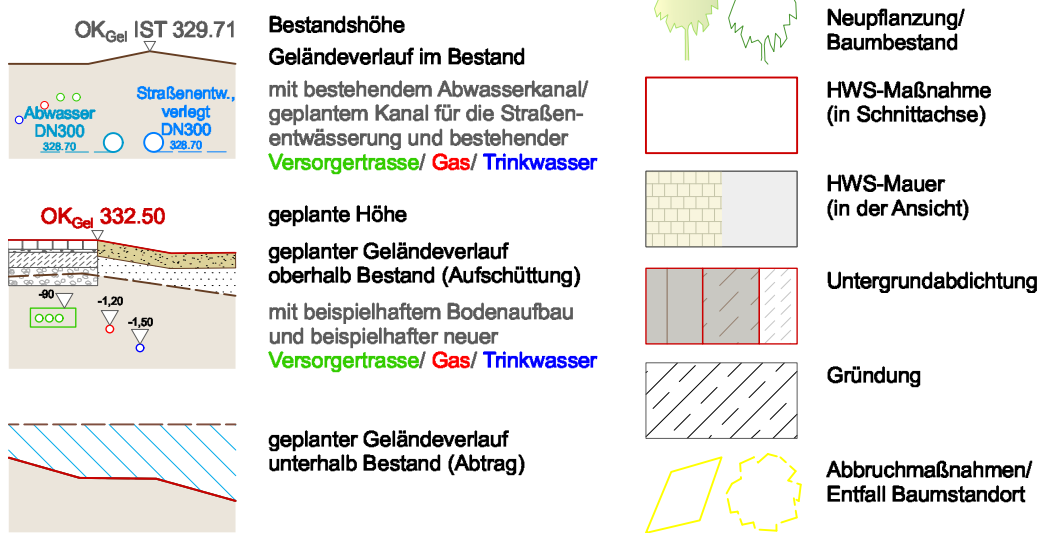

Vermerke Genehmigungsbehörde :

Wasserwirtschaftsamt Regensburg

STADT REGENSBURG

c					
b					
a					
Index	Bemerkung	geändert am	Name	geprüft am	Name

Übersichtslageplan

Vorhaben : Hochwasserschutz Regensburg Abschnitt H Unterer Wöhrd PLANFESTSTELLUNG

Landkreis/ Stadt : Regensburg

Vorhabensträger : Freistaat Bayern, Wasserwirtschaftsamt Landshuter Straße 59, 9053 Regensburg

Maßstab : M 1:100

Planinhalt : Planabschnitt (PA)2 Querschnitt 2.1, Achse Maffeistraße

Planung : Arbeitsgemeinschaft TEAM 3

entw. : 3/2024

gez. : 4/2025

gepr. : 5/2025

30.04. 2025

26.05. 2025

Datum

Unterschrift Entwurfsverfasser

Datum

Unterschrift Vorhabensträger

Plan-Code : 36200-G-B 2.1.1

Anlage : B 2.1.1

Phase : G

Plan-Nr. : RB-H- QS 2.1-100

Vorhabenskennzeichen: G1t 3620001015


Lagebezug: GK4 (EPSG 31468)

Höhenbezug: Regensburger Höhennetz aus 1927 in m ü.NN(≠ DHHN12/ 92/ 2016 des LDBV)

team 3

UB

WWA

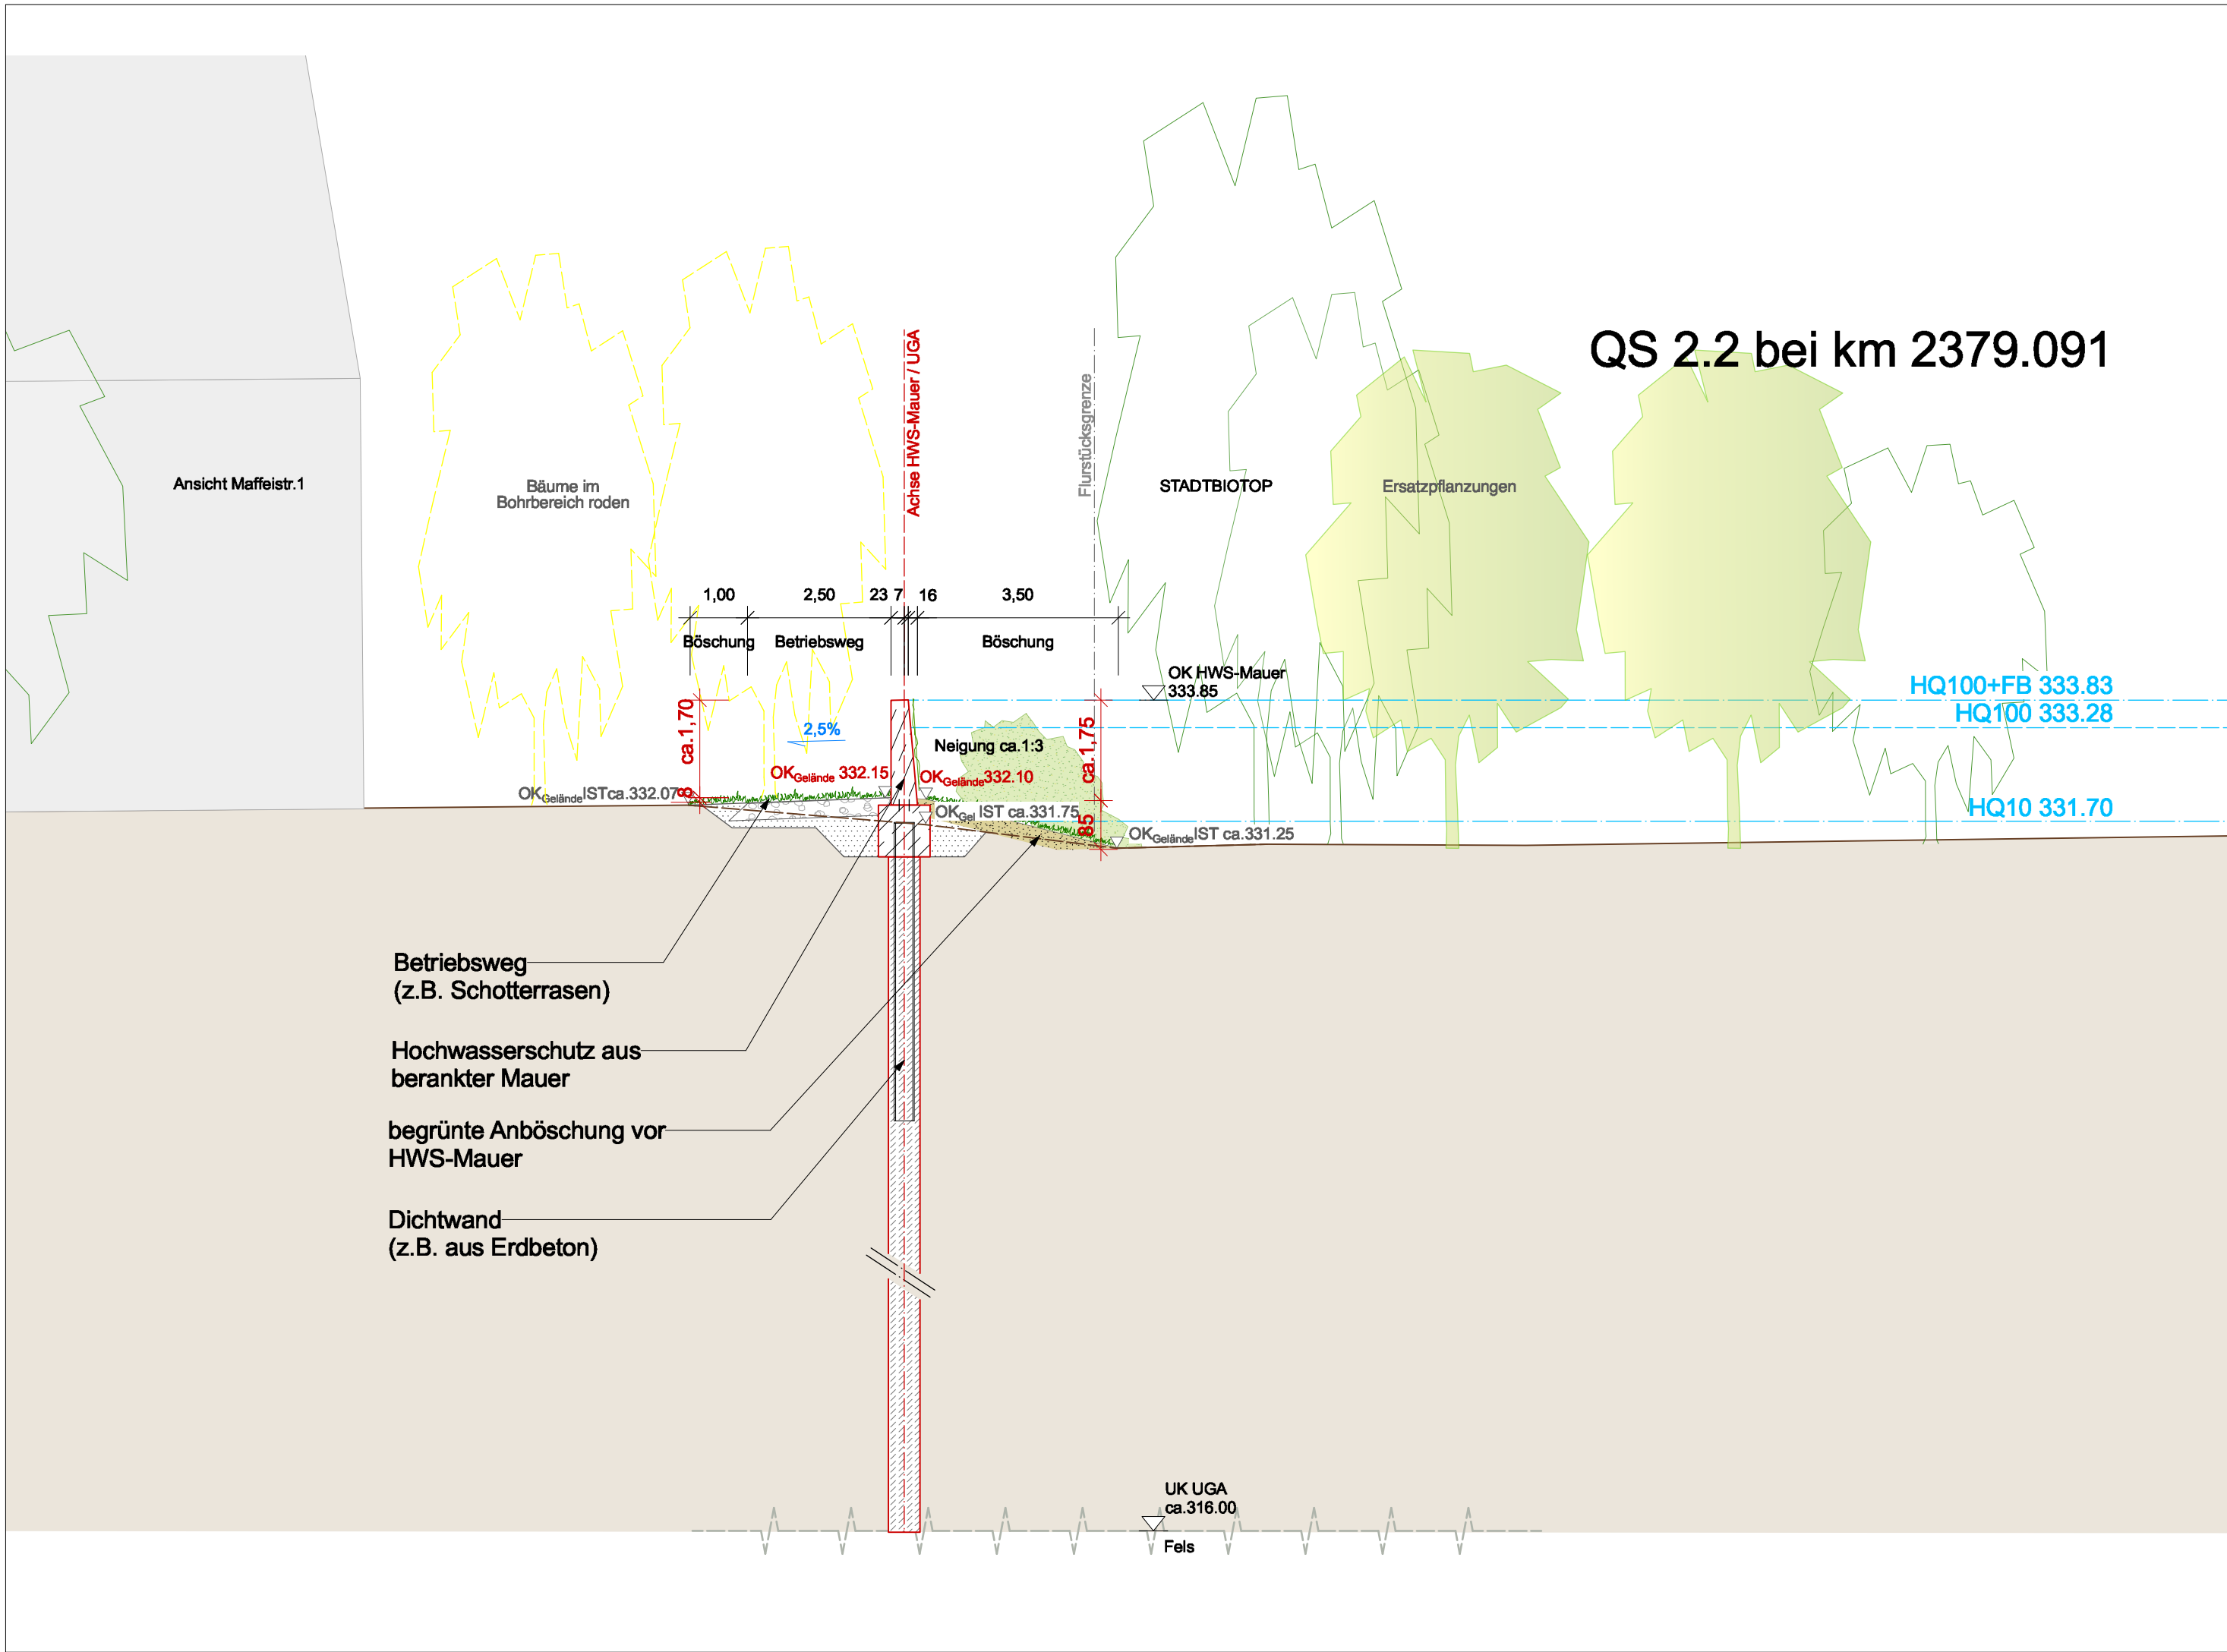

LEGENDE

OK_{Gel} IST 329.71

Abwasser DN300 329.70

Straßenentw. verlegt DN300 329.71

OK_{Gel} 332.50

-0.90

-1.20

-1.50

geplanter Geländeverlauf unterhalb Bestand (Abtrag)

Bestandshöhe
Geländeverlauf im Bestand
mit bestehendem Abwasserkanal/
geplantem Kanal für die Straßen-
entwässerung und bestehender
Versorgertrasse/ Gas/ Trinkwasser

geplante Höhe
geplanter Geländeverlauf
oberhalb Bestand (Aufschüttung)
mit beispielhaftem Bodenaufbau
und beispielhafter neuer
Versorgertrasse/ Gas/ Trinkwasser

geplanter Geländeverlauf
unterhalb Bestand (Abtrag)

Neupflanzung/
Baumbestand

HWS-Maßnahme
(in der Schnittachse)

HWS-Mauer
(in der Ansicht)

Untergrundabdichtung

Gründung

Abbruchmaßnahmen/
Entfall Baumstandort

Vermerke Genehmigungsbehörde :

Wasserwirtschaftsamt
Regensburg

STADT
REGENSBURG

c					
b					
a					
Index	Bemerkung	geändert am	Name	geprüft am	Name

Übersichtslageplan :

Vorhaben :

**Hochwasserschutz Regensburg
Abschnitt H Unterer Wöhrd
PLANFESTSTELLUNG**

Landkreis/ Stadt : Regensburg

Vorhabensträger : Freistaat Bayern, Wasserwirtschaftsamt
Landshuter Straße 59, 9053 Regensburg

Plan-Code : 36200-G-B 2.1.2

Anlage : B 2.1.2	Phase : G
------------------	-----------

Plan-Nr. : RB-H- QS 2.2-100

Vorhabenskennzeichen:
G11 3620001015

Maßstab : M 1:100

Planinhalt : Planabschnitt (PA)2
Querschnitt 2.2, Maffeistr. 1

Lagebezug: GK4 (EPSG 31468)
Höhenbezug: Regensburger Höhennetz aus
1927 in m ü.NN(≠ DHHN12/ 92/
2016 des LDBV)

Planung : **Arbeitsgemeinschaft TEAM 3**

INGENIEURGESELLSCHAFT mbH

architekten und landschaftsarchitekten

Landschafts
architekten

entw. : 3/2024	team 3
gez. : 4/2025	UB
gepr. : 5/2025	WWA

30.04. 2025

Datum

Unterschrift Entwurfsverfasser

26.05. 2025

Datum

Unterschrift Vorhabensträger

QS 2.3 bei km 2379.142

ca. 12,60
Liegewiese

1,80
Uferweg

8,50
Böschung

Pappelreihe
(Bestand)

Flurstücksgrenze

HQ100+FB 333.83
HQ100 333.28

HQ10 331.72

Gefälle ca. 1:5

Gefälle ca. 3,5%

OK_{Böschung} IST 332.63
OK_{Weg} IST 332.92
OK_{Gel.} IST 333.01
OK_{Böschung} IST 332.95
OK_{Weg} 331.64
OK_{Weg} 331.68
OK_{Böschung} = OK_{Wurzel} 332.58

Uferweg
(z.B. Schotterrasen)

Geländeabtrag
(Retentionsraumvergrößerung)

begrünte Anböschung vor
HWS-Mauer

Hochwasserschutz aus
berankter Mauer

Dichtwand
(z.B. aus Erdbeton)

Betriebsweg/ Parkplatz Jakobigelände
(wieder-)herstellen nach Geländeauftrag
(z.B. Schotter, Asphalt)

STADTBIOTOP

2,30
Böschung

15,30
Überstand

4,30
Stpl.

5,60
Fahrgasse (Asphalt)

4,30
Stpl.

OK HWS-Mauer 333.85
OK_{Gel.} IST 331.73
UK_{Böschung} 331.70
OK_{Gel.} IST 331.60
OK_{Gelände} 332.60
OK_{Gelände} 332.52

Achse HWS-Mauer / UGA

UK UGA
ca. 314.00
Fels

Das Diagramm zeigt zwei Kurven für die Gelkonzentration C_{Gel} über der Gelzeit t_R . Die Kurve für 'Abwasser' (rot) hat eine höhere Gelkonzentration bei einer Gelzeit von 329,71 Minuten im Vergleich zur Kurve für 'Straßenentw.' (blau). Die Gelkonzentrationen sind als C_{Gel} markiert, und die Gelzeiten sind als t_R markiert.



HWS-Maßnahme
(in Schnittachse)

Untergrundabdichtung

 **Gründung**

**Abbruchmaßnahmen/
Entfall Baumstandort**


Wasserwirtschaftsamt
Regensburg



STADT  REGENSBURG

c					
b					
a					
Index	Bemerkung	geändert am	Name	geprüft am	Name

Übersichtslageplan :

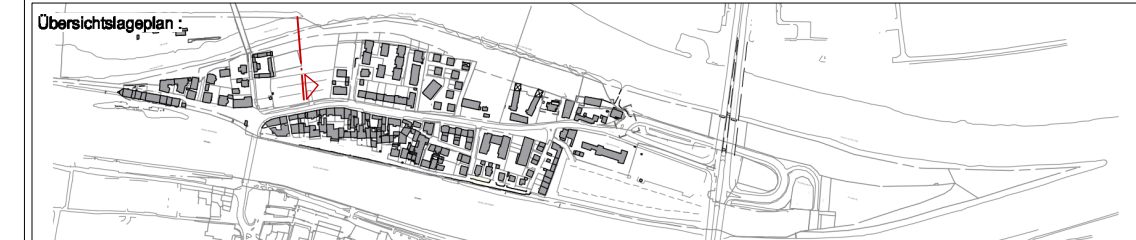

**Hochwasserschutz Regensburg
Abschnitt H Unterer Wöhrd
PLANFESTSTELLUNG**

Plan-Code: 36200-G-B 2.1.3

Anlage : **B 2.1.3**Phase : **G**

Regensburg

Freistaat Bayern, Wasserwirtschaftsamt
Landshuter Straße 59, 9053 Regensburg

Plan-Nr. :

RB-H-QS 2.3-100

Vorhabenskennzeichen:
G1t 3620001015

Maßstab :
M 1:100

Planinhalt: Planabschnitt (PA)2
Querschnitt 2.3, Jakobigelände

Lagebezug: GK4 (EPSG 31468)

Höhenbezug: Regensburger Höhennetz aus 1927 in m ü.NN (≠ DHHN12/ 92/ 2016 des LDBV)

Arbeitsgemeinschaft TEAM 3



INGENIEURGESELLSCHAFT mbH

ARCHISCAP
architekten und landschaftsarchitekten



entw. :	3/2024
---------	--------

3/2024

team 3

gez. :

4/2025

UB

gepr. :

5/2025

WWA

30.04. 2025




Datum	
-------	--

Unterschrift Entwurfsverfasser

26.05. 2025

Datum

Unterschrift Vorhabensträger

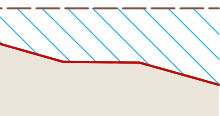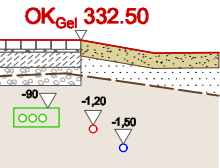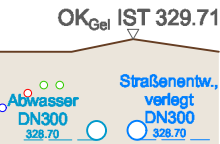

Bestandshöhe
Geländeverlauf im Bestand
mit bestehendem Abwasserkanal/
geplantem Kanal für die Straßen-
entwässerung und bestehender
Versorgertrasse/ Gas/ Trinkwasser

geplante Höhe
geplanter Geländeverlauf
oberhalb Bestand (Aufschüttung)
mit beispielhaftem Bodenaufbau
und beispielhafter neuer
Versorgertrasse/ Gas/ Trinkwasser

geplanter Geländeeverlauf
unterhalb Bestand (Abtrag)

**Neupflanzung
Baumbestand**

HWS-Maßnahme
(in Schnittachse)



HWS-Mauer
(in der Ansicht)

 Untergrundabdichtung

 **Gründung**


Abbruchmaßnahmen
Entfall Baumstandort

Vermerke Genehmigungsbehörde :



STADT
REGENSBURG

c					
b					
a					
Index	Bemerkung	geändert am	Name	geprüft am	Name

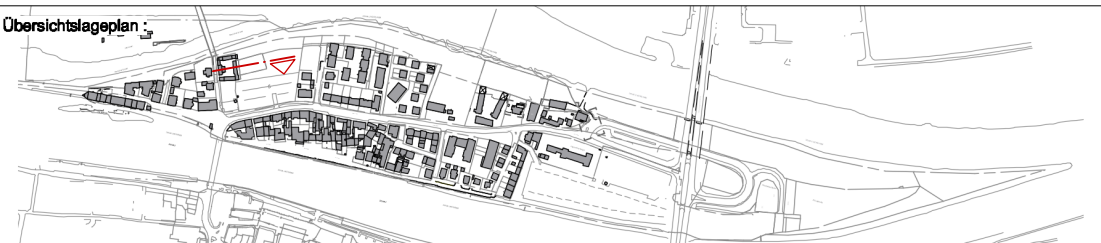

Vorhaben :		Hochwasserschutz Regensburg Abschnitt H Unterer Wöhrd PLANFESTSTELLUNG	
Landkreis/ Stadt :		Regensburg	
Vorhabenträger :		Freistaat Bayern, Wasserwirtschaftsamt Landshuter Straße 59, 9053 Regensburg	
Maßstab :		Planinhalt: Planabschnitt (PA)2 Querschnitt 2.4, Proskestr.4 Hinterhaus	
M 1:100			
Planung :		Arbeitsgemeinschaft TEAM 3	
 INGENIEURGESELLSCHAFT mbH		 architekten und landschaftsarchitekten	
		 Landschaftsarchitekten	
Plan-Code :		36200-G-B 2.1.4	
Anlage :		B 2.1.4	Phase : G
Plan-Nr. :		RB-H-QS 2.4-100	
Vorhabenskennzeichen:		Glt 3620001015	
Lagebezug:		GK4 (EPSG 31468)	
Höhenbezug:		Regensburgburger Höhennetz, aus 1927 in m ü.NN (= DHN12/ 92/ 2016 des LDBV)	
entw. :		3/2024	team 3
gez. :		4/2025	UB
gepr. :		5/2025	WWA


30.04. 2025
Datum

Unterschrift Entwurfsverfasser




26.05. 2025

Unterschrift Vorhabensträger

QS 2.5 Brandner Kanal

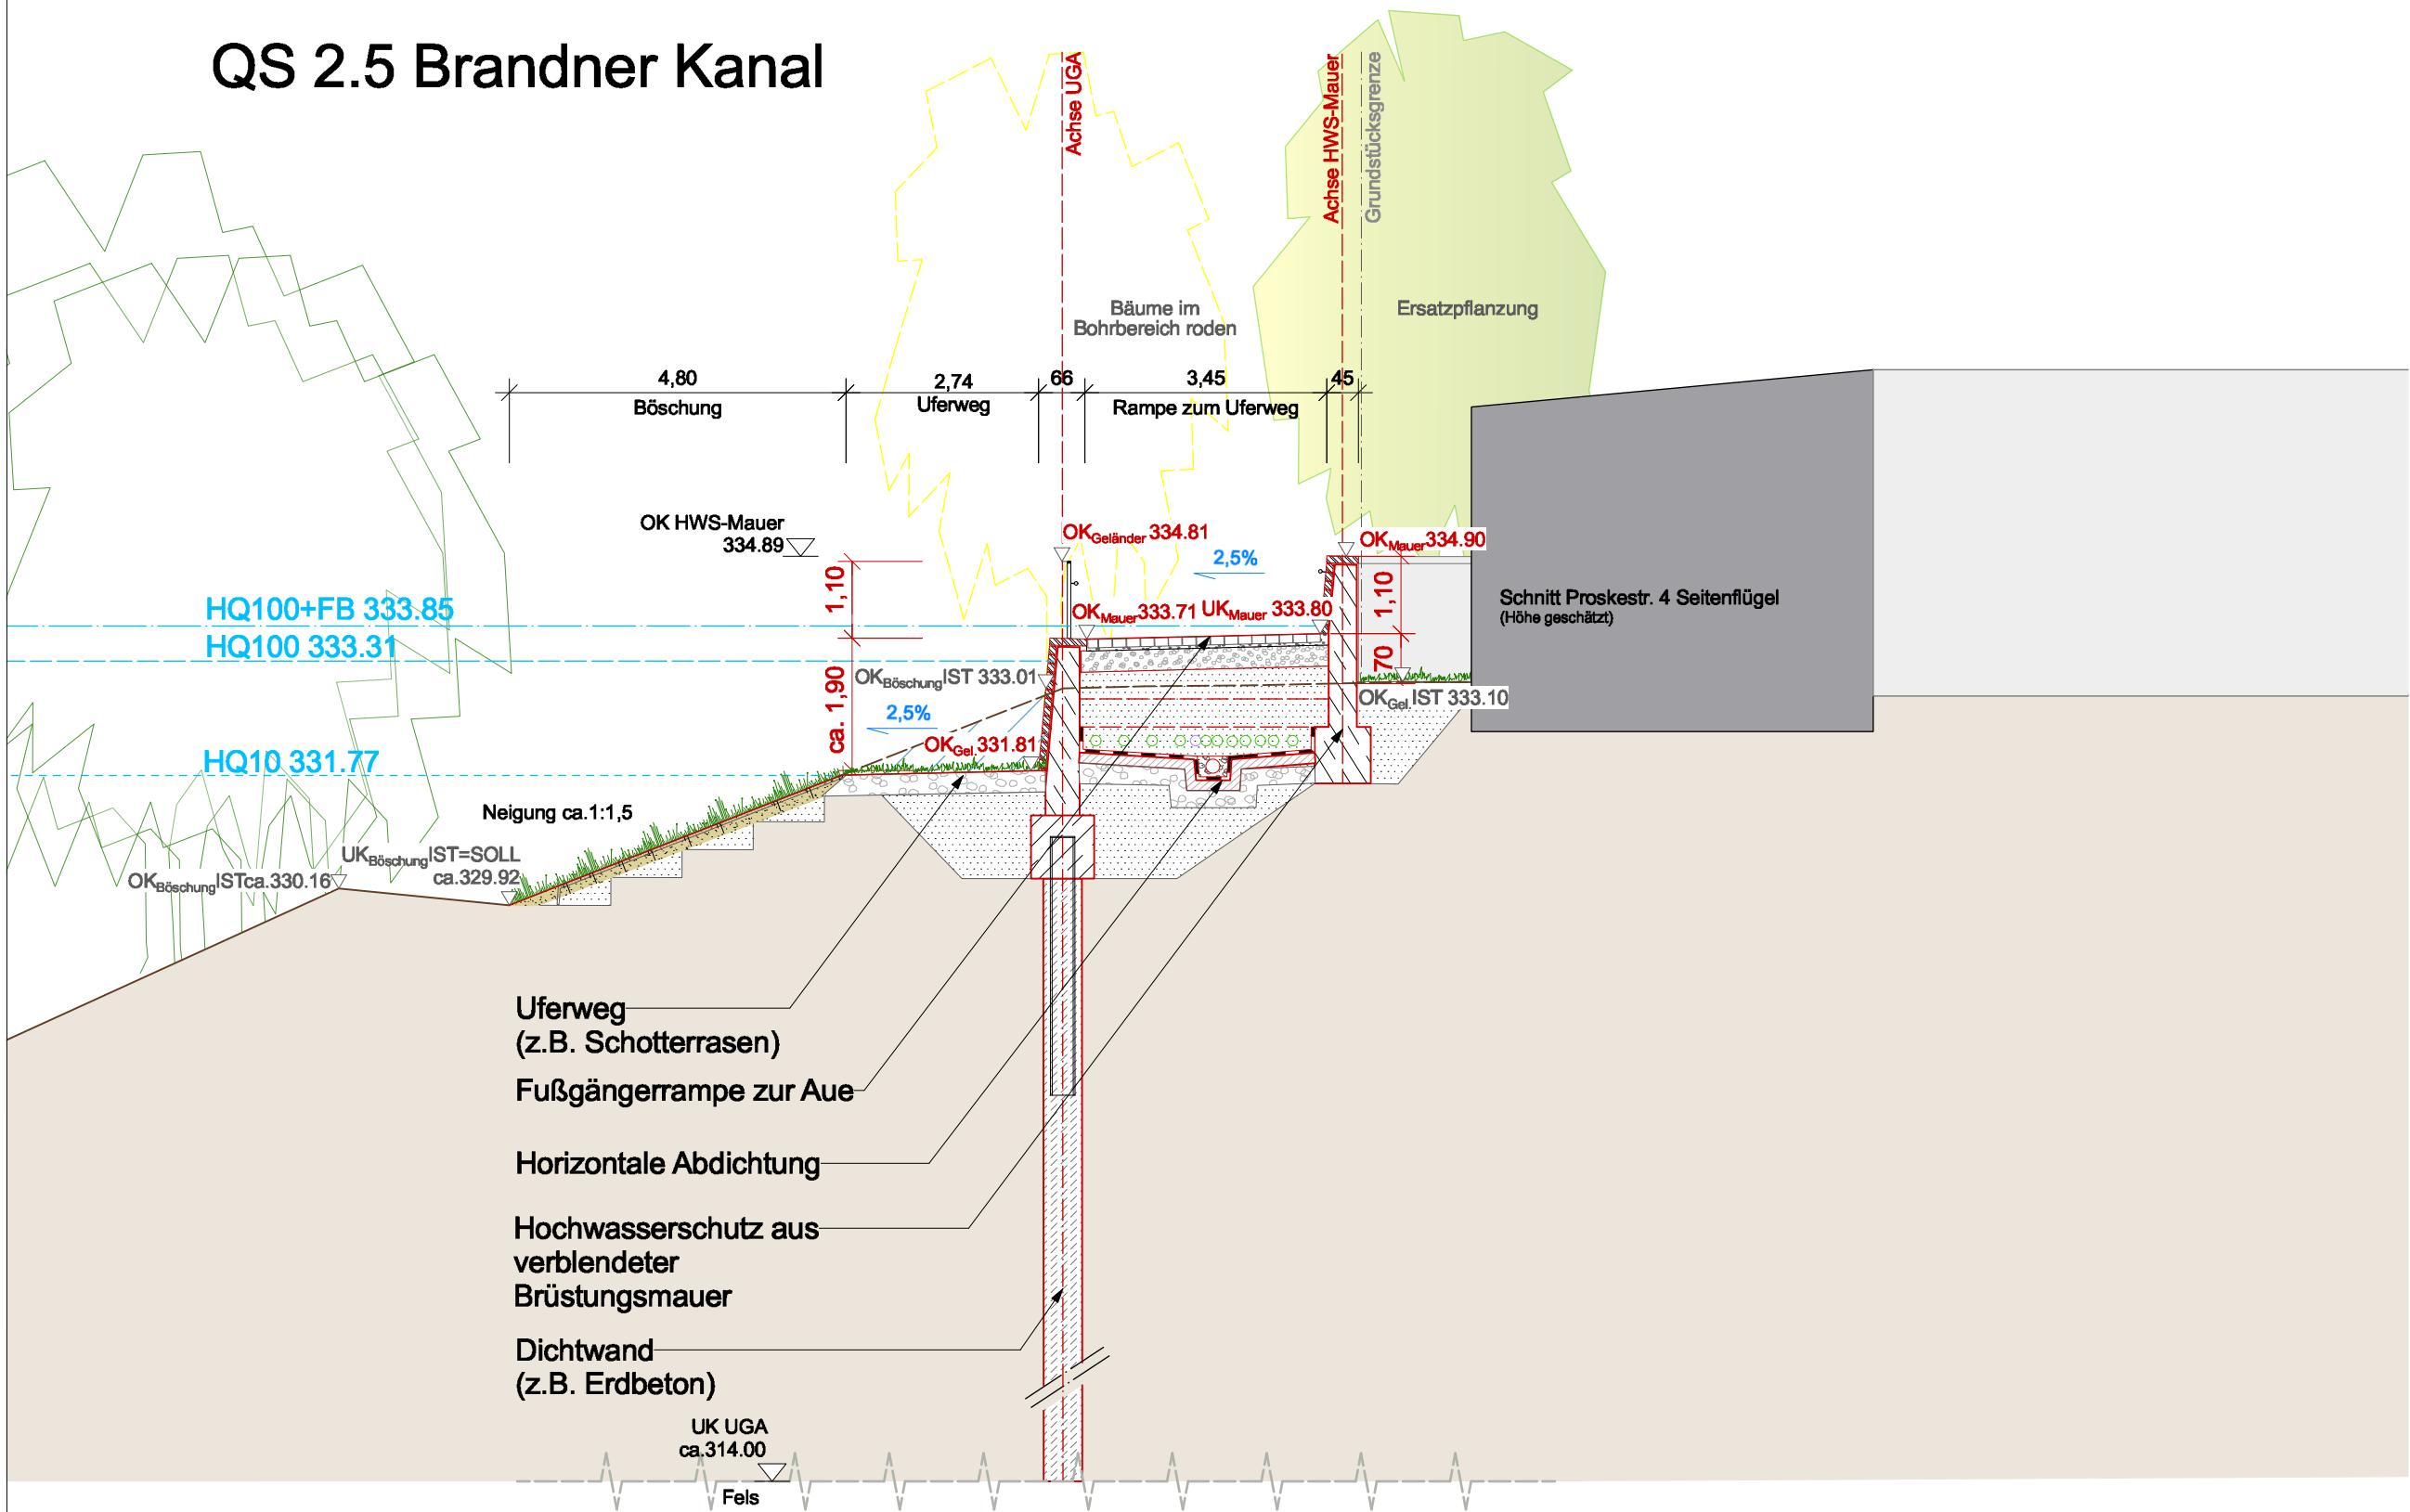




LEGENDE

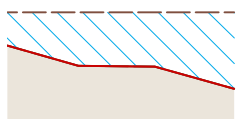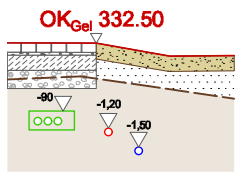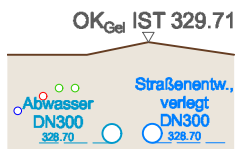

Bestandshöhe
Geländeverlauf im Bestand
mit bestehendem Abwasserkanal/
geplantem Kanal für die Straßen-
entwässerung und bestehender
Versorgertrasse/ Gas/ Trinkwasser

geplante Höhe
geplanter Geländeverlauf
oberhalb Bestand (Aufschüttung)
mit beispielhaftem Bodenaufbau
und beispielhafter neuer
Versorgertrasse/ Gas/ Trinkwasser

geplanter Geländeverlauf
unterhalb Bestand (Abtrag)

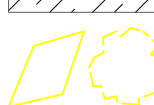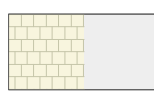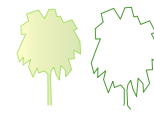

Neupflanzung/ Baumbestand

HWS-Maßnahme
(in Schnittachse)

HWS-Mauer
(in der Ansicht)

Untergrundabdichtung

Gründung

Abbruchmaßnahmen/ Entfall Baumstandort

Vermerke Genehmigungsbehörde :

c					
b					
a					
Index	Bemerkung	geändert am	Name	geprüft am	Name

Übersichtslageplan :

Vorhaben : **Hochwasserschutz Regensburg**
Abschnitt H Unterer Wöhrd
PLANFESTSTELLUNG

Landkreis/ Stadt : **Regensburg**
Vorhabensträger : **Freistaat Bayern, Wasserwirtschaftsamt**
Landshuter Straße 59, 9053 Regensburg

Maßstab : **M 1:100**

Planung : **Arbeitsgemeinschaft TEAM 3**

Plan-Code : **36200-G-B 2.1.5**
Anlage : **B 2.1.5** Phase : **G**
Plan-Nr. : **RB-H-QS 2.5-100**
Vorhabenskennzeichen : **G1t 3620001015**

Lagebezug : **GK4 (EPSG 31468)**
Höhenbezug : **Regensburger Höhennetz aus 1927 in m ü.NN(≠ DHHN12/ 92/ 2016 des LDBV)**

entw. : **3/2024** team **3**
gez. : **4/2025** **UB**
gepr. : **5/2025** **WWA**

Datum **30.04. 2025** Unterschrift Entwurfsverfasser
Datum **26.05. 2025** Unterschrift Vorhabensträger