

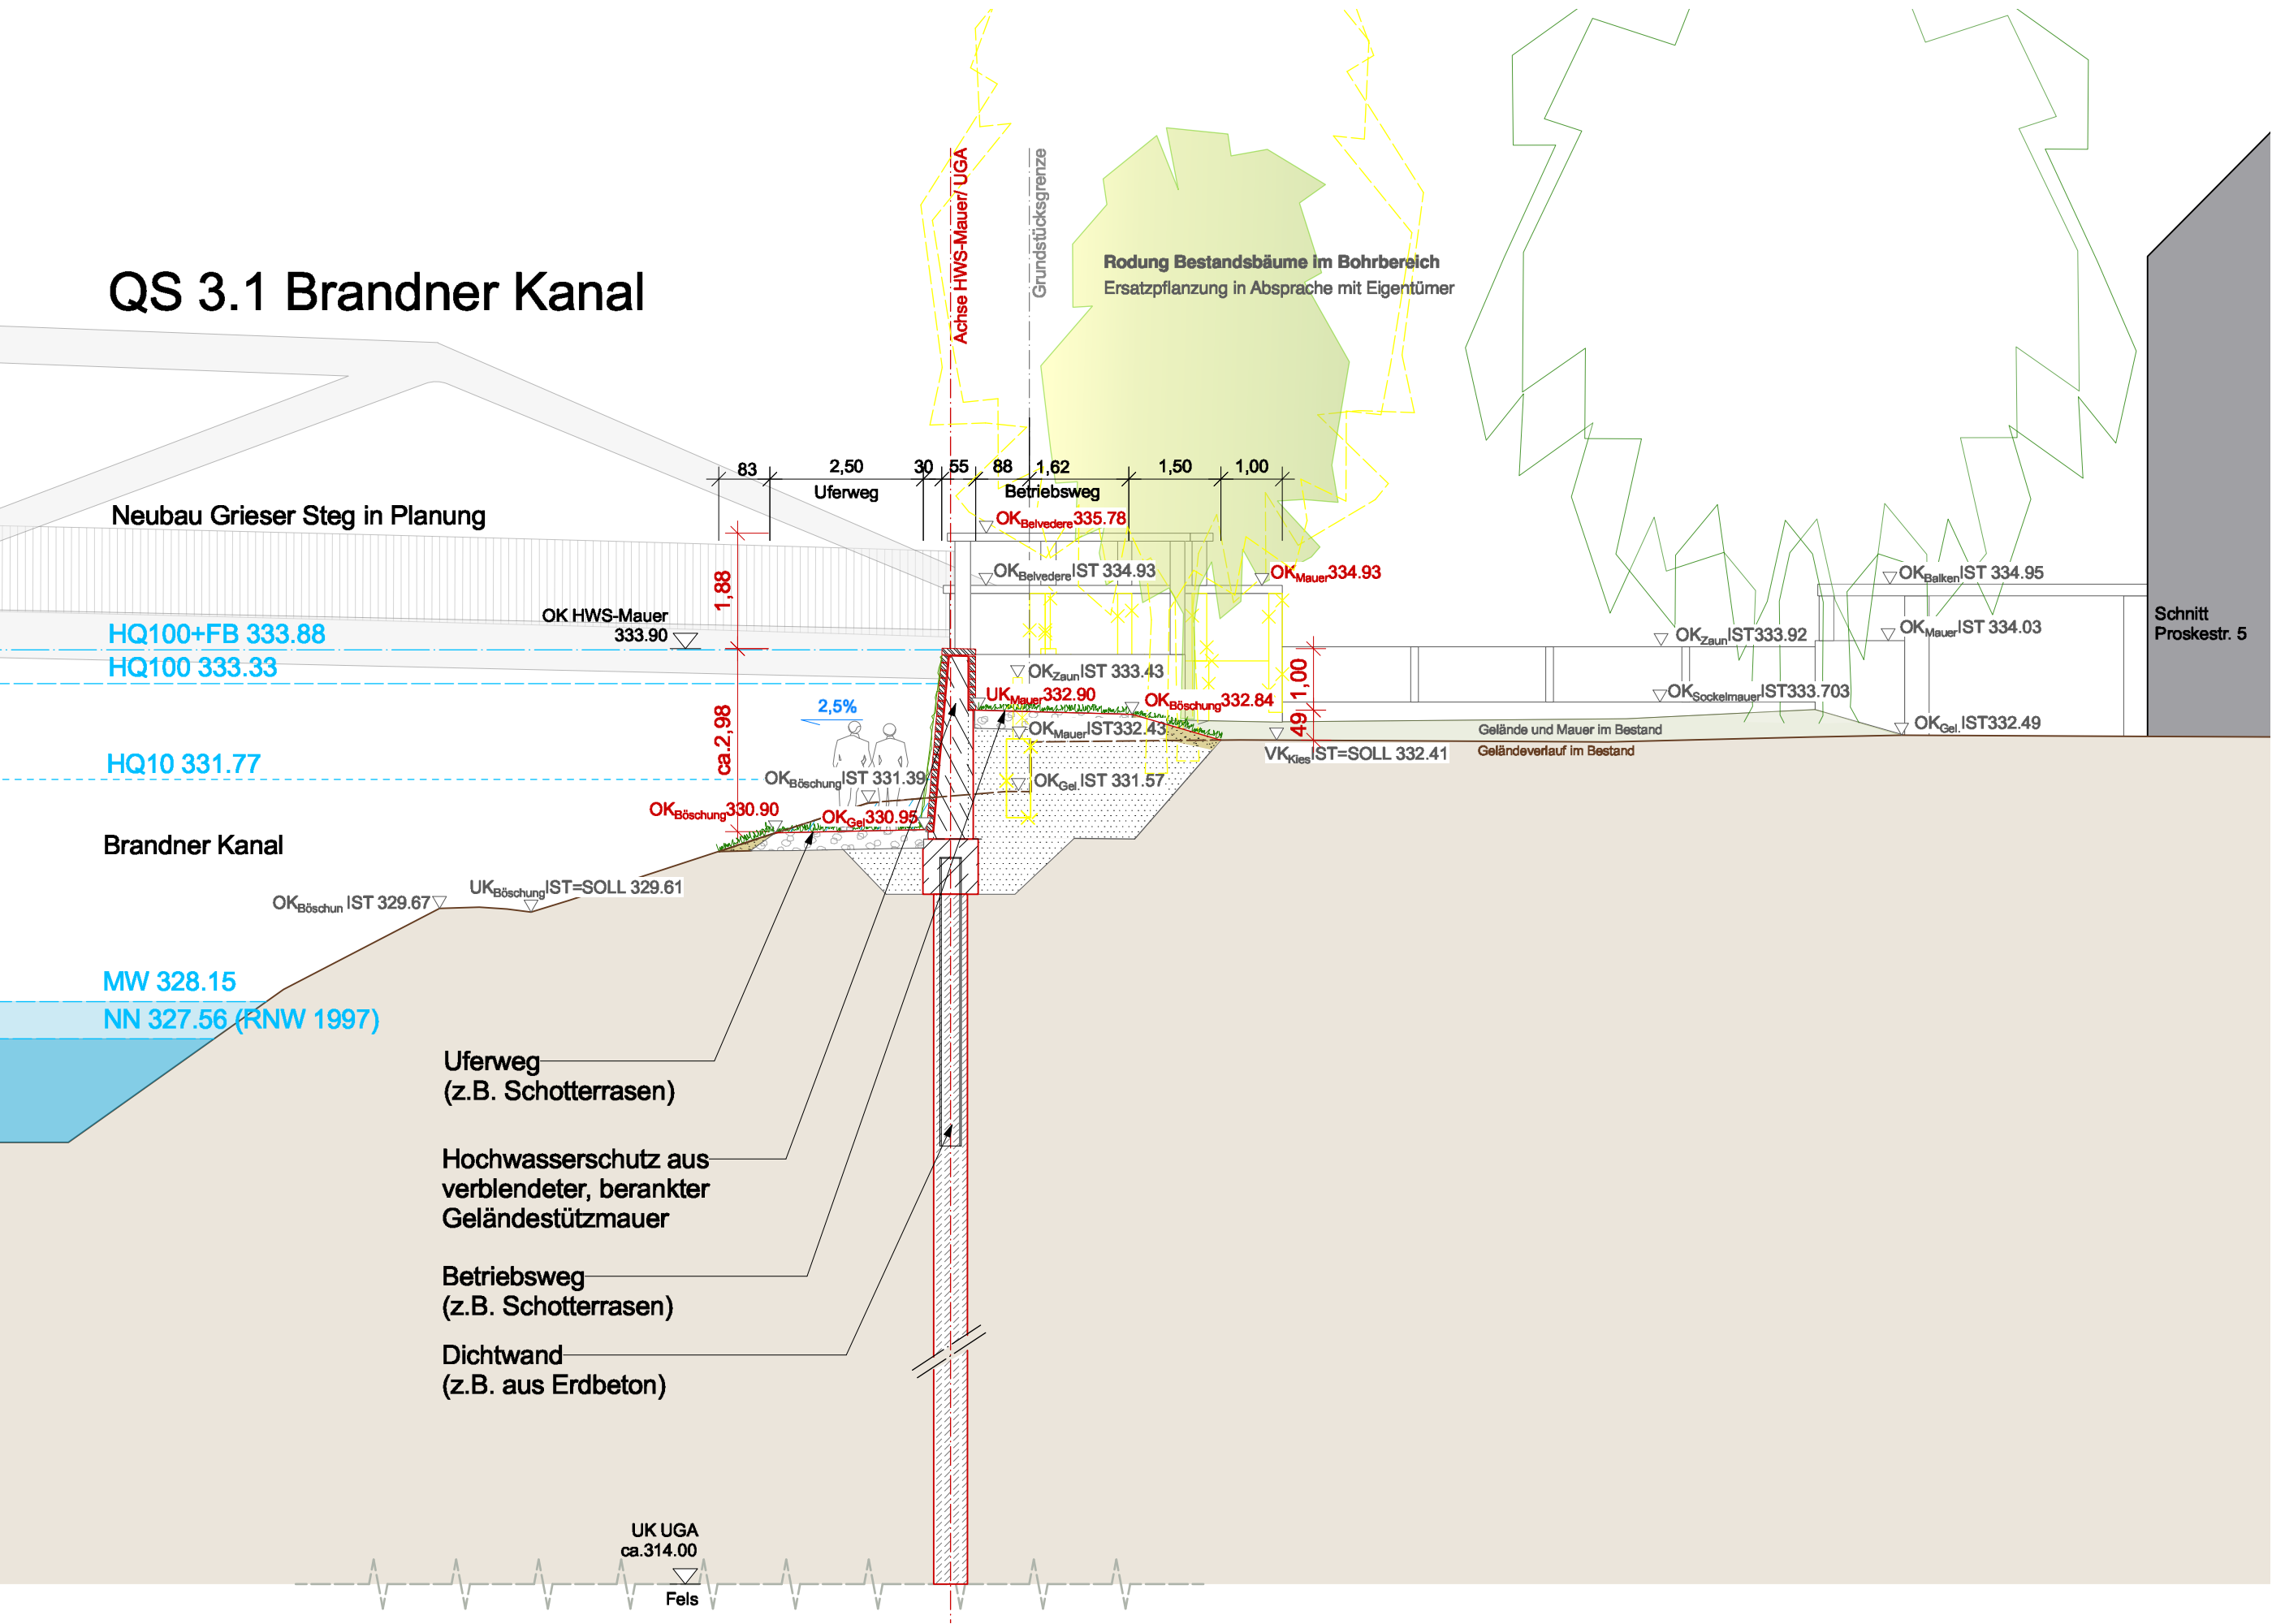
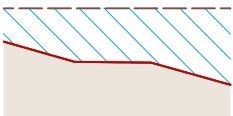


QS 3.1 Brandner Kanal

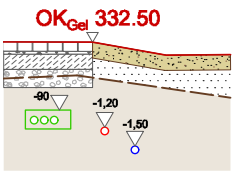




LEGENDE

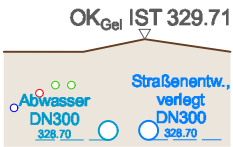

Bestandshöhe
Geländeverlauf im Bestand
mit bestehendem Abwasserkanal/
geplantem Kanal für die Straßen-
entwässerung und bestehender
Versorgertrasse/ Gas/ Trinkwasser

geplante Höhe
geplanter Geländeverlauf
oberhalb Bestand (Aufschüttung)
mit beispielhaftem Bodenaufbau
und beispielhafter neuer
Versorgertrasse/ Gas/ Trinkwasser

geplanter Geländeverlauf
unterhalb Bestand (Abtrag)

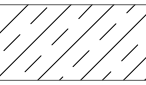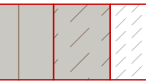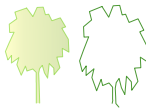

Neupflanzung/
Baumbestand

HWS-Maßnahme
(in Schnittachse)

HWS-Mauer
(in der Ansicht)

Untergrundabdichtung


Gründung

Abbruchmaßnahmen/
Entfall Baumstandort

Vermerke Genehmigungsbehörde :




c					
b					
a					
Index	Bemerkung	geändert am	Name	geprüft am	Name

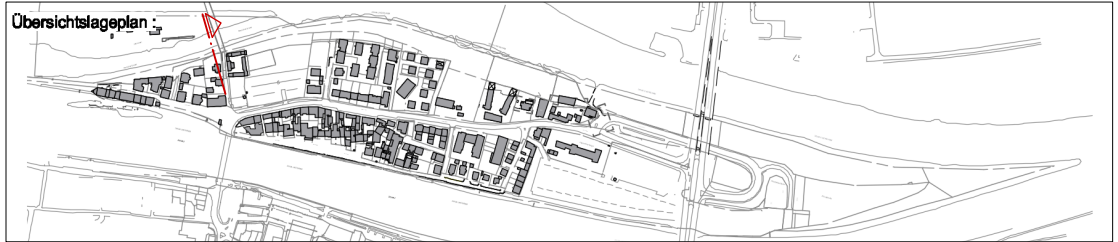


Vorhaben :		Hochwasserschutz Regensburg Abschnitt H Unterer Wöhrd PLANFESTSTELLUNG		Plan-Code : 36200-G-B 3.1.1			
Landkreis/ Stadt :		Regensburg		Anlage :	B 3.1.1	Phase :	G
Vorhabensträger :		Freistaat Bayern, Wasserwirtschaftsamt Landshuter Straße 59, 9053 Regensburg		Plan-Nr. : RB-H- QS 3.1-100			
				Vorhabenskennzeichen: G1t 3620001015			
Maßstab :		Planinhalt : Planabschnitt (PA)3 Querschnitt 3.1, Proskestr. 5		Lagebezug: GK4 (EPSG 31468)			
M 1:100				Höhenbezug: Regensburger Höhennetz aus 1927 in m ü.NN (≠ DHHN12/ 92/ 2016 des LDBV)			
Planung :		Arbeitsgemeinschaft TEAM 3		entw. : 3/2024 team 3			
schönmigplan INGENIEURGESELLSCHAFT mbH		archiscapē architekten und landschaftsarchitekten		gez. : 4/2025 UB			
		bmr. Landschaftsarchitekten		gepr. : 5/2025 WWA			

30.04. 2025 Datum	Unterschrift Entwurfsverfasser	26.05. 2025 Datum	Unterschrift Vorhabensträger
----------------------	--------------------------------	----------------------	------------------------------

QS 3.2 Brandner Kanal

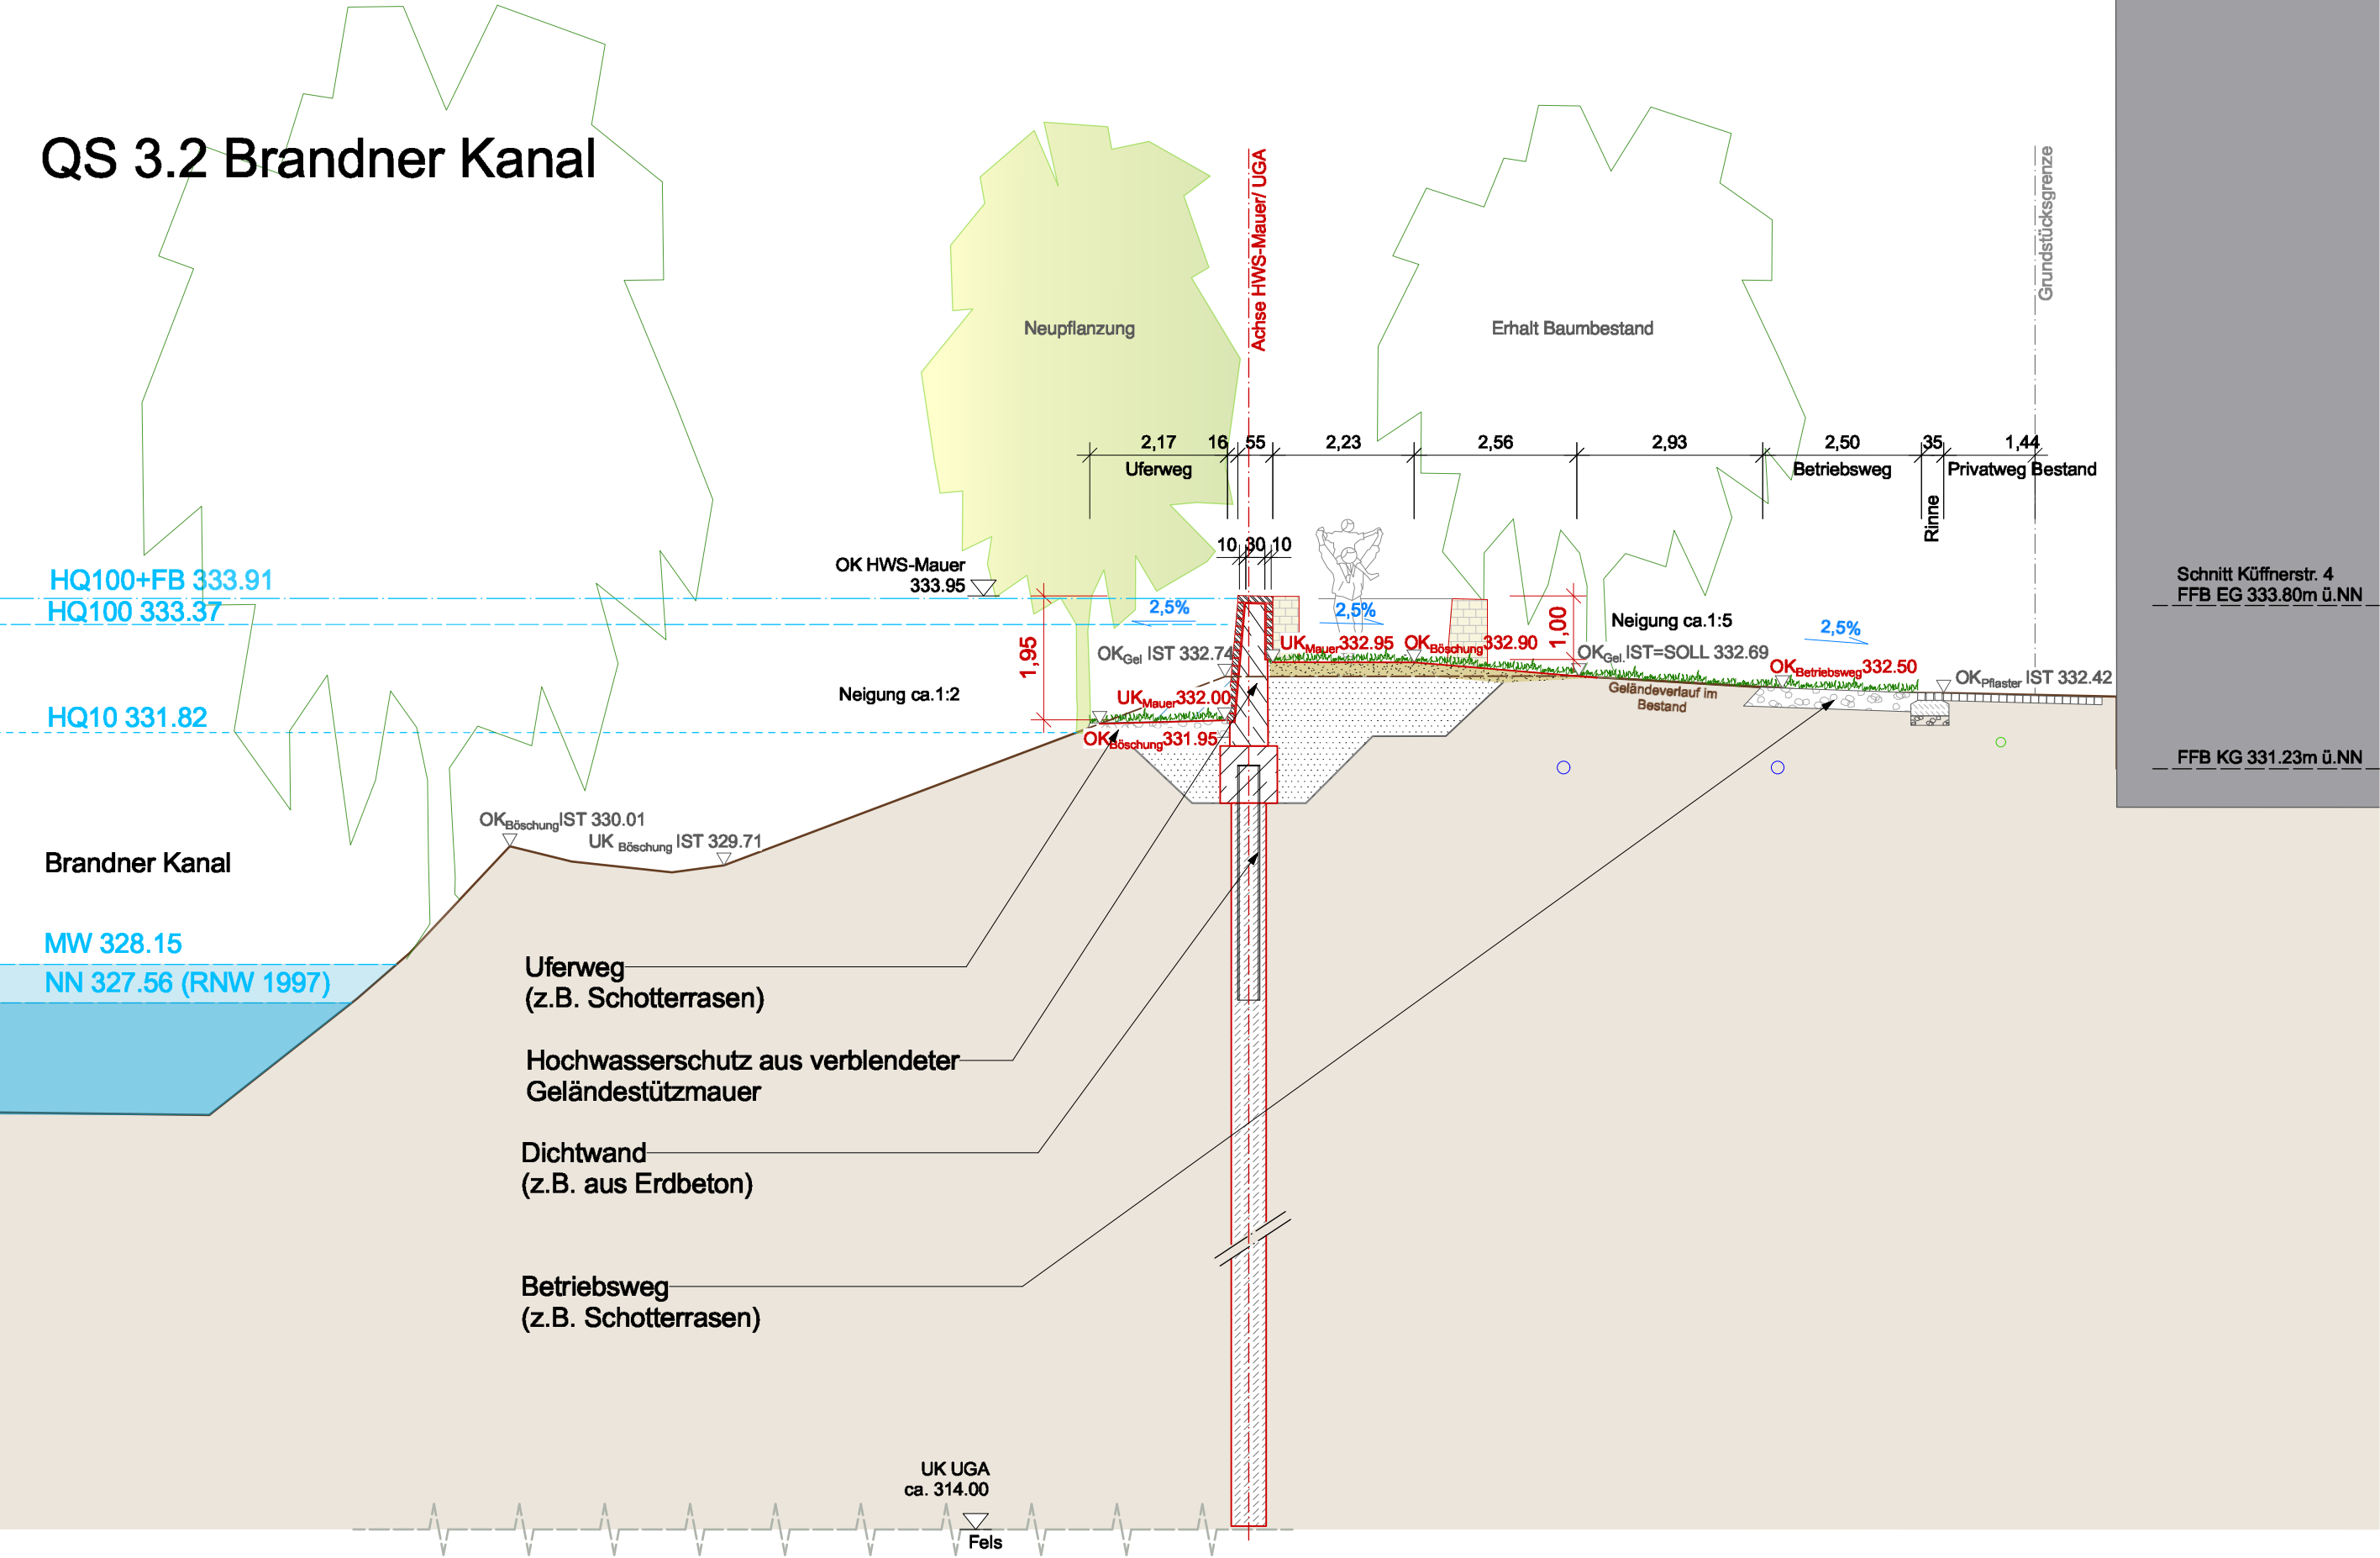

LEGENDE

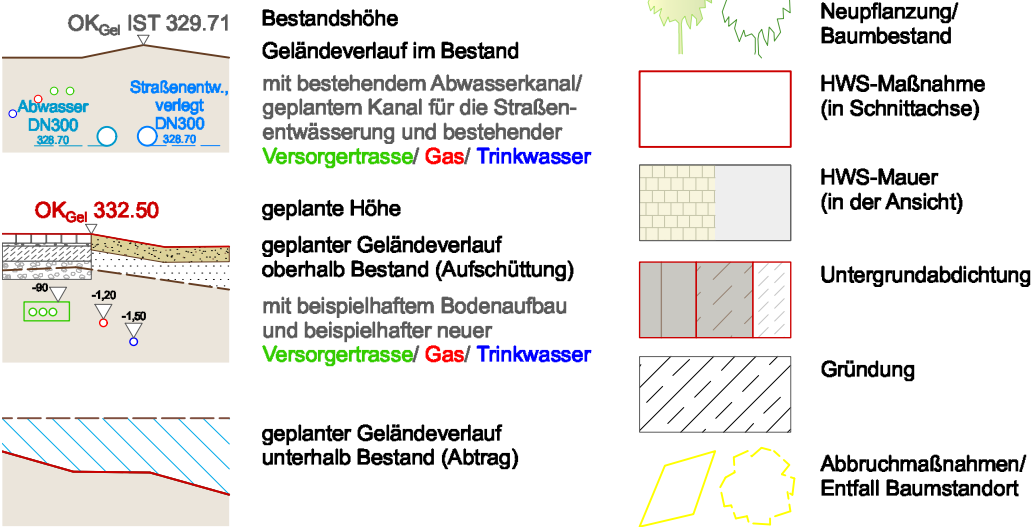


Vermerke Genehmigungsbehörde :





STADT
REGENSBURG

c					
b					
a					
Index	Bemerkung	geändert am	Name	geprüft am	Name

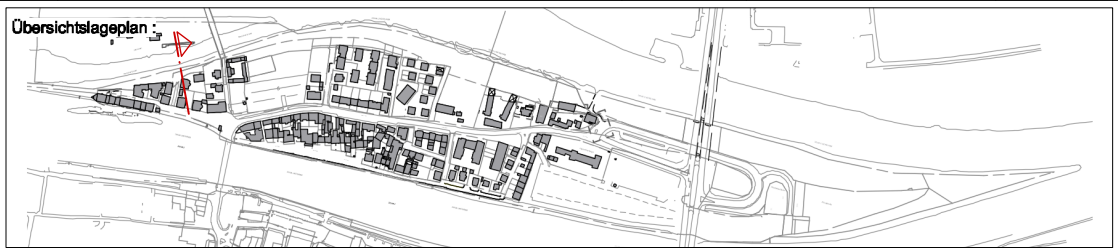

Vorhaben :	Hochwasserschutz Regensburg Abschnitt H Unterer Wöhrd PLANFESTSTELLUNG	Plan-Code : 36200-G-B 3.1.2			
		Anlage :	B 3.1.2	Phase :	G
Landkreis/ Stadt :	Regensburg	Plan-Nr. : RB-H- QS 3.2-100			
Vorhabensträger :		Vorhabenskennzeichen: G11 3620001015			
Maßstab :	M 1:100	Lagebezug: GK4 (EPSG 31468)			
		Höhenbezug: Regensburger Höhennetz aus 1927 in m ü.NN(≠ DHH-N12/ 92/ 2016 des LDBV)			
Planung :	Arbeitsgemeinschaft TEAM 3	entw. : 3/2024 team 3			
		gez. : 4/2025 UB			
		gepr. : 5/2025 WWA			


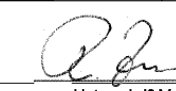
30.04. 2025 Datum	 Unterschrift Entwurfsverfasser	26.05. 2025 Datum	 Unterschrift Vorhabensträger
----------------------	---	----------------------	---

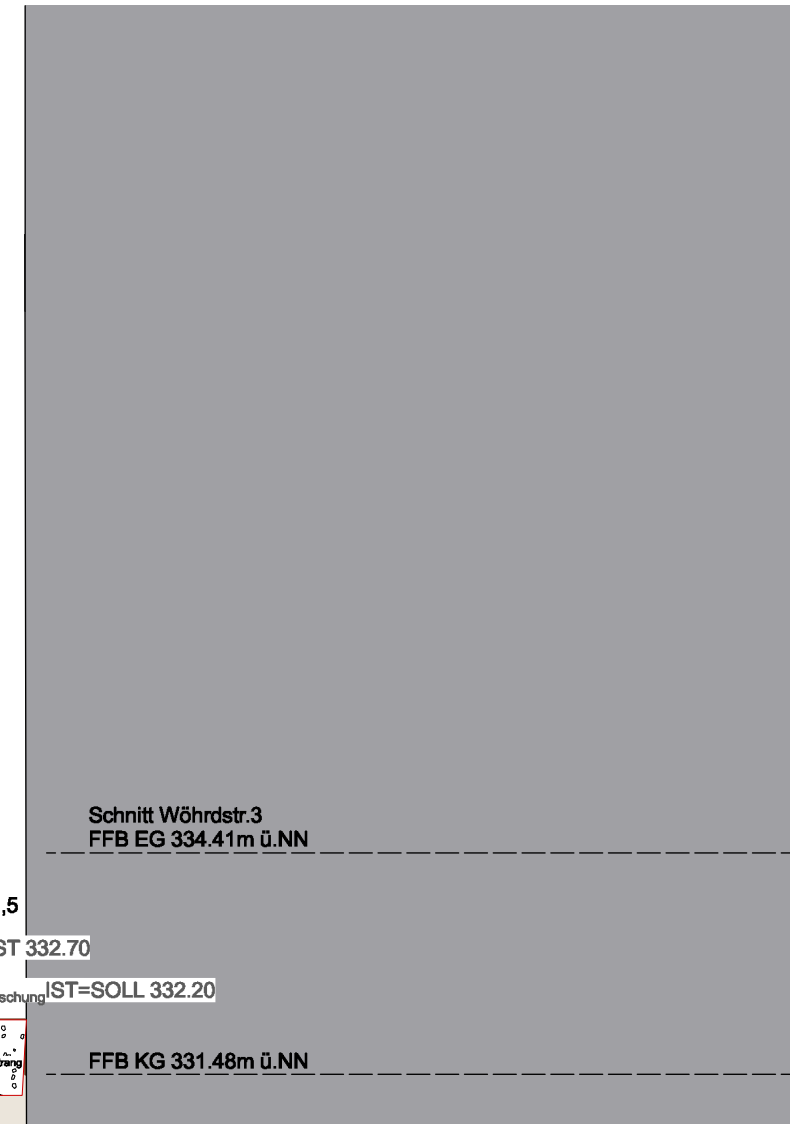[illegible]


OK_{Gel} IST 329.71

Abwasser DN300 329.70

Straßenentw., verlegt DN300 329.70

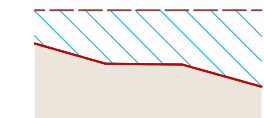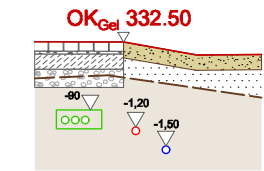

geplanter Geländeverlauf
unterhalb Bestand (Abtrag)

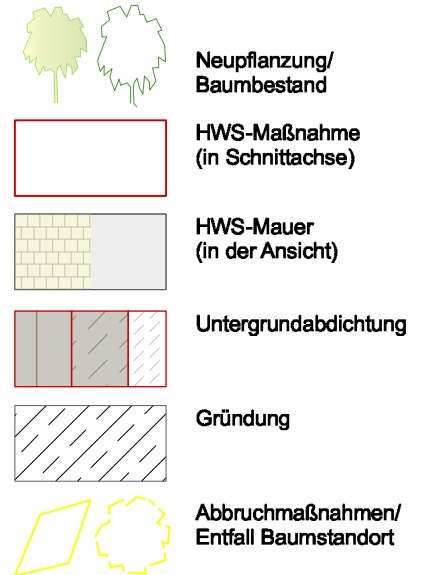

Wasserwirtschaftsamt
Regensburg



**STADT
REGENSBURG**

c					
b					
a					
Index	Bemerkung	geändert am	Name	geprüft am	Name




Vorhaben : Hochwasserschutz Regensburg Abschnitt H Unterer Wöhrd PLANFESTSTELLUNG		Plan-Code : 36200-G-B 3.1.3	
		Anlage : B 3.1.3	Phase : G
		Plan-Nr. : RB-H-QS 3.3-100	
		Vorhabenskennzeichen: Glt 3620001015	
Landkreis/ Stadt : Vorhabensträger :	Regensburg Freistaat Bayern, Wasserwirtschaftsamt Landshuter Straße 59, 9053 Regensburg		
Maßstab : M 1:100	Planinhalt : Planabschnitt (PA)3 Querschnitt 3.3, Wöhrdstr. 3		Lagebezug: GK4 (EPSG 31468) Höhenbezug: Regensburger Höhennetz aus 1927 in m ü.NN(≠ DHHN12/ 92/ 2016 des LDBV)


Planung : Arbeitsgemeinschaft TEAM 3  INGENIEURGESELLSCHAFT mbH	 architekten und landschaftsarchitekten	 Landschaftsarchitekten	entw. :	3/2024	team 3
			gez. :	4/2025	UB
			gepr. :	5/2025	WWA

30.04.2025		26.05.2025	
Datum	Unterschrift Entwurfsverfasser	Datum	Unterschrift Vorhabensträger


QS 3.4 Brandner Kanal

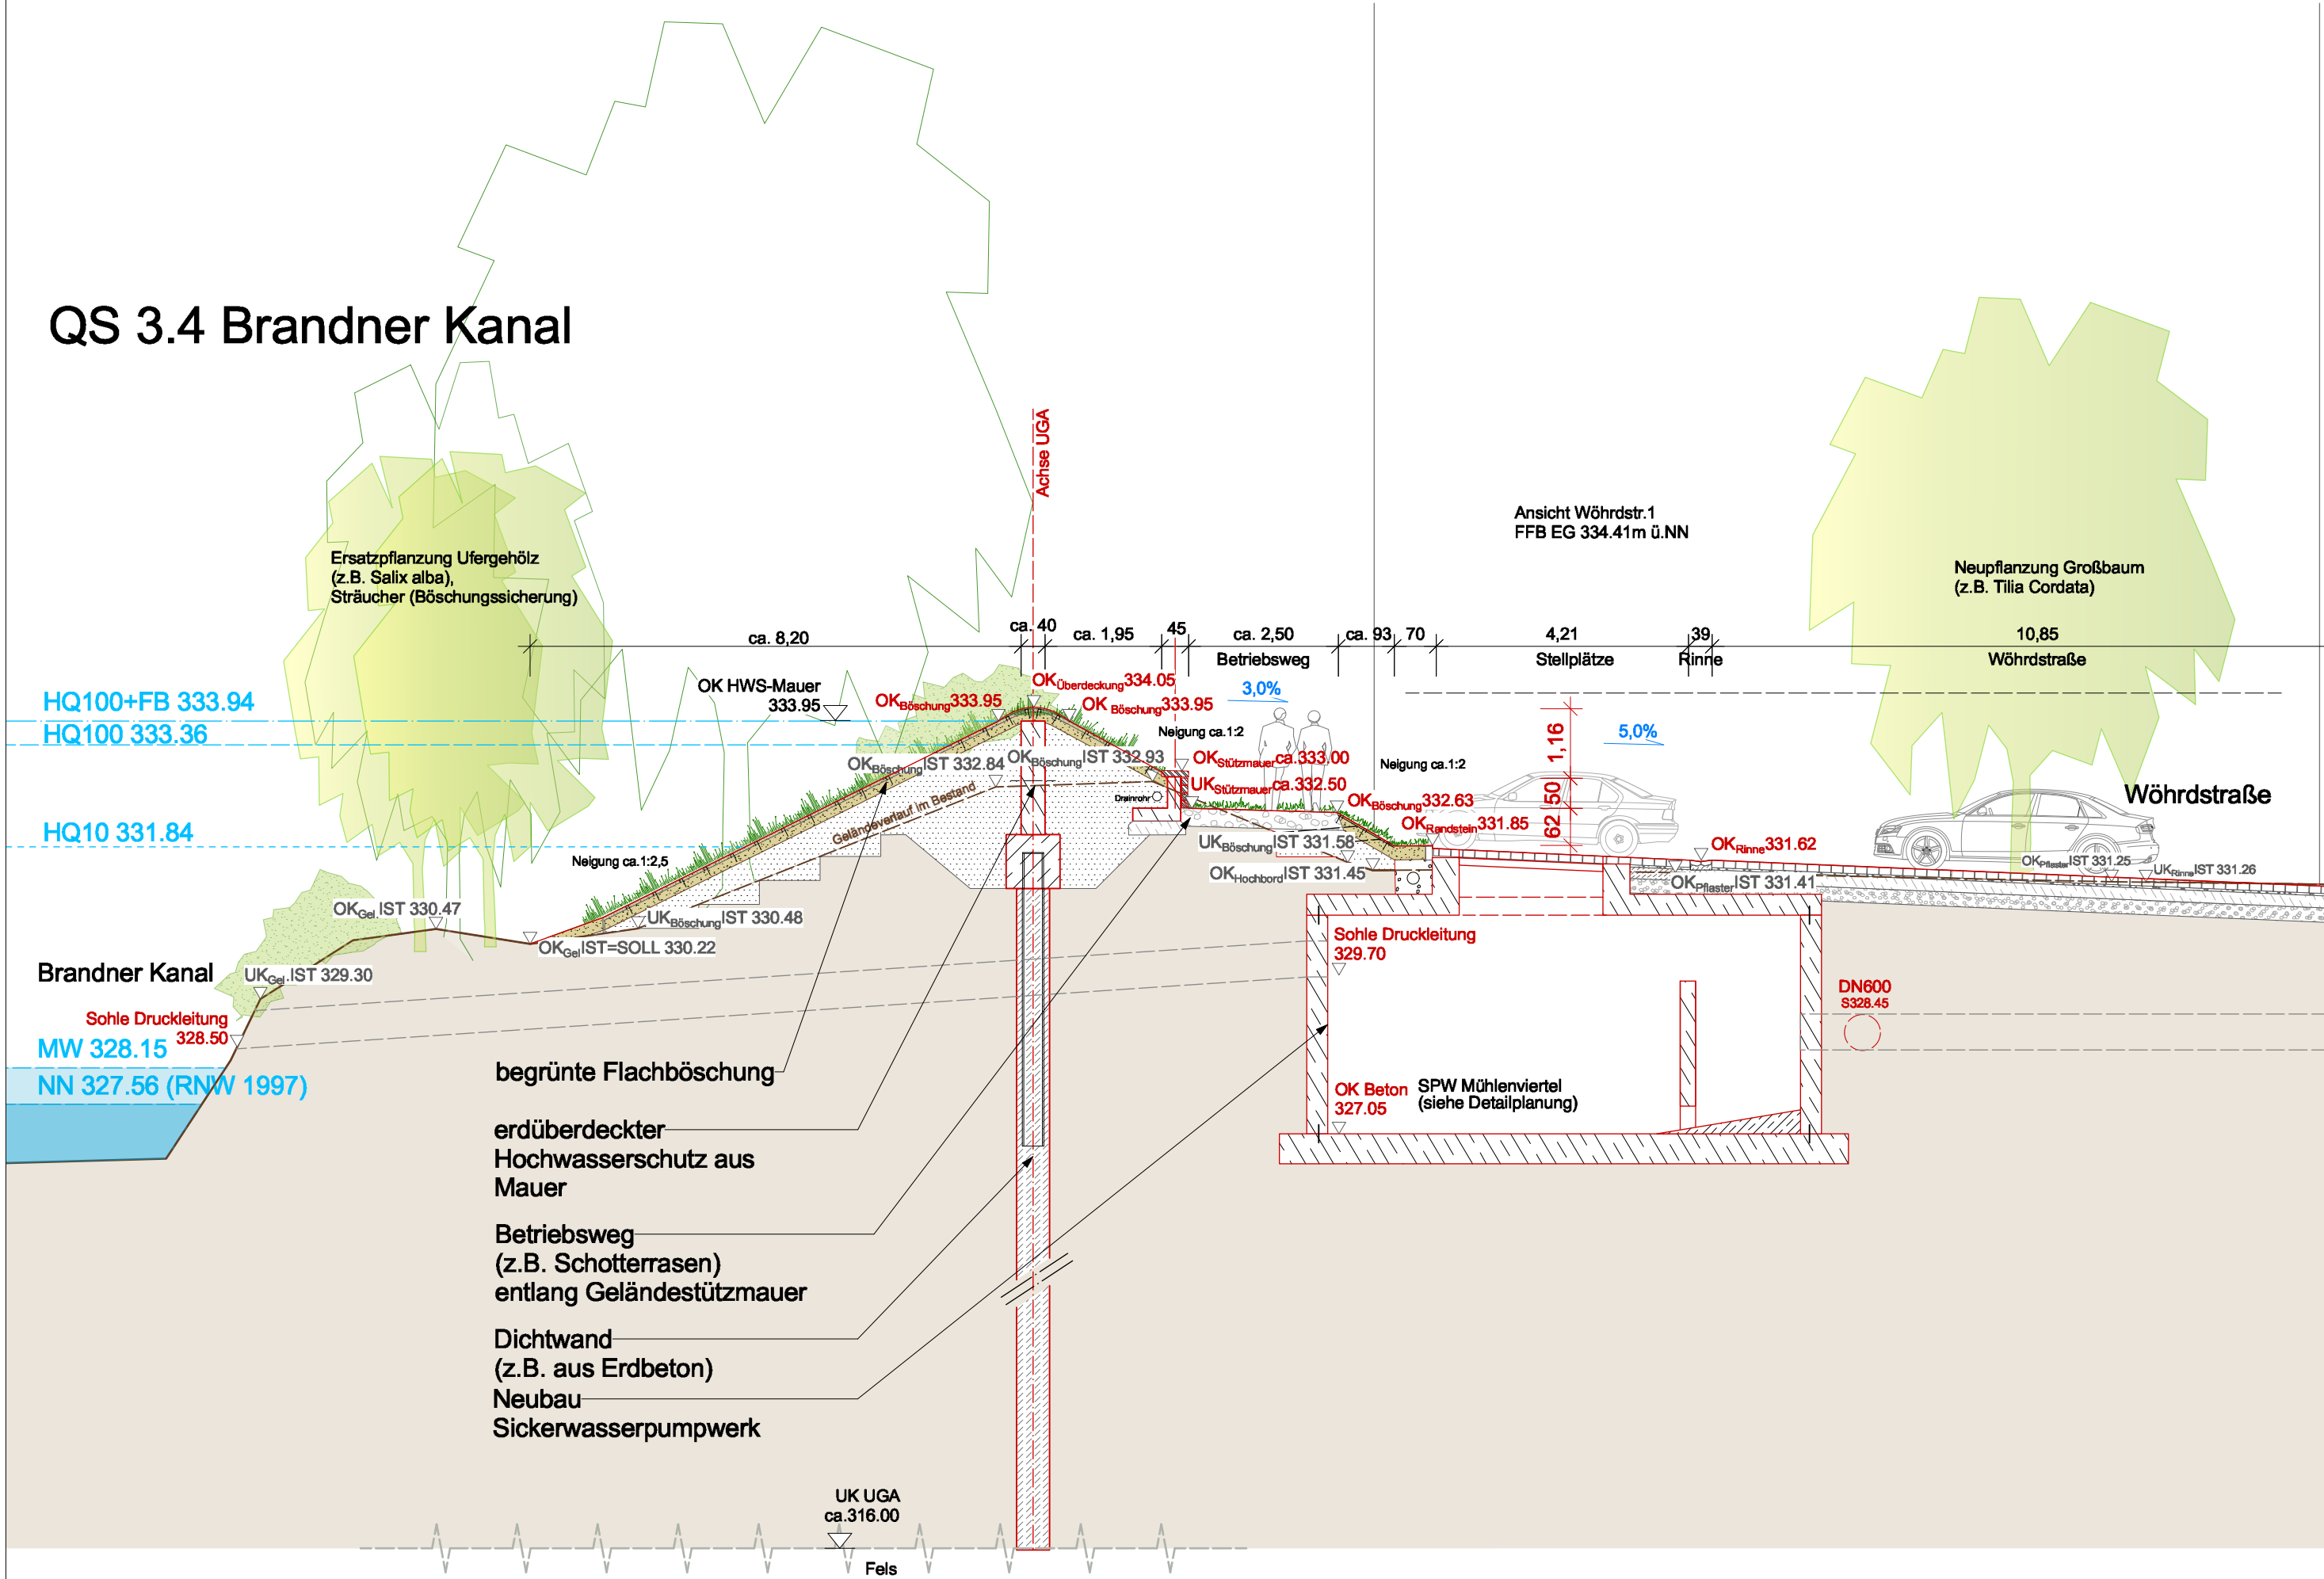


LEGENDE

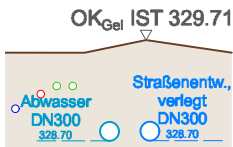


Bestandshöhe
Gelände Verlauf im Bestand
mit bestehendem Abwasserkanal/
geplantem Kanal für die Straßen-
entwässerung und bestehender
Versorgertrasse/ Gas/ Trinkwasser

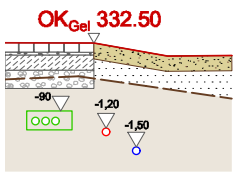

geplante Höhe
geplanter Gelände Verlauf
oberhalb Bestand (Aufschüttung)
mit beispielhaftem Bodenaufbau
und beispielhafter neuer
Versorgertrasse/ Gas/ Trinkwasser

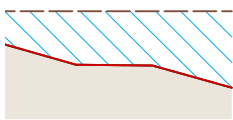


geplanter Gelände Verlauf
unterhalb Bestand (Abtrag)

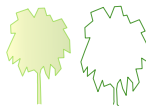


Neupflanzung/
Baumbestand




HWS-Maßnahme
(in der Schnittachse)

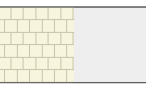

HWS-Mauer
(in der Ansicht)

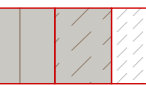

Untergrundabdichtung

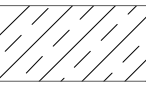

Gründung



Abbruchmaßnahmen/
Entfall Baumstandort

Vermerke Genehmigungsbehörde :



STADT
REGENSBURG

c					
b					
a					
Index	Bemerkung	geändert am	Name	geprüft am	Name



Vorhaben :		Hochwasserschutz Regensburg Abschnitt H Unterer Wöhrd PLANFESTSTELLUNG		Plan-Code : 36200-G-B 3.1.4				
Landkreis/ Stadt :		Regensburg		Anlage :	B 3.1.4	Phase :	G	
Vorhabensträger :		Freistaat Bayern, Wasserwirtschaftsamt Landshuter Straße 59, 9053 Regensburg		Plan-Nr. :		RB-H- QS 3.4-100		
Maßstab :		M 1:100		Vorhabenskennzeichen:		G11 3620001015		
		Planinhalt: Planabschnitt (PA)3 Querschnitt 3.4, Wöhrdstr. 1		Lagebezug:		GK4 (EPSG 31468)		
				Höhenbezug:		Regensburger Höhennetz aus 1927 in m ü.NN (≠ DHHN12/ 92/ 2016 des LDBV)		
Planung :		Arbeitsgemeinschaft TEAM 3		entw. :		3/2024	team 3	
						gez. :	4/2025	UB
INGENIEURGESELLSCHAFT mbH		architekten und landschaftsarchitekten		Landschaftsarchitekten		gepr. :	5/2025	WWA

30.04. 2025 Datum	Unterschrift Entwurfsverfasser	26.05. 2025 Datum	Unterschrift Vorhabensträger
----------------------	--------------------------------	----------------------	------------------------------