


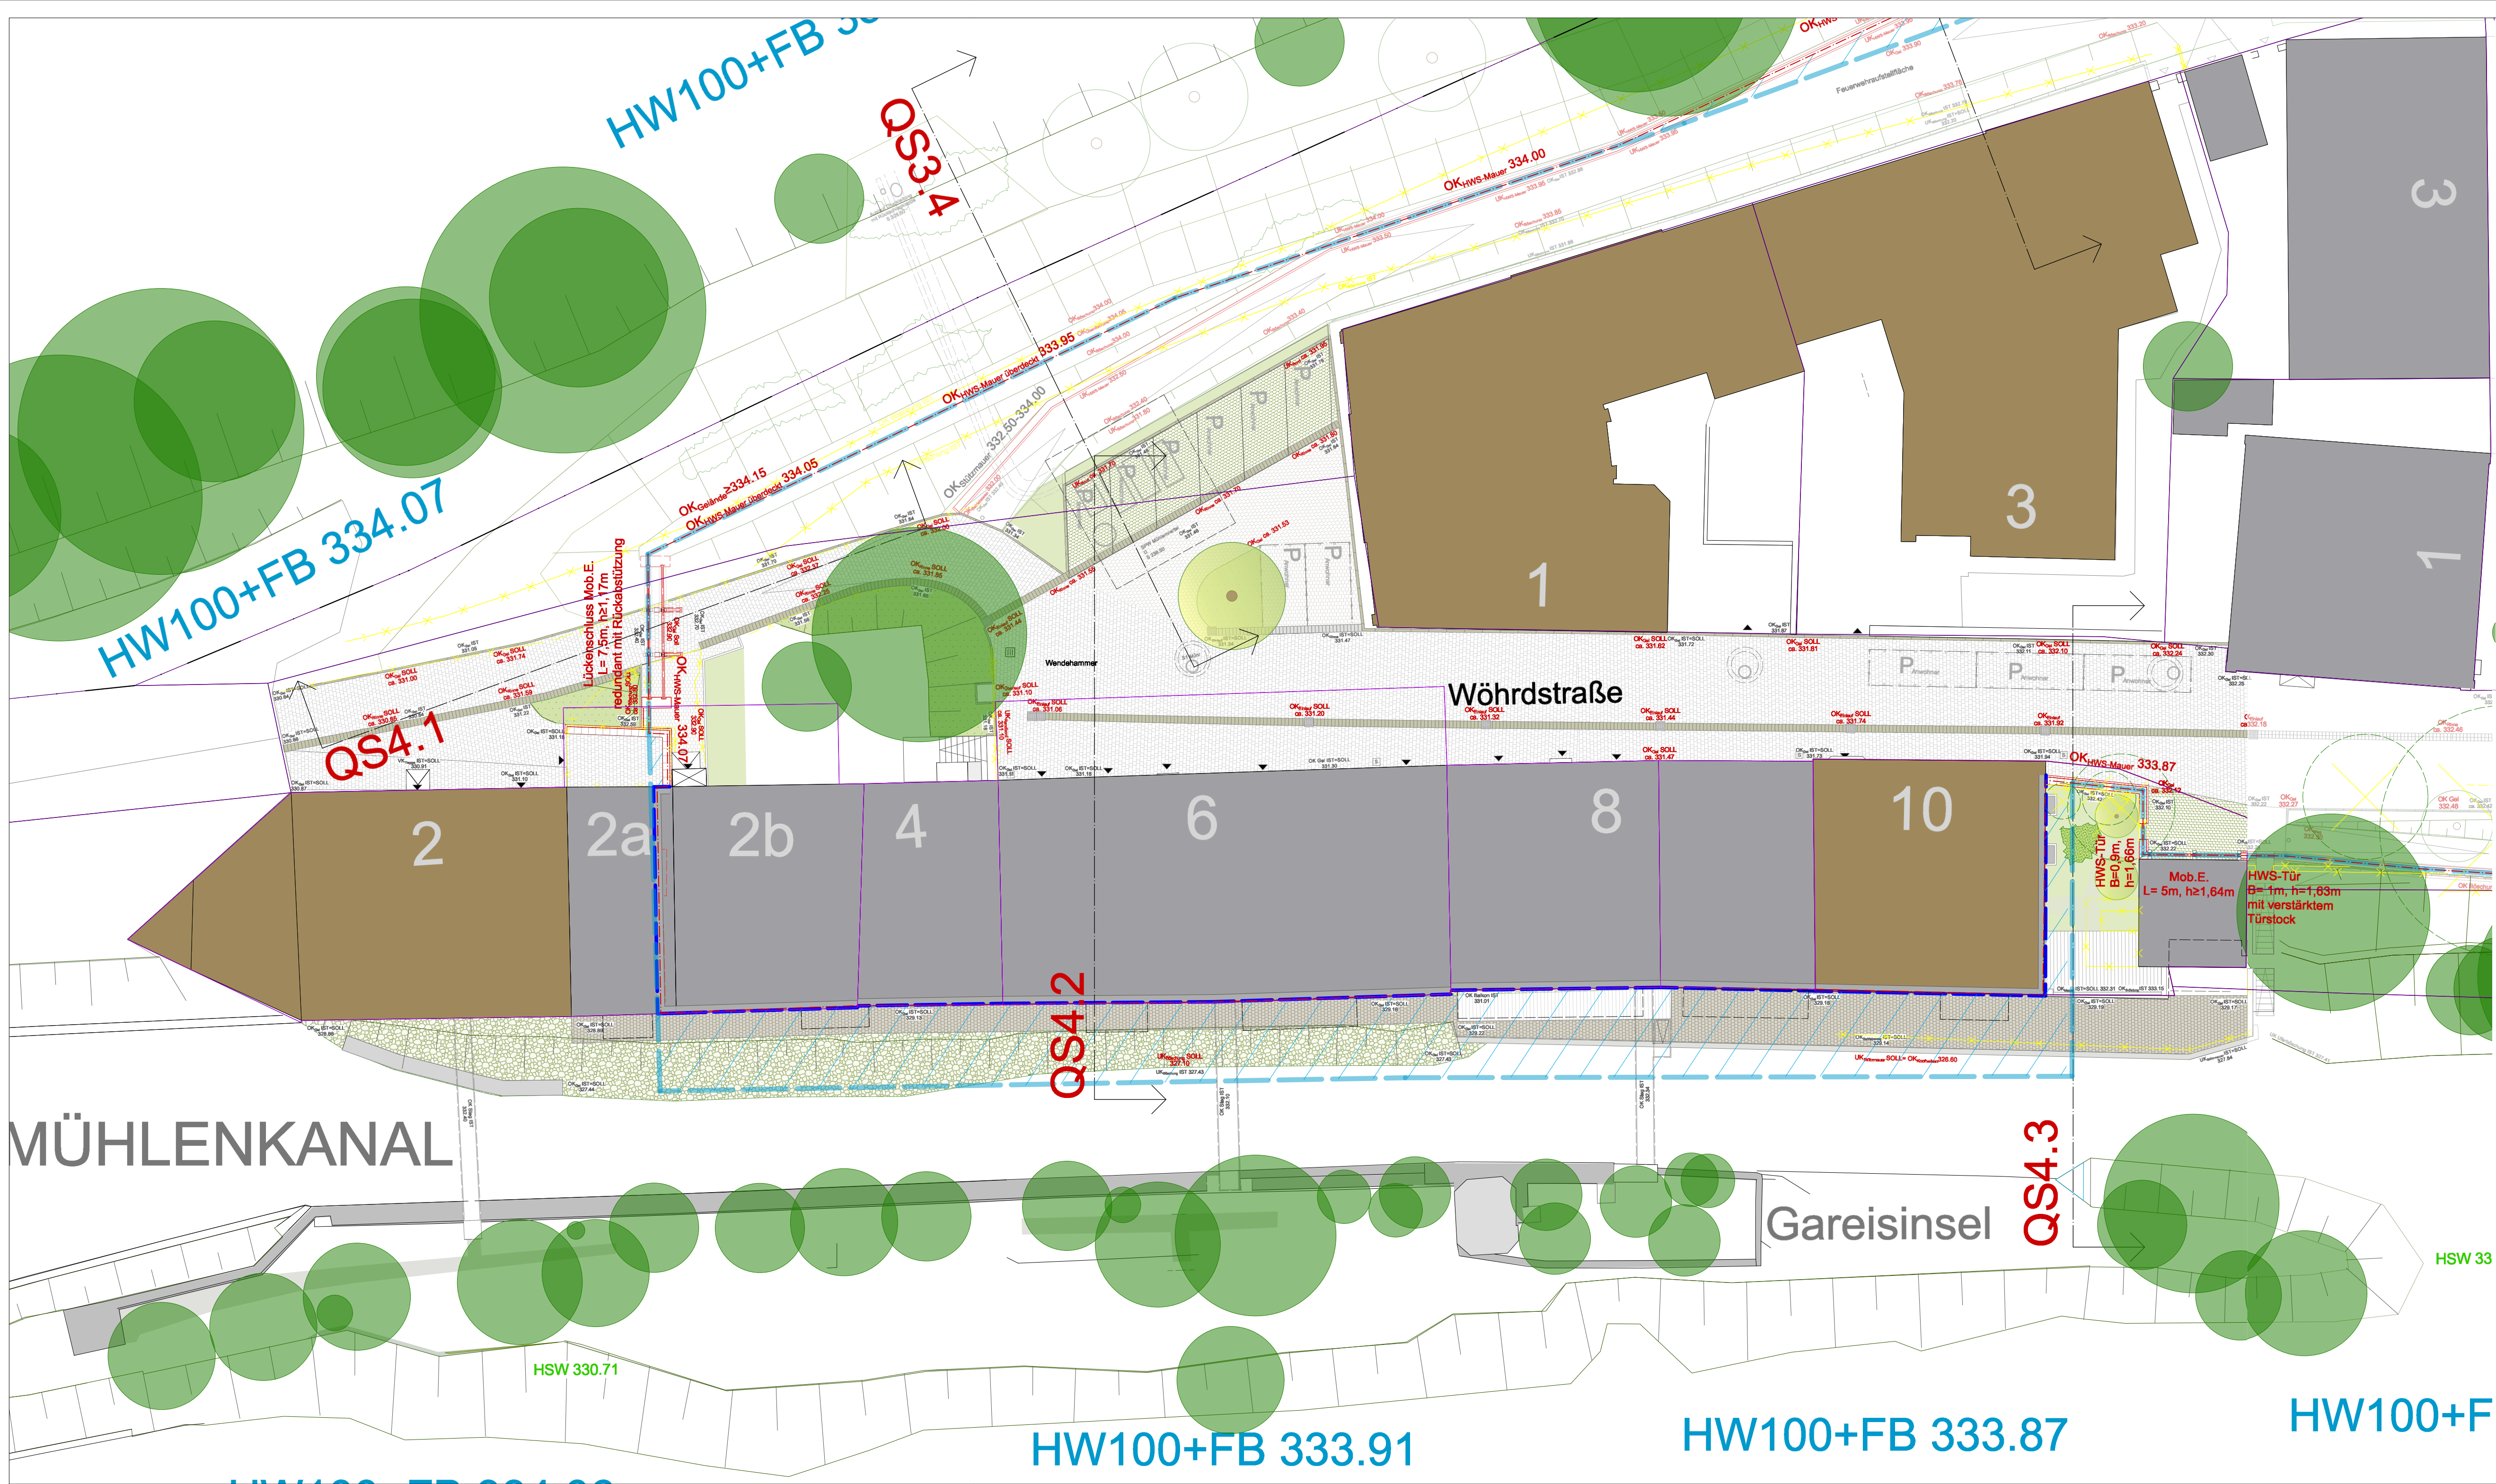

LEGENDE

Flurstücksgrenze

Gehölzbestand, Erhalt

Sträucher/Hecke im Bestand, Erhalt

333.60 Höhe im Bestand

Böschung im Bestand

Asphaltbelag im Bestand

Terrasse im Bestand (Erhalt/ Wiederherstellen)

ungebundener Belag (Schotter) im Bestand

Gebäude im Bestand

Tiefgarage im Bestand

Denkmal im Bestand

Extensive Wiese im Bestand (Erhalt/ Wiederherstellen)

Ufermauer, saniert

Mauer im Bestand

Gehölzstandort, Entfall

Neupflanzung Gehölz Standort verschleichen

Neupflanzung Sträucher/Hecke Standort verschleichen

333.60 geplante Höhe

Böschung, neu

neuer Pfasterbelag gebunden, geschnitten/ behauen

neuer Pfasterbelag, ungebunden mit Splitttrag/ Resenartige

neue Schotterdecke/ wassergebundene Decke

Rasengittersteine, neu

Schottermassen, neu (Bartbeweg)

Wiese mit hohem Böschung (Gräber/ Stauden), neu

wechsellückige Wiese, neu

extensiv gepflegte Wiese, neu

intensiv gepflegte Wiese, neu

Wasserbausteine/ Trockenmauer, neu

Achse mobiler HWS (Mobile Elemente) mobiler HWS (für einschaliges Mob.E.)

stationärer HWS (überdachte Mauer)

stationärer HWS mit aufgesetzten mobilen Elementen

Achse vertikale Untergrundabdichtung

horizontale Untergrundabdichtung

gebäudeübergreifender HW-Schutz

Integration bestehender mobiler Verschluss

PKW-Stellplatz neu

behindertengerecht

neue Treppenanlage

Bordstein, neu

Sitzbank, neu

Blocksteinpaved, neu

Poller, neu

Einfriedung, Zaunanlage

Stützmauer, neu

Handlauf/ Geländer, neu

offene Straßenentwässerungsrinne, neu

Rinne mit Abdeckung, neu

Straßeneinfuhr, neu

Schacht, neu

Vormerkung Genehmigungsbehörde:

c	b	a	Index	Bemerkung	geändert am	Name	geprüft am	Name
Übersichtsplan: 								

Vorhaben:

Hochwasserschutz Regensburg
Abschnitt H Unterer Wöhrd
PLANFESTSTELLUNG

Landkreis/ Stadt:

Regensburg

Vorhabenträger:

Freistaat Bayern, Wasserwirtschaftsamt
Landshuter Straße 59, 9053 Regensburg

Maßstab:

M 1:200

Planinhalt:

Planabschnitt (PA) 4
Lageplanausschnitt Mühlenviertel
Wöhrdstr. 1-4, 6, 8, 10

Planung:

Plan-Code:

36200-G-B 4.0

Anlage:

B 4.0

Phase:

G

Plan-Nr.:

RB-H-LP 4-200

Vorhabenskennzeichen:

G11 3620001015

Lagebezug:

GK4 (EPSG 31468)

Höhenbezug:

Regensburger Höhenreferenz aus
1927 in m ü. NN (f. DRS-N/2/92/
2016 des LDBV)

entw.:

3/2024

team:

3

gepr.:

4/2025

UB:

gepr.:

5/2025

WWA:

30.04.2025

30.04.2025

Datum

Unterschrift Entwurfsverfasser

Datum

Unterschrift Vorhabenträger