

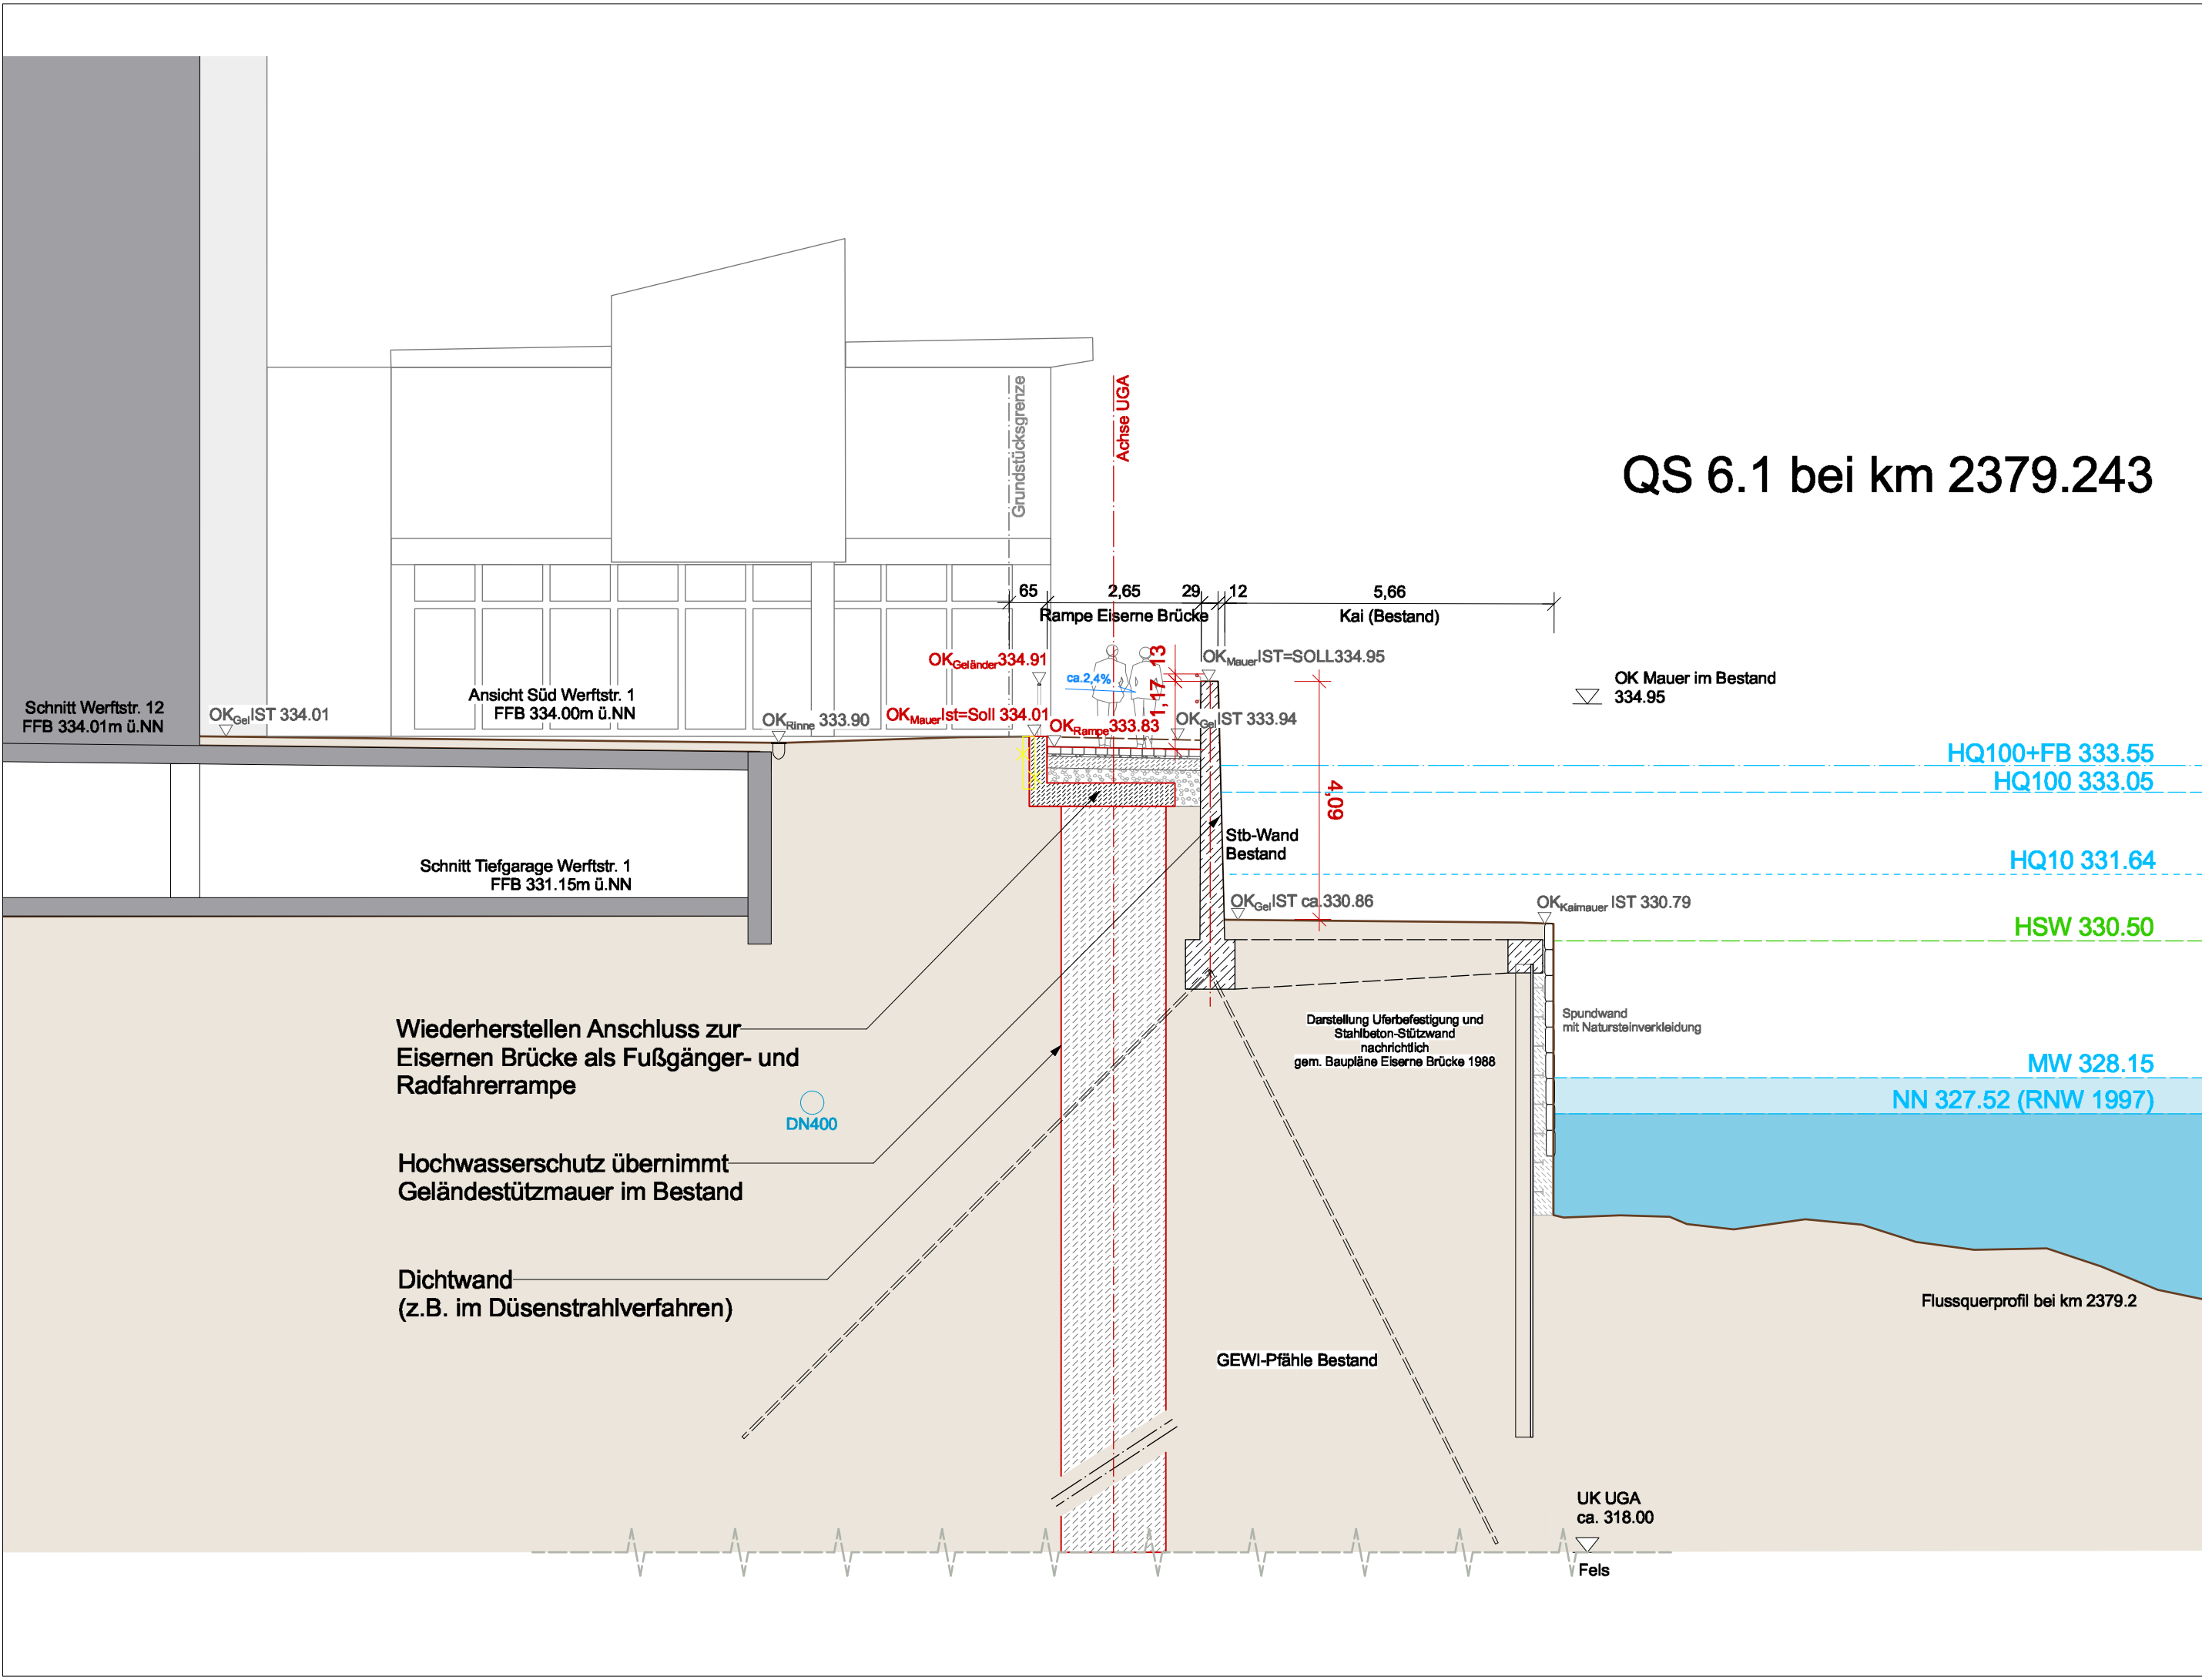
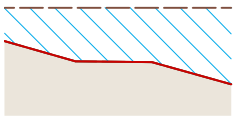


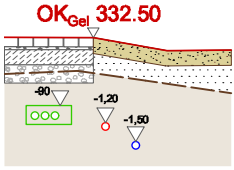

QS 6.1 bei km 2379.243

LEGENDE

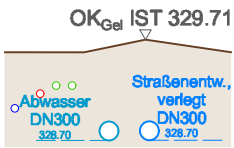

Bestandshöhe
Geländeverlauf im Bestand
mit bestehendem Abwasserkanal/
geplantem Kanal für die Straßen-
entwässerung und bestehender
Versorgertrasse/ Gas/ Trinkwasser

geplante Höhe
geplanter Geländeverlauf
oberhalb Bestand (Aufschüttung)
mit beispielhaftem Bodenaufbau
und beispielhafter neuer
Versorgertrasse/ Gas/ Trinkwasser

geplanter Geländeverlauf
unterhalb Bestand (Abtrag)



**Neupflanzung/
Baumbestand**

**HWS-Maßnahme
(in Schnittachse)**

**HWS-Mauer
(in der Ansicht)**

Untergrundabdichtung

Gründung

**Abbruchmaßnahmen/
Entfall Baumstandort**


Vermerke Genehmigungsbehörde :

c					
b					
a					
Index	Bemerkung	geändert am	Name	geprüft am	Name

Übersichtslageplan

Vorhaben :	Hochwasserschutz Regensburg Abschnitt H Unterer Wöhrd PLANFESTSTELLUNG	Plan-Code :	36200-G-B 6.1.1	
Landkreis/ Stadt :	Regensburg	Anlage :	B 6.1.1	Phase : G
Vorhabensträger :	Freistaat Bayern, Wasserwirtschaftsamt Landshuter Straße 59, 9053 Regensburg	Plan-Nr. :	RB-H- QS 6.1-100	
Maßstab :	M 1:100	Vorhabenskennzeichen:	G1t 3620001015	
Planung :	Arbeitsgemeinschaft TEAM 3 	Lagebezug:	GK4 (EPSG 31468)	
		Höhenbezug:	Regensburger Höhennetz aus 1927 in m ü.NN (≠ DHHN12/ 92/ 2016 des LDBV)	
		entw. :	3/2024	team 3
		gez. :	4/2025	UB
		gepr. :	5/2025	WWA

30.04. 2025 Datum	 Unterschrift Entwurfsverfasser	26.05. 2025 Datum	 Unterschrift Vorhabensträger
----------------------	------------------------------------	----------------------	----------------------------------

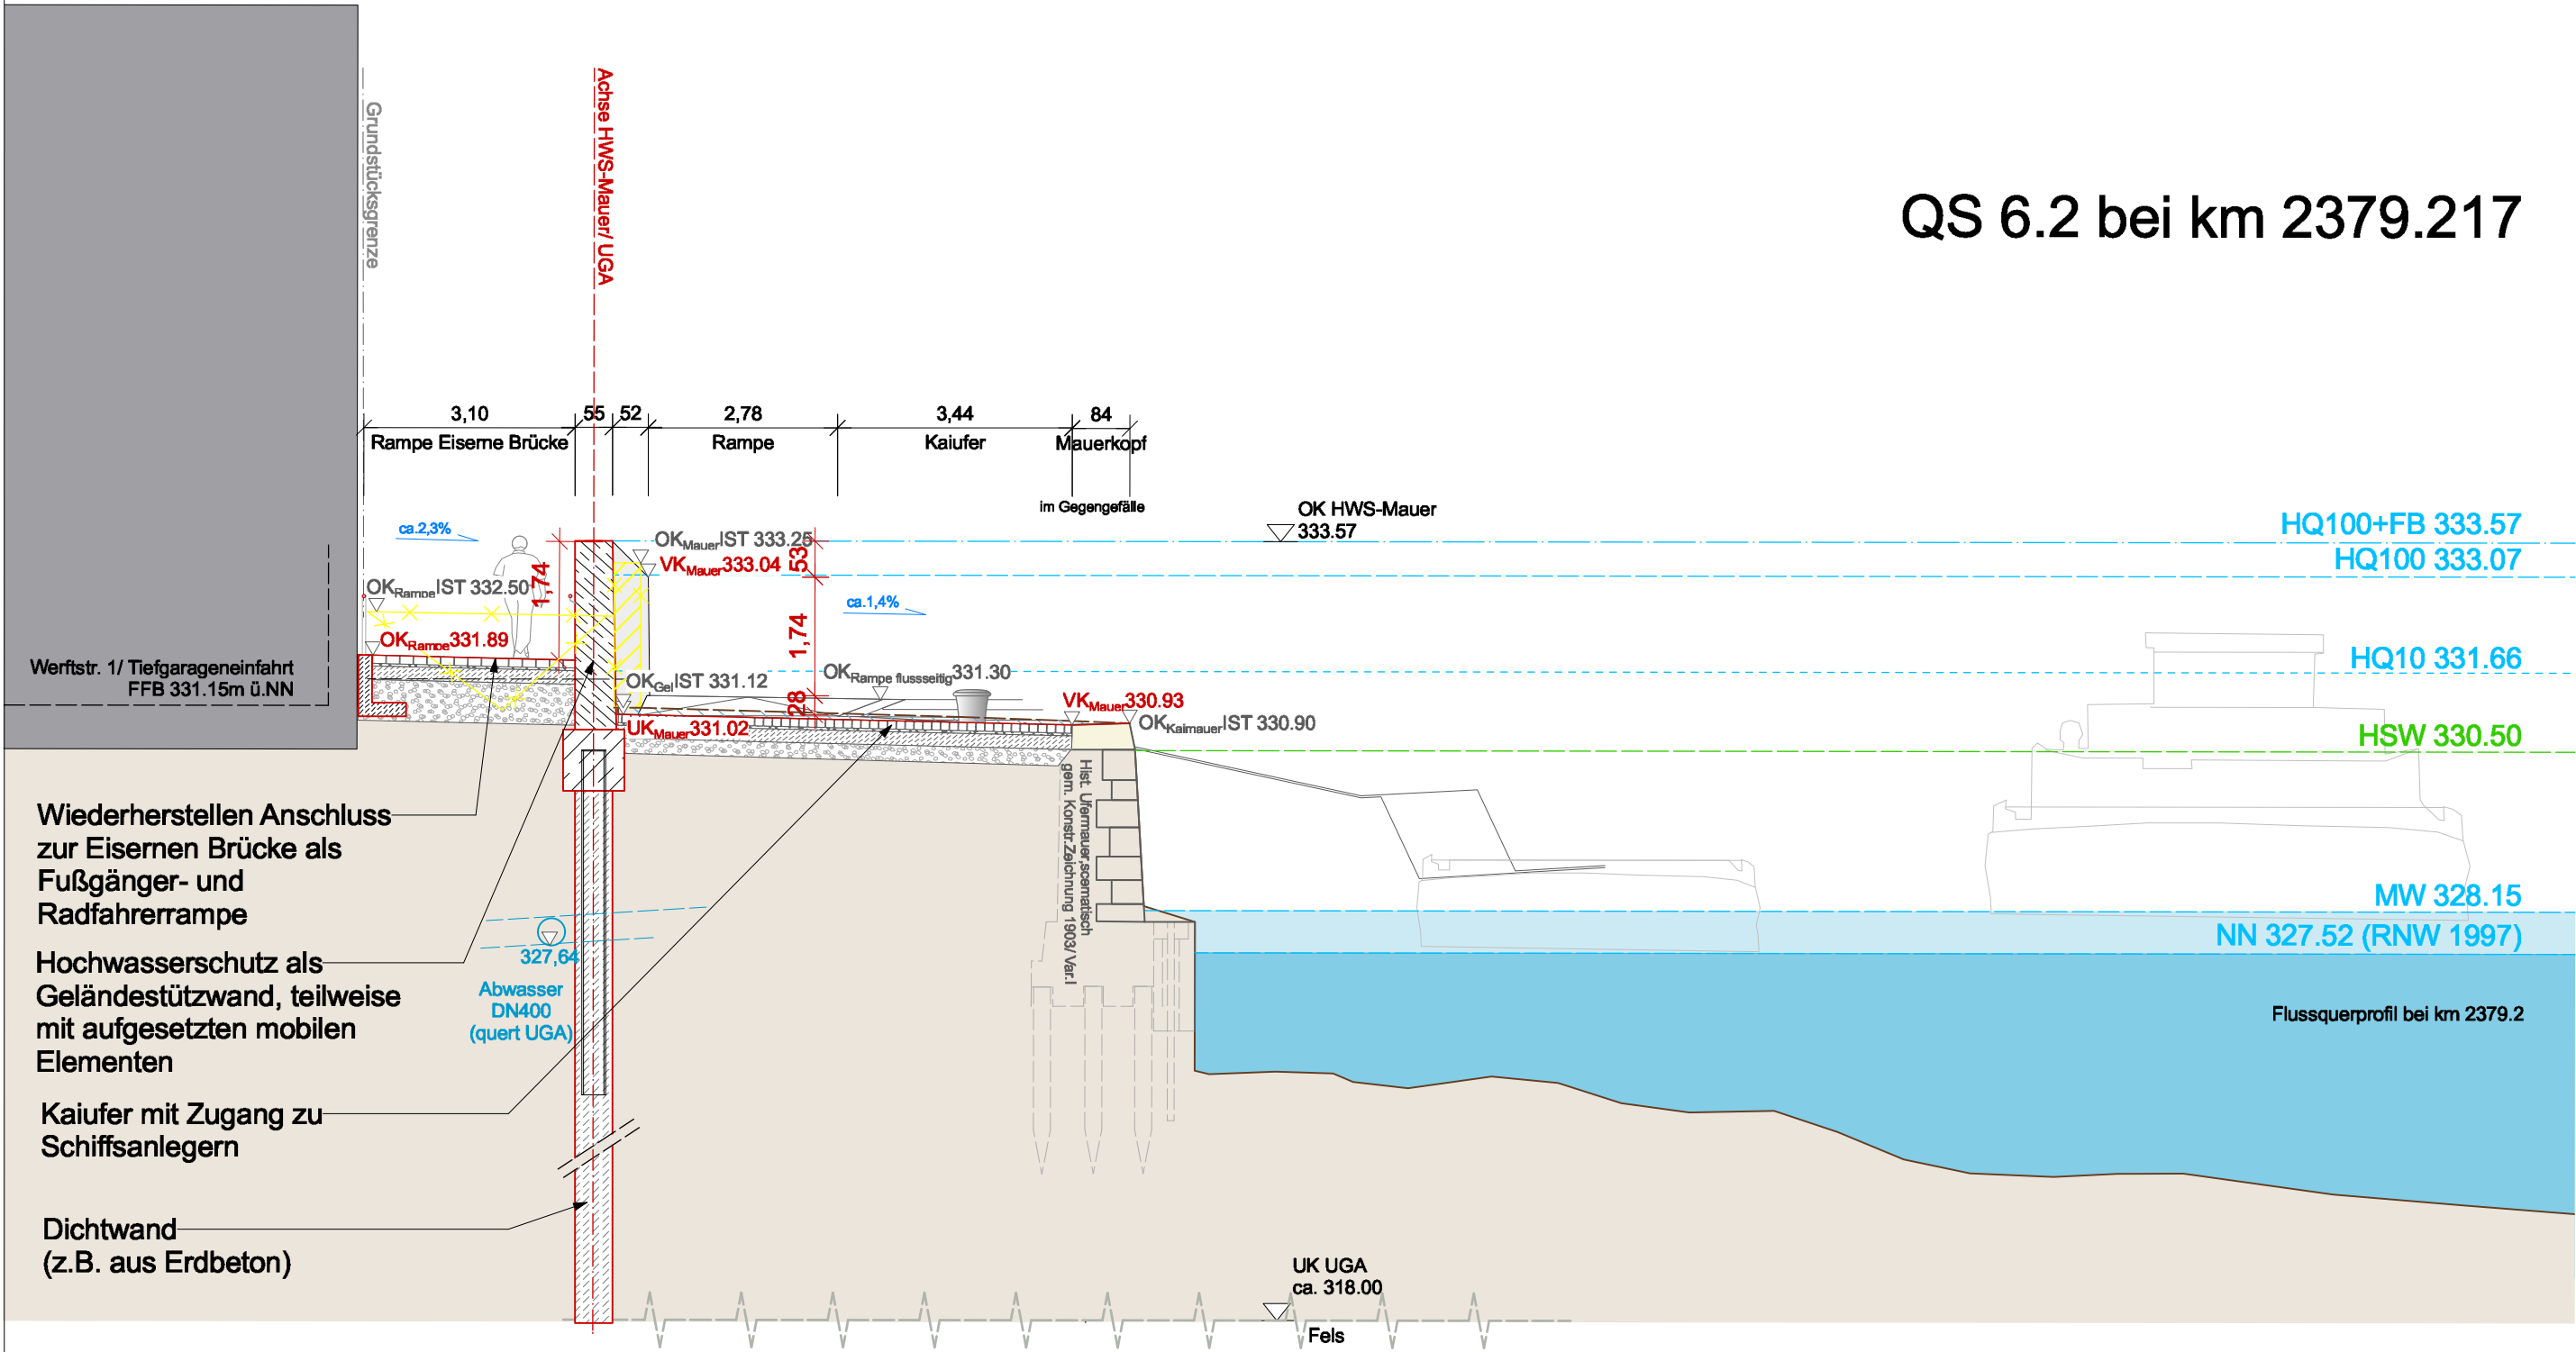

QS 6.2 bei km 2379.217

LEGENDE

OK_{Gel} IST 329.71

OK_{Gel} 332.50

Bestandshöhe
Geländeverlauf im Bestand
mit bestehendem Abwasserkanal/
geplantem Kanal für die Straßen-
entwässerung und bestehender
Versorgertrasse/ Gas/ Trinkwasser

geplante Höhe
geplanter Geländeverlauf
oberhalb Bestand (Aufschüttung)
mit beispielhaftem Bodenaufbau
und beispielhafter neuer
Versorgertrasse/ Gas/ Trinkwasser

geplanter Geländeverlauf
unterhalb Bestand (Abtrag)

Neupflanzung/
Baumbestand

HWS-Maßnahme
(in Schnittachse)

HWS-Mauer
(in der Ansicht)

Untergrundabdichtung

Gründung

Abbruchmaßnahmen/
Entfall Baumstandort

Vermerke Genehmigungsbehörde :

STADT
REGENSBURG

c					
b					
a					
Index	Bemerkung	geändert am	Name	geprüft am	Name

Übersichtslageplan

Vorhaben :

**Hochwasserschutz Regensburg
Abschnitt H Unterer Wöhrd
PLANFESTSTELLUNG**

Landkreis/ Stadt :

Regensburg

Vorhabenträger :

Freistaat Bayern, Wasserwirtschaftsamt
Landshuter Straße 59, 9053 Regensburg

Maßstab :

M 1:100

Planinhalt :

**Planabschnitt (PA)6
Querschnitt 6.2, Werftstr. 1**

Planung :

Plan-Code :

36200-GB 6.1.2

Anlage :

B 6.1.2

Phase :

G

Plan-Nr. :

RB-H-QS 6.2-100

Vorhabenskennzeichen:

G11 3620001015

Lagebezug:

GK4 (EPSG 31468)

Höhenbezug:

Regensburger Höhennetz aus
1927 in m ü.NN (≠ DHHN12/ 92/
2016 des LDBV)

entw. :

3/2024

gez. :

4/2025

gepr. :

5/2025

team 3

UB

WWA

30.04. 2025

Datum

Unterschrift Entwurfsverfasser

26.05. 2025

Datum

Unterschrift Vorhabenträger

QS 6.3 bei km 2379.181

Schnitt Werftstr. 4 FFB 331.90m ü.NN

Ansicht Werftstr. 5 FFB 331.90m ü.NN

Grundstücksgrenze

3,27

Neupflanzung (Zierkirsche) mit Wurzelführung/-sperre

5,61

Mischverkehrsfläche

Werftstraße

15

55

86

99

1,21

1,98

2,17

84

3 Stg. 15/33

6 Stg. 15/33

Kai

Mauerkopf im Gegengefälle

OK Mob.E. 333.62

HQ100+FB 333.62

HQ100 333.12

OK Zaun IST 333.14

OK Sockel IST 332.10

UK Sockel IST 331.45

ca. 3,7%

ca. 2,7%

OK Rinne 331.17

OK Straße IST 331.19

2,12

UK Mob.E. 331.50

UK Bord 331.38

ca. 1,5%

ca. 2,4%

OK Stufe 331.45

UK Stufe 331.00

OK Stufe 331.00

ca. 1,4%

Abbruch/Verlegung Verteilerkasten

UK Mob.E. 331.50

HQ10 331.67

OK Gel IST 330.86

OK Gel IST 330.88

OK Dalbe 330.96

HSW 330.47

UK Stufe 330.10

ca. -0,03

OK Kalmauer IST 330.12

MW 328.15

NN 327.52 (RNW 1997)

Vorschlag Neuordnung Versorger

Umplanung Gas, Trinkwasser

Straßenentw. geplant DN300

Drainage DN300

Abwasser DN400

Wiederherstellen Werftstraße als Mischverkehrsfläche mit flankierender Baumreihe

Hochwasserschutz als mobile Elemente

Platzbereich mit Stufenanlage

Kaiufer mit Zugang zu Schiffsanlegern

Dichtwand (z.B. aus Erdbeton)

Flussquerprofil bei km 2379.2

UK UGA ca. 317.00

Fels

OK_{Gel} | IST 329.71

Abwasser DN300 328.70

Straßenentw., verlegt DN300 328.70

L_{Einbau}

A cross-section diagram of a road structure. The top layer is a red line labeled 'OK_{Gel} 332.50'. Below it is a hatched layer, then a layer with circles, and a bottom layer. A green box contains two circles with a label '-90' above them. To the right, a red circle has a label '-1,20' above it, and a blue circle has a label '-1,50' above it. The diagram shows a transition from a solid surface to a sloped embankment.

	Neupflanzung/ Baumbestand
	HWS-Maßnahme (in Schnittachse)
	HWS-Mauer (in der Ansicht)
	Untergrundabdichtung
	Gründung
	Abbruchmaßnahmen/ Entfall Baumstandort

Wasserwirtschaftsamt
Regensburg

**STADT
REGENSBURG**

c					
b					
a					
Index	Bemerkung	geändert am	Name	geprüft am	Name

Obersichtslageplan



Plan-Code : 36200-G-B 6.1.3

Anlage : B 6.1.3	Phase : G
-------------------------	------------------

Plan-Nr. : **RB-H-QS 6.3-100**

Maßstab :
M 1:100

Lagebezug: GK4 (EPSG 31468)
Höhenbezug: Regensburger Höhennetz aus 1927 in m ü.NN (≠ DHHN12/92/2016 des LDBV)

Planung : **Arbeitsgemeinschaft TEAM 3**

schömigplan
INGENIEURGESELLSCHAFT mbH


ARCHISCAP
architekten und landschaftsarchitekten

entw. :	3/2024	team 3
gez. :	4/2025	UB
gepr. :	5/2025	WWA

30.04.2025
Datum



Unterschrift Entwurfsverfasser

26.05.2025
Datum Unterschrift Vorhabensträger

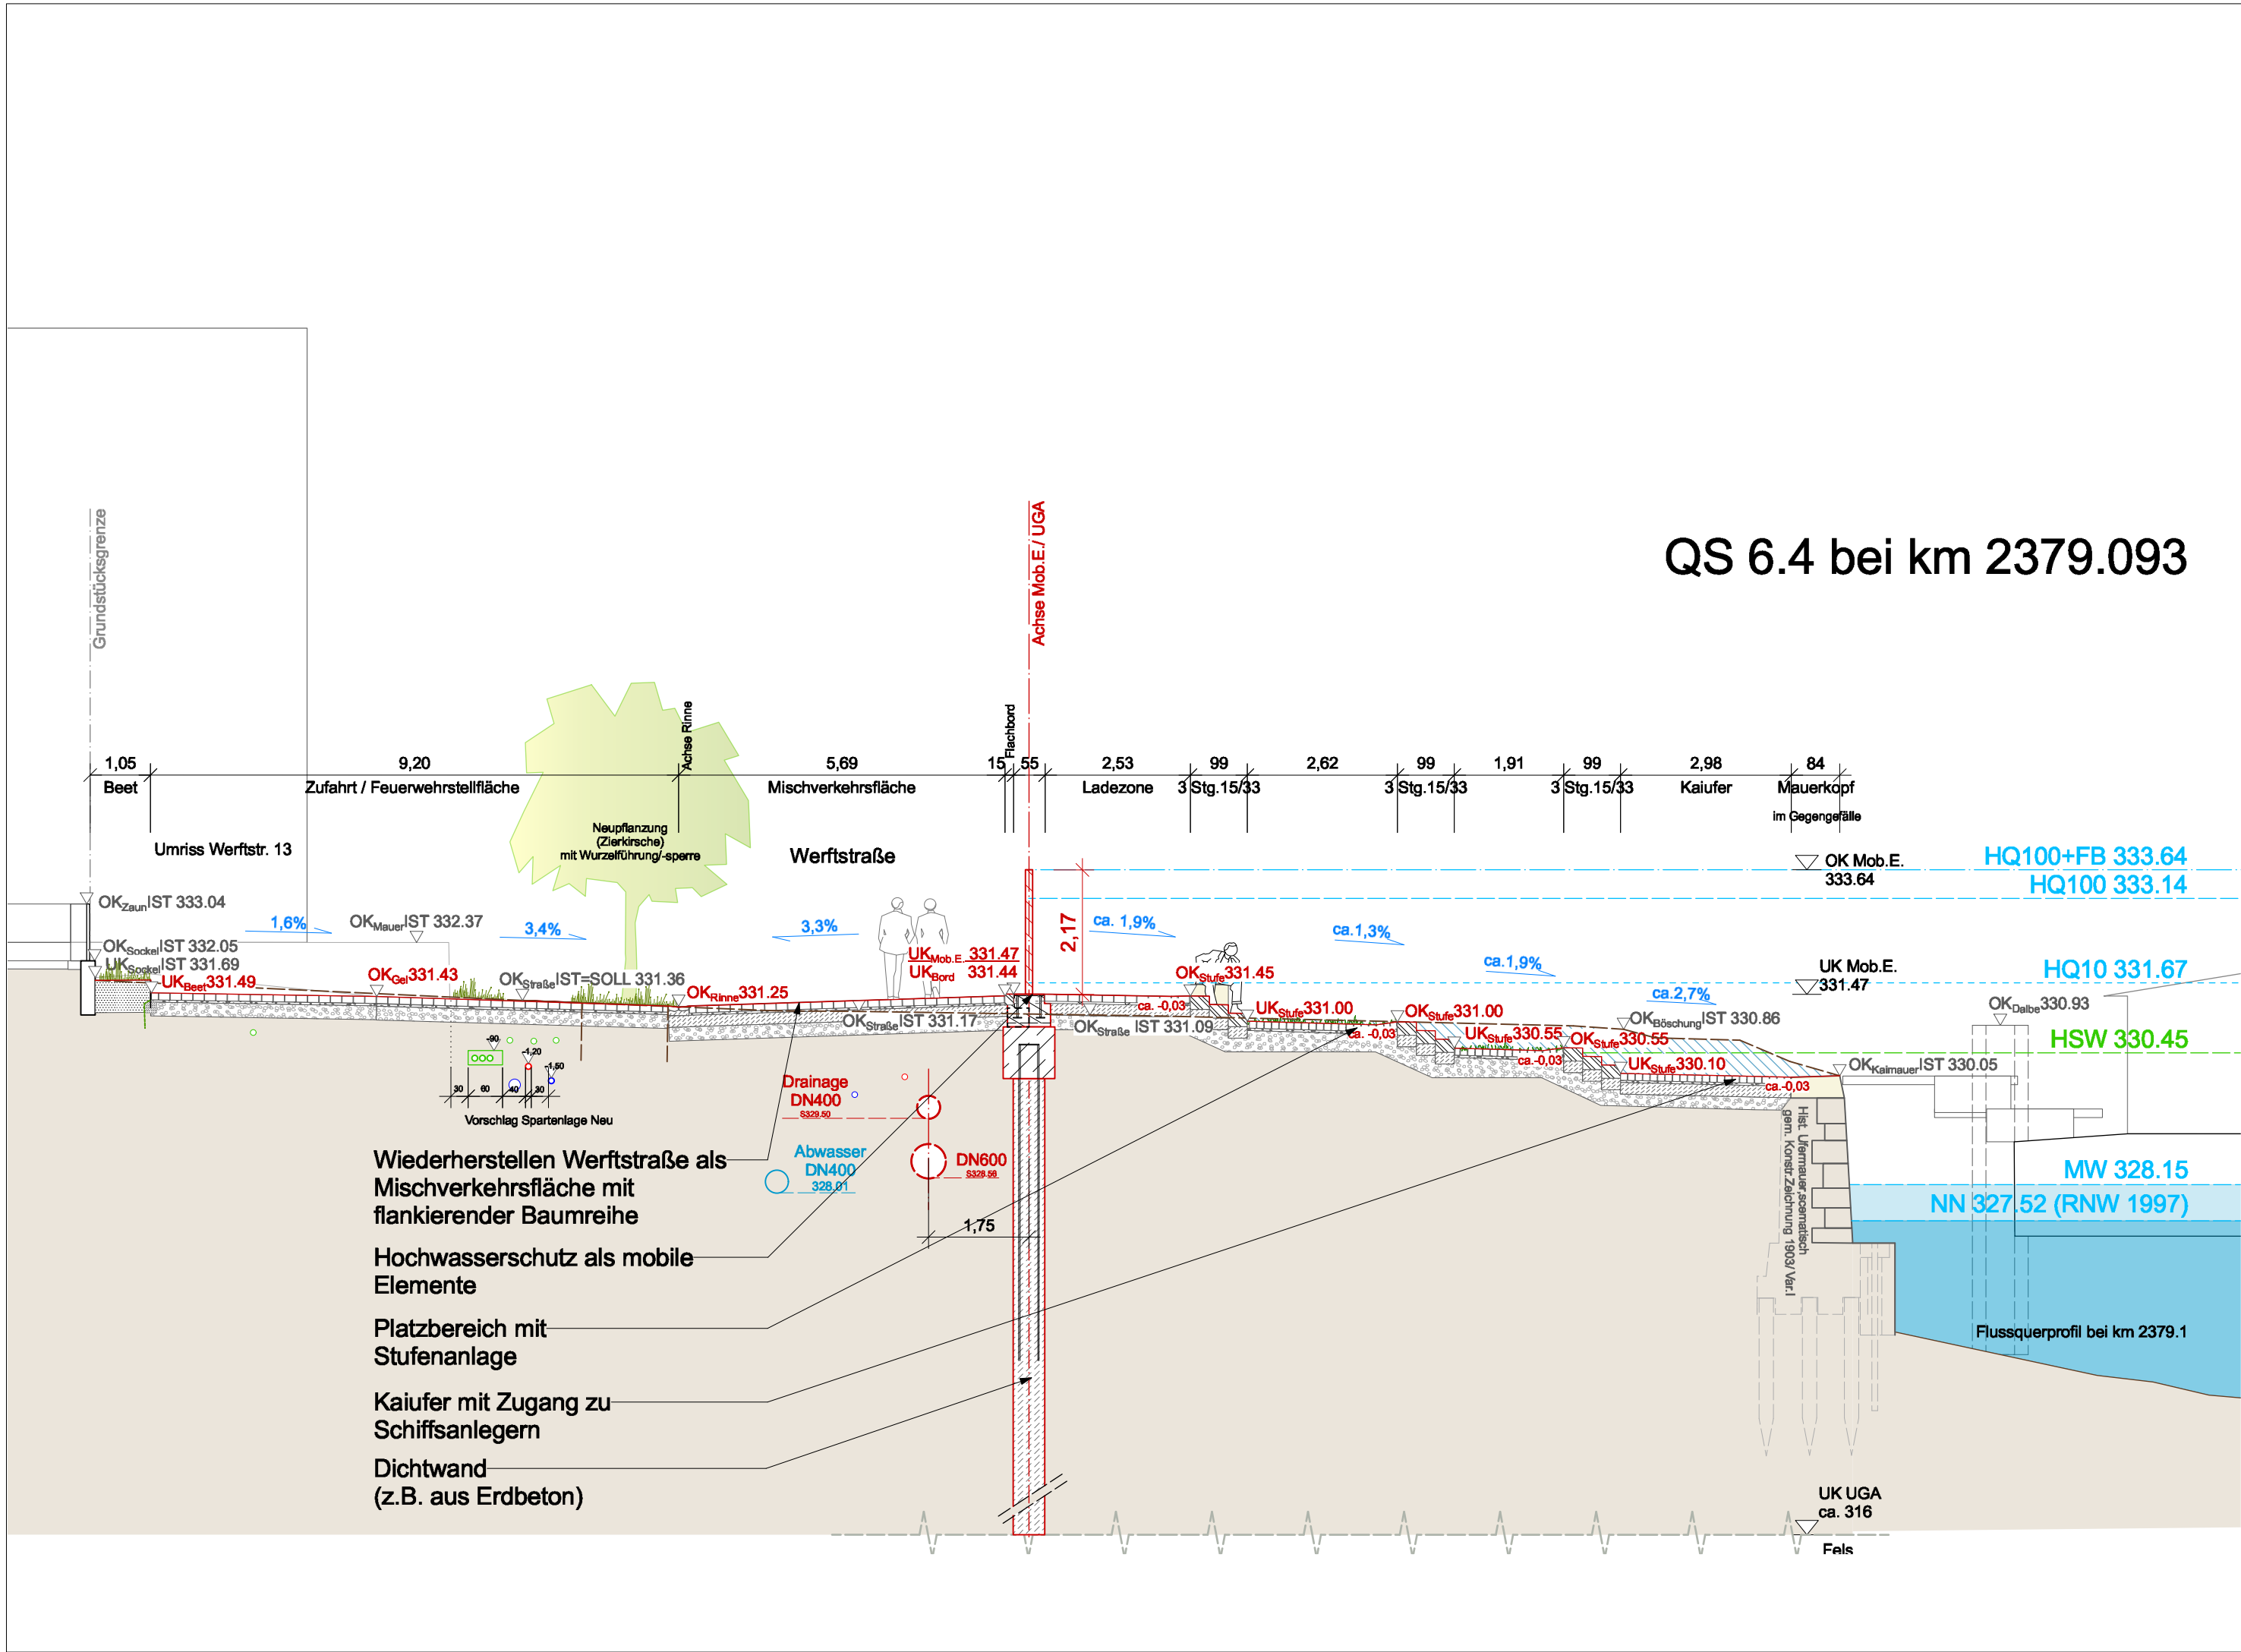


QS 6.4 bei km 2379.093


LEGENDE

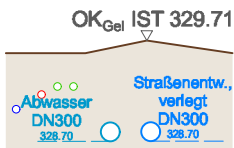


Bestandshöhe
Geländeverlauf im Bestand
mit bestehendem Abwasserkanal/
geplantem Kanal für die Straßen-
entwässerung und bestehender
Versorgertrasse/ Gas/ Trinkwasser

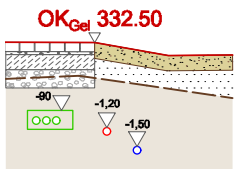

geplante Höhe
geplanter Geländeverlauf
oberhalb Bestand (Aufschüttung)
mit beispielhaftem Bodenaufbau
und beispielhafter neuer
Versorgertrasse/ Gas/ Trinkwasser

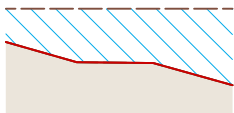

geplanter Geländeverlauf
unterhalb Bestand (Abtrag)

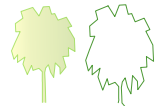

Neupflanzung/
Baumbestand



HWS-Maßnahme
(in Schnittachse)



HWS-Mauer
(in der Ansicht)



Untergrundabdichtung



Gründung



Abbruchmaßnahmen/
Entfall Baumstandort

Vermerke Genehmigungsbehörde :




STADT
REGENSBURG

c					
b					
a					
Index	Bemerkung	geändert am	Name	geprüft am	Name



Vorhaben :	Hochwasserschutz Regensburg Abschnitt H Unterer Wöhrd PLANFESTSTELLUNG	Plan-Code : 36200-G-B 6.1.4	
		Anlage : B 6.1.4	Phase : G
Landkreis/ Stadt :	Regensburg	Plan-Nr. : RB-H- QS 6.4-100	
Vorhabensträger :	Freistaat Bayern, Wasserwirtschaftsamt Landshuter Straße 59, 9053 Regensburg	Vorhabenskennzeichen: G11 3620001015	
Maßstab :	Planinhalt : Planabschnitt (PA)6 Querschnitt 6.4, Werftstr. 10	Lagebezug: GK4 (EPSG 31468)	
		Höhenbezug: Regensburger Höhennetz aus 1927 in m ü.NN(≠ DHHN12/ 92/ 2016 des LDBV)	
Planung :	Arbeitsgemeinschaft TEAM 3	entw. : 3/2024	team 3
		gez. : 4/2025	UB
		gepr. : 5/2025	WWA

30.04. 2025 Datum	 Unterschrift Entwurfsverfasser	26.05. 2025 Datum	 Unterschrift Vorhabensträger
----------------------	------------------------------------	----------------------	----------------------------------

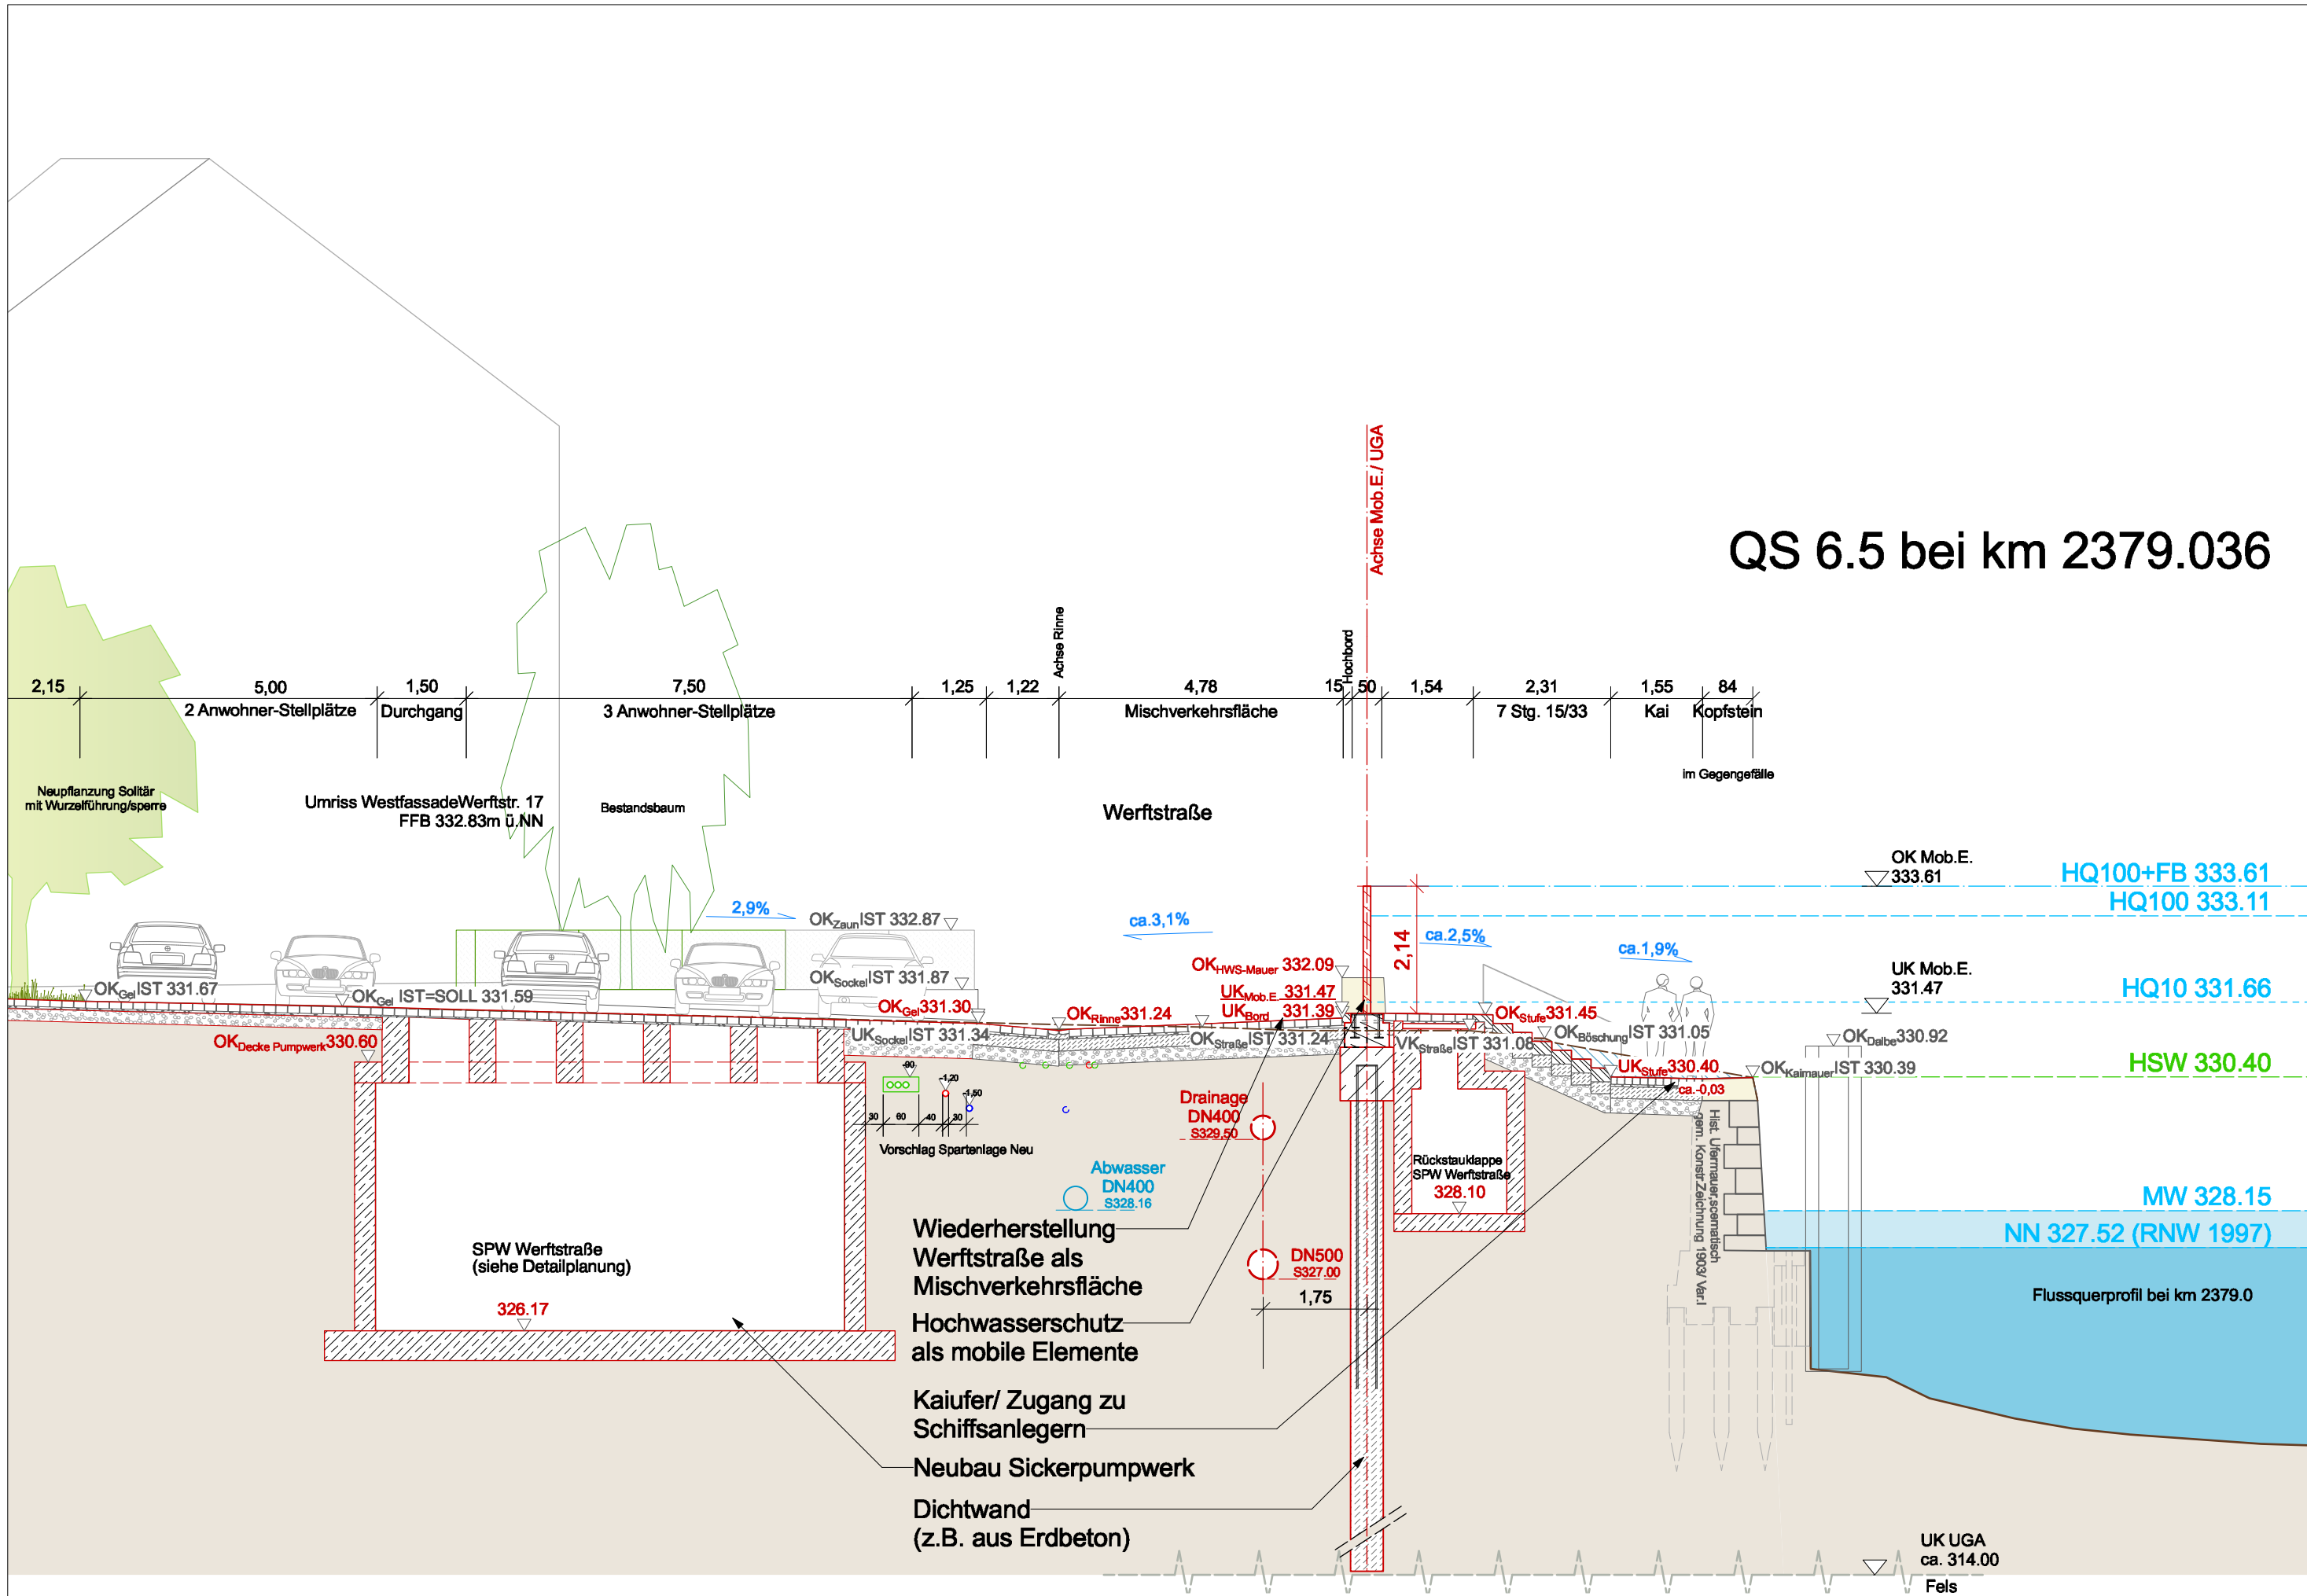

QS 6.5 bei km 2379.036

LEGENDE

OK_{Gel} IST 329.71

Bestandshöhe
Geländeverlauf im Bestand
mit bestehendem Abwasserkanal/
geplantem Kanal für die Straßen-
entwässerung und bestehender
Versorgertrasse/ Gas/ Trinkwasser

OK_{Gel} 332.50

geplante Höhe
geplanter Geländeverlauf
oberhalb Bestand (Aufschüttung)
mit beispielhaftem Bodenaufbau
und beispielhafter neuer
Versorgertrasse/ Gas/ Trinkwasser

geplanter Geländeverlauf
unterhalb Bestand (Abtrag)

Neupflanzung/
Baumbestand

HWS-Maßnahme
(in Schnittachse)

HWS-Mauer
(in der Ansicht)

Untergrundabdichtung

Gründung

Abbruchmaßnahmen/
Entfall Baumstandort

Vermerke Genehmigungsbehörde :

c					
b					
a					
Index	Bemerkung	geändert am	Name	geprüft am	Name

Übersichtslageplan :

Vorhaben :

Hochwasserschutz Regensburg
Abschnitt H Unterer Wöhrd
PLANFESTSTELLUNG

Landkreis/ Stadt : Regensburg

Vorhabensträger : Freistaat Bayern, Wasserwirtschaftsamt
Landshuter Straße 59, 9053 Regensburg

Plan-Code : 36200-G-B 6.1.5

Anlage : B 6.1.5	Phase : G
------------------	-----------

Plan-Nr. : RB-H- QS 6.5-100

Vorhabenskennzeichen:
G1t 3620001015

Maßstab : M 1:100

Planinhalt : Planabschnitt (PA)6
Querschnitt 6.5, Werftstr. 16

Lagebezug: GK4 (EPSG 31468)

Höhenbezug: Regensburger Höhennetz aus 1927 in m ü.NN(≠ DHHN12/ 92/ 2016 des LDBV)

Planung :

INGENIEURGESELLSCHAFT mbH

architekten und landschaftsarchitekten

landschaftsarchitekten

Arbeitsgemeinschaft TEAM 3

entw. : 3/2024	team 3
gez. : 4/2025	UB
gepr. : 5/2025	WWA

30.04. 2025

Datum

Unterschrift Entwurfsverfasser

26.05. 2025

Datum

Unterschrift Vorhabensträger