


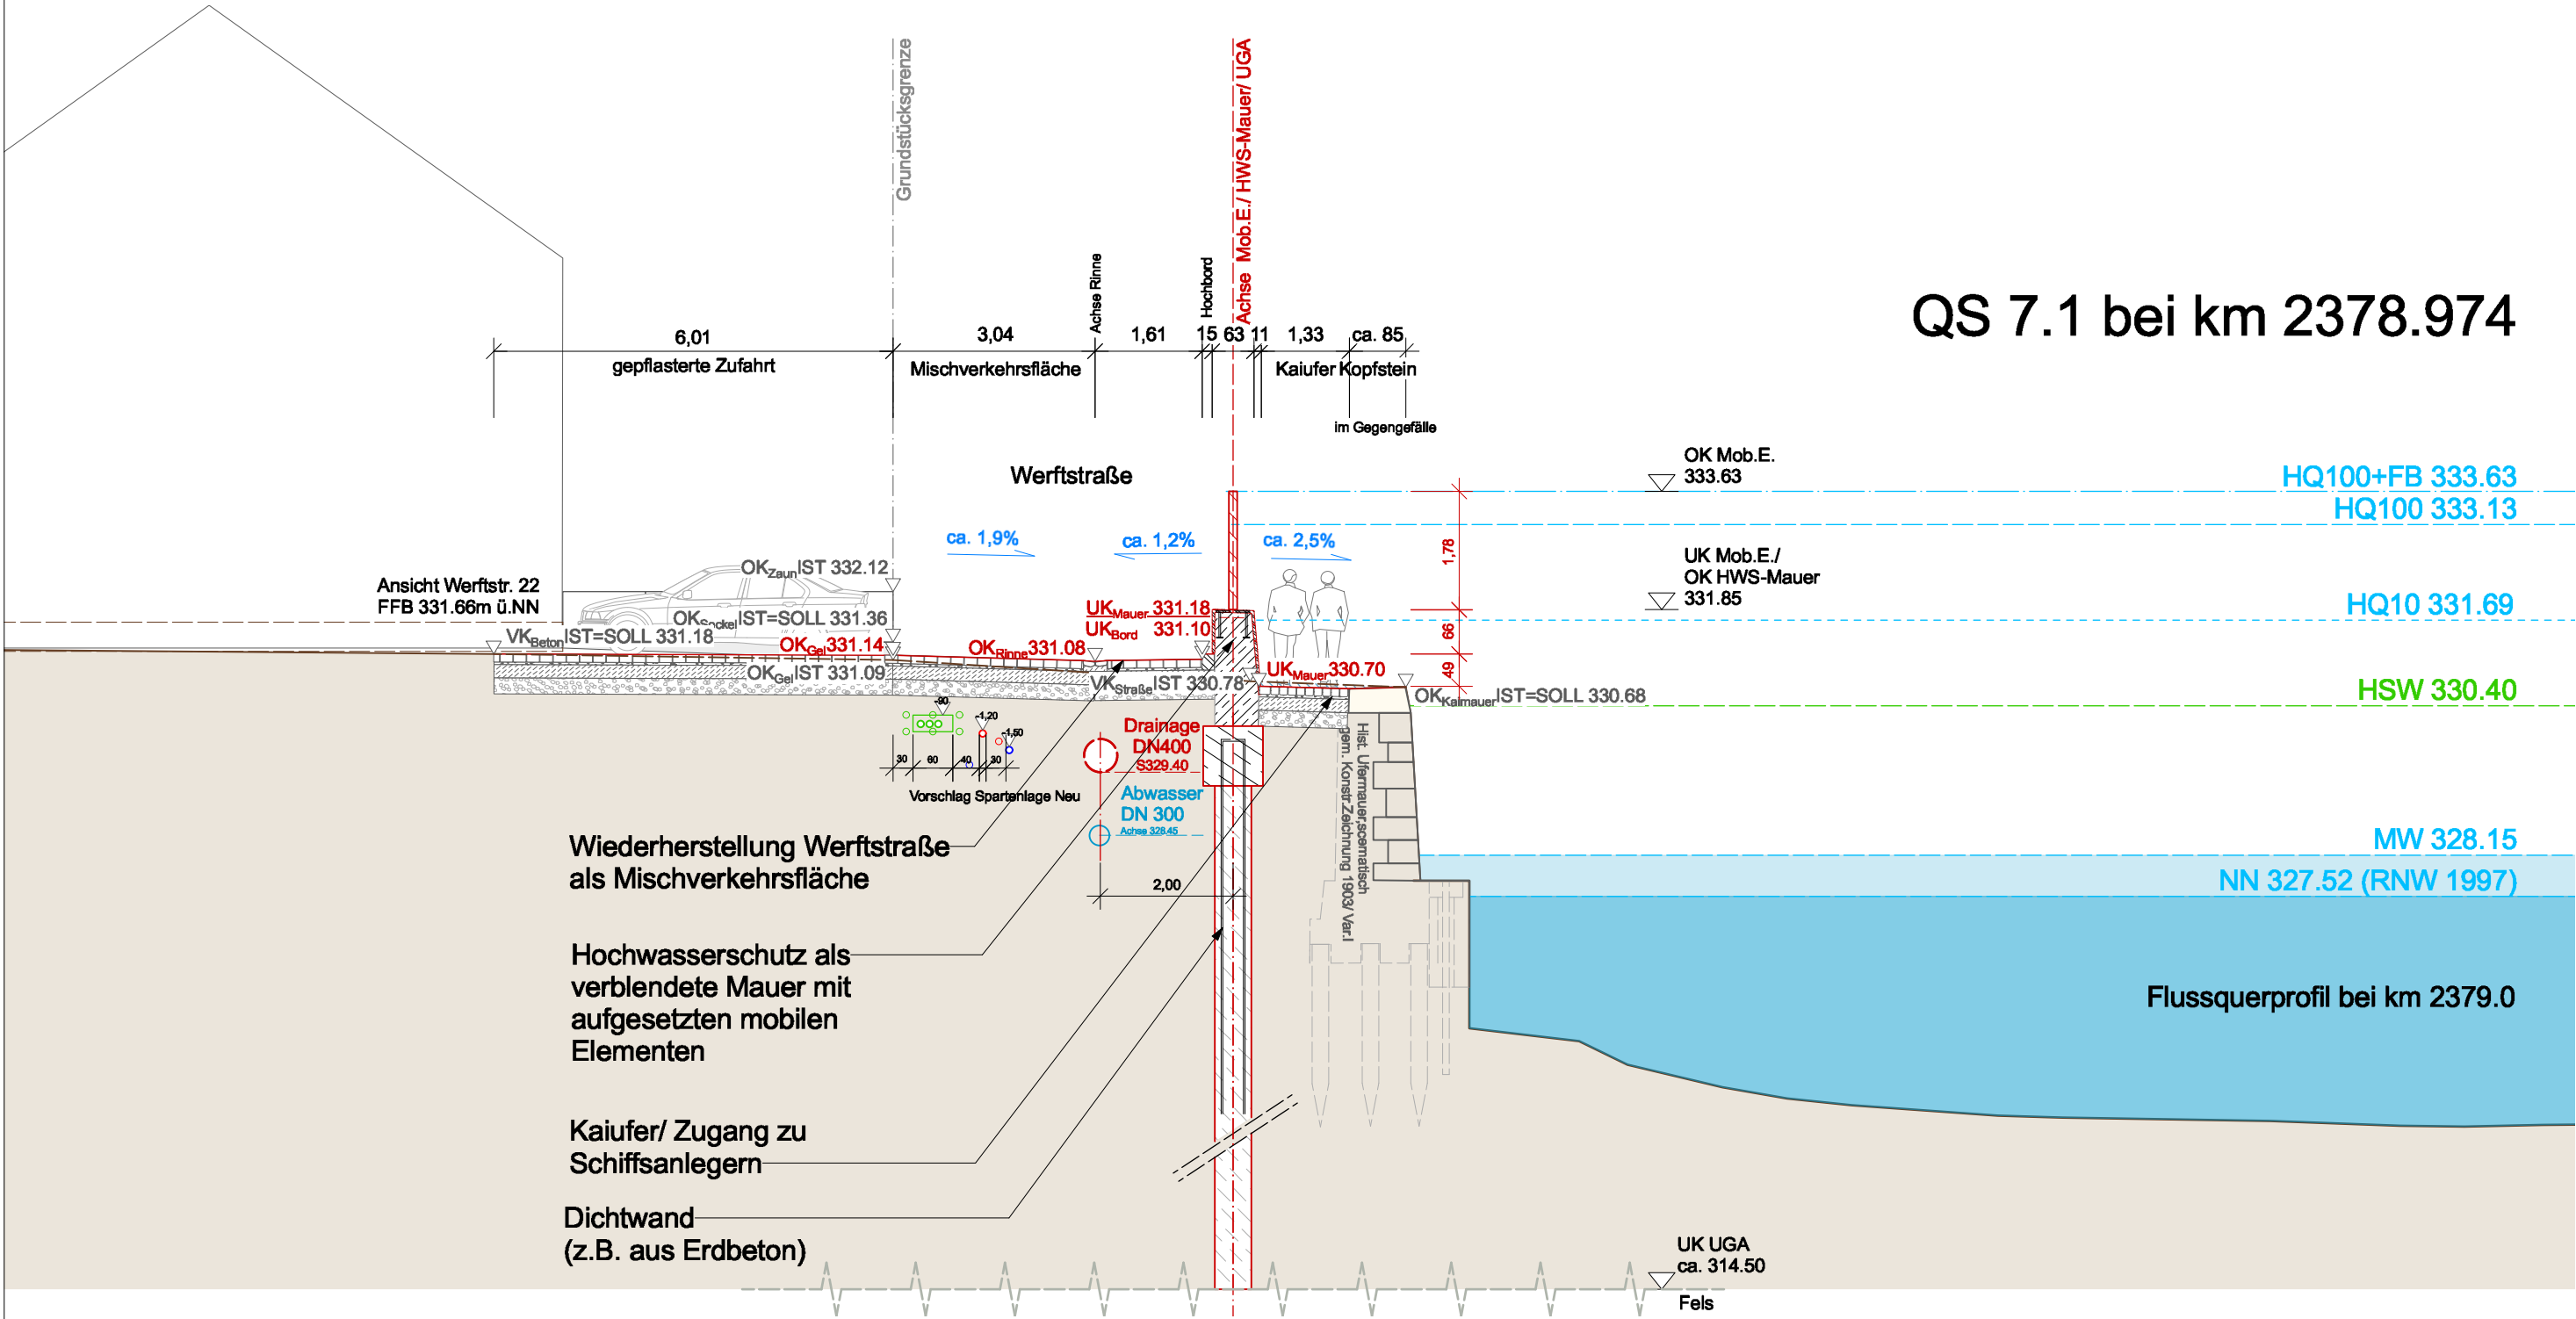

LEGENDE

OK_{Gel} IST 329.71

Abwasser DN300 329.70

Straßenentw. verlegt DN300 329.70

OK_{Gel} 332.50

geplante Höhe

geplanter Geländeverlauf oberhalb Bestand (Aufschüttung)

mit beispielhaftem Bodenaufbau und beispielhafter neuer Versorgertrasse/ Gas/ Trinkwasser

geplanter Geländeverlauf unterhalb Bestand (Abtrag)

Neupflanzung/ Baumbestand

HWS-Maßnahme (in Schnittachse)

HWS-Mauer (in der Ansicht)

Untergrundabdichtung

Gründung

Abbruchmaßnahmen/ Entfall Baumstandort

Vermerke Genehmigungsbehörde :

Wasserwirtschaftsamt Regensburg

STADT REGENSBURG

c					
b					
a					
Index	Bemerkung	geändert am	Name	geprüft am	Name

Übersichtslageplan

Vorhaben :

Landkreis/ Stadt :

Vorhabensträger :

Maßstab :

Planung :

Hochwasserschutz Regensburg

Abschnitt H Unterer Wöhrd

PLANFESTSTELLUNG

Regensburg

Freistaat Bayern, Wasserwirtschaftsamt Landshuter Straße 59, 9053 Regensburg

M 1:100

Planinhalt : Planabschnitt (PA) 7 Querschnitt 7.1, Werftstr. 22

Arbeitsgemeinschaft TEAM 3

schönigplan INGENIEURGESELLSCHAFT mbH

ARCHISCAP architekten und landschaftsarchitekten

lrm Landschaftsarchitekten

Plan-Code :

Anlage :

Phase :

Plan-Nr. :

Vorhabenskennzeichen:

Lagebezug:

Höhenbezug:

entw. :

gez. :

gepr. :

36200-G-B 7.1.1

B 7.1.1

G

RB-H- QS 7.1-100

G11 3620001015

GK4 (EPSG 31468)

Regensburger Höhennetz aus 1927 in m ü.NN (≠ DHH-N12/ 92/ 2016 des LDBV)

3/2024

4/2025

5/2025

team 3

UB

WWA

30.04. 2025


Datum

Unterschrift Entwurfsverfasser

26.05. 2025

Datum

Unterschrift Vorhabensträger

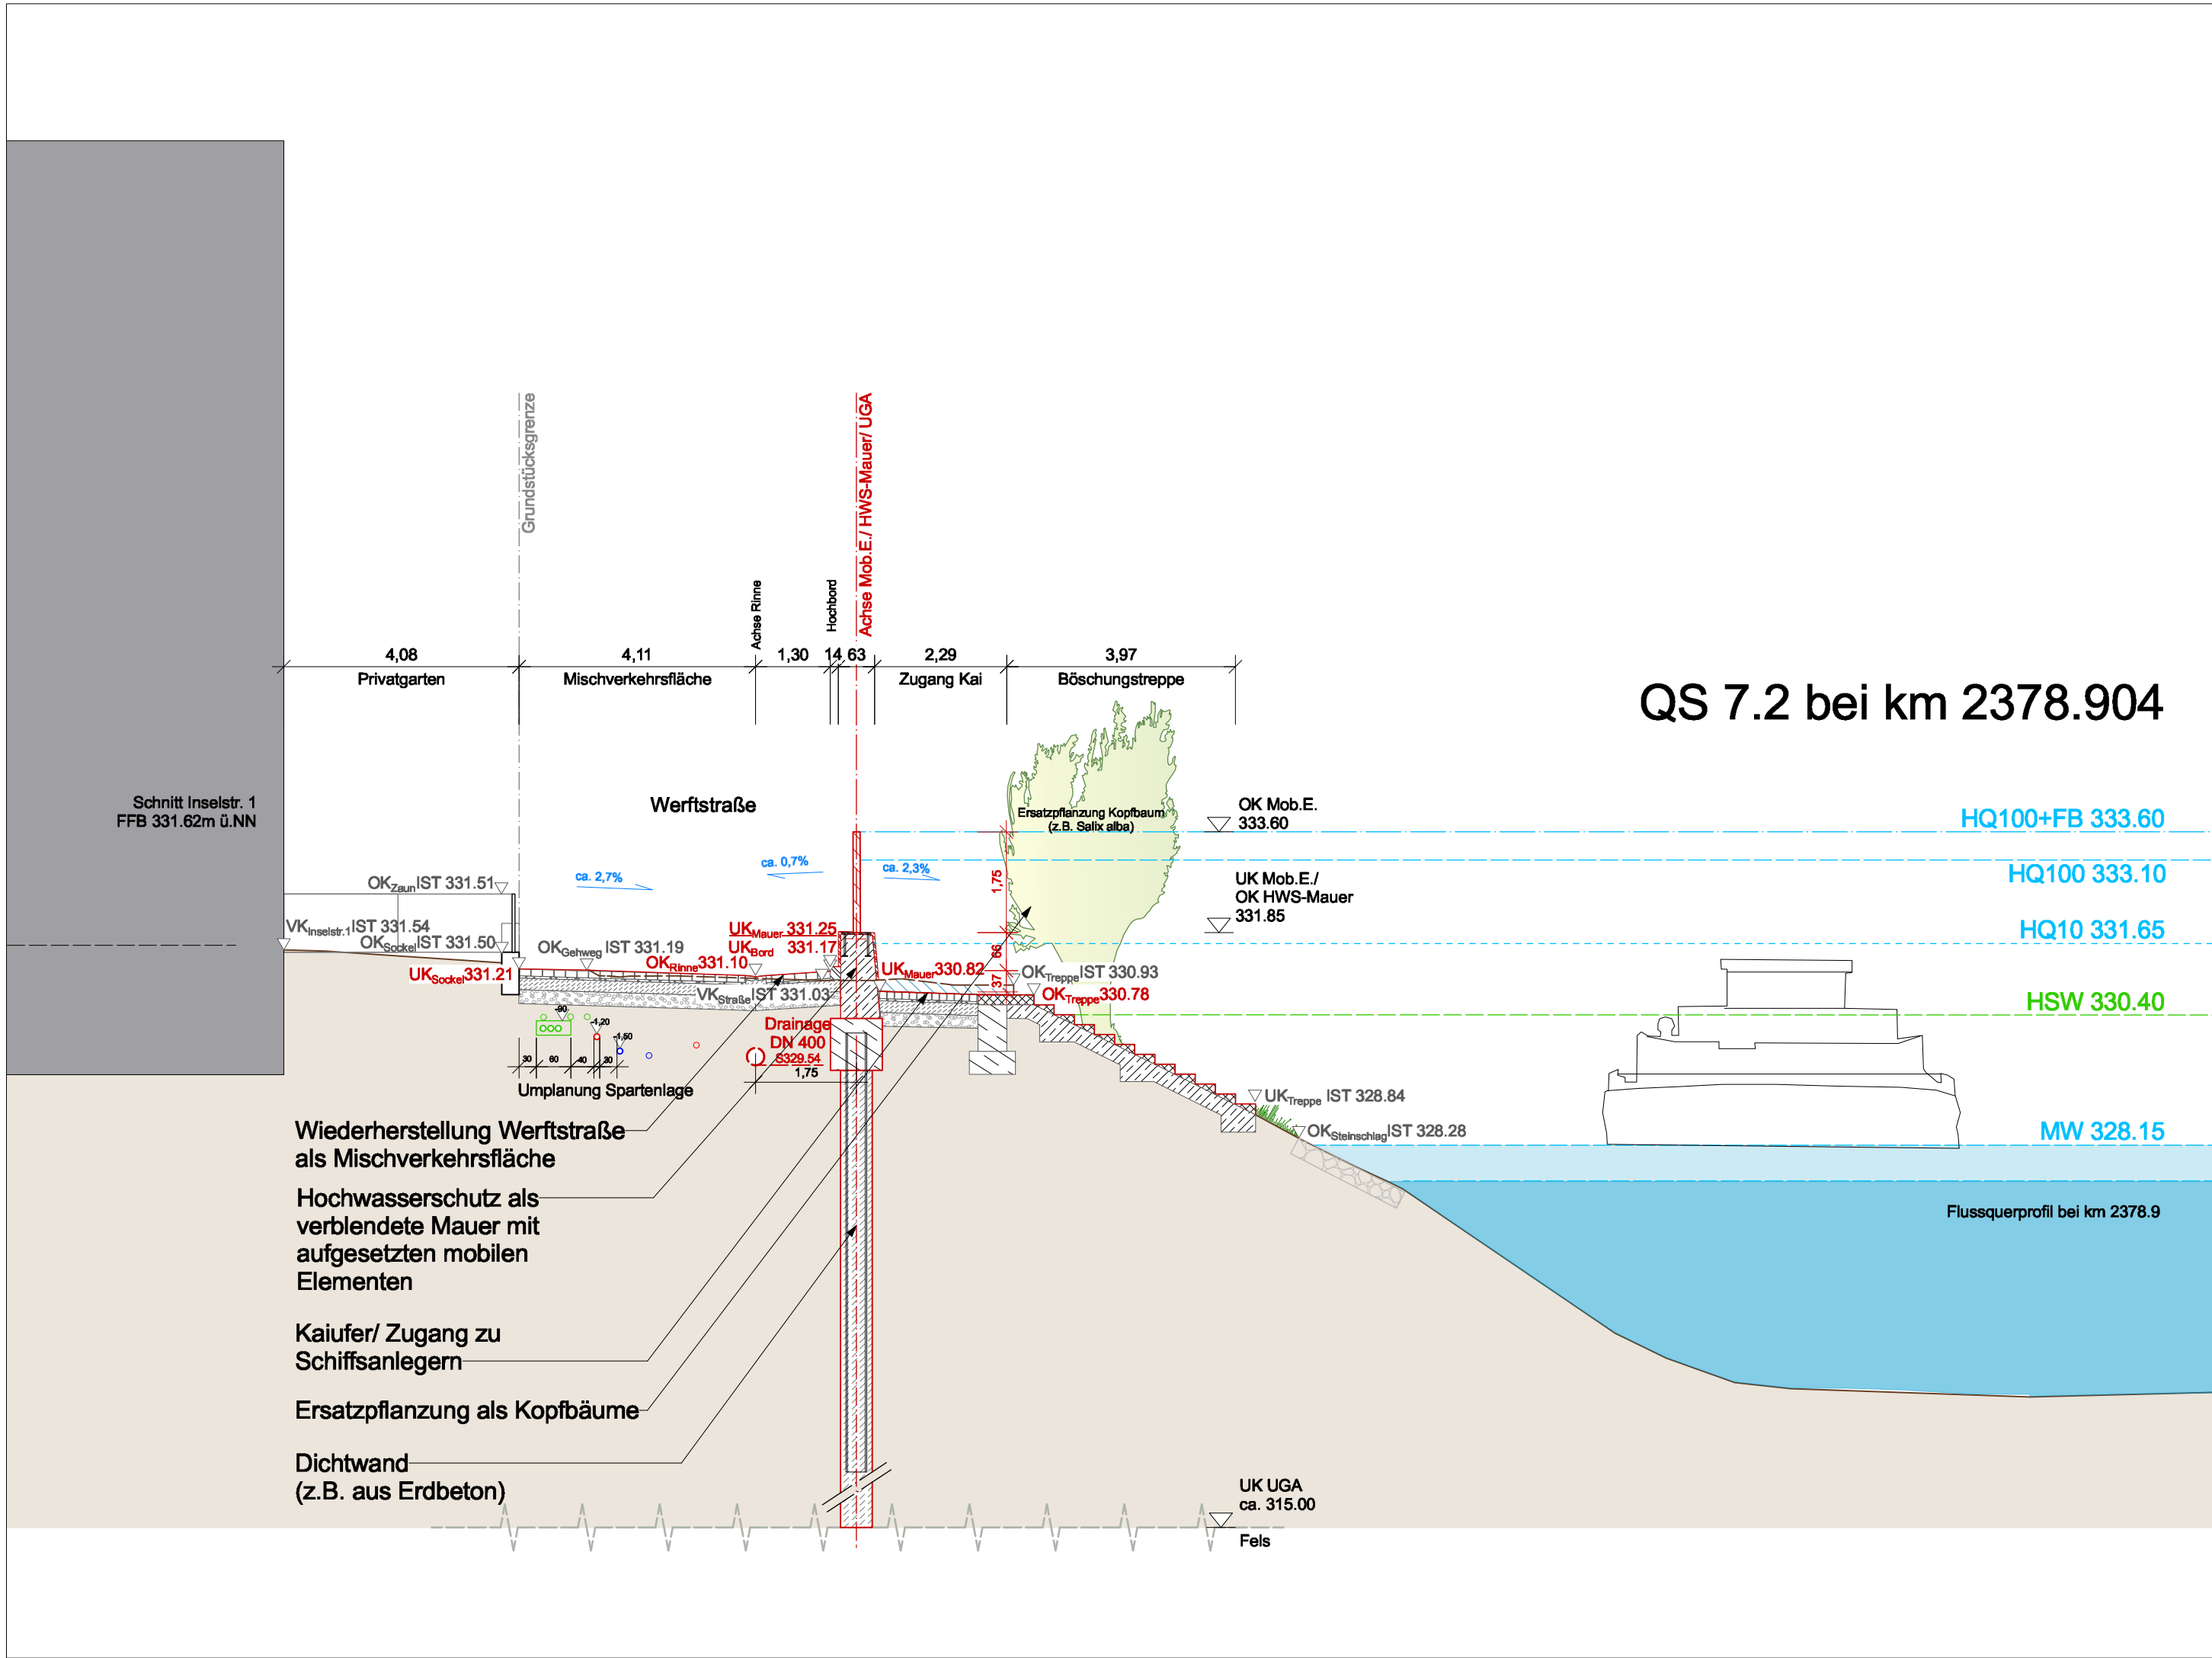




**Abbruchmaßnahmen/
Entfall Baumstandort**

**STADT
REGENSBURG**

30.04.2025		26.05.2025	
Datum	Unterschrift Entwurfsverfasser	Datum	Unterschrift Vorhabensträger

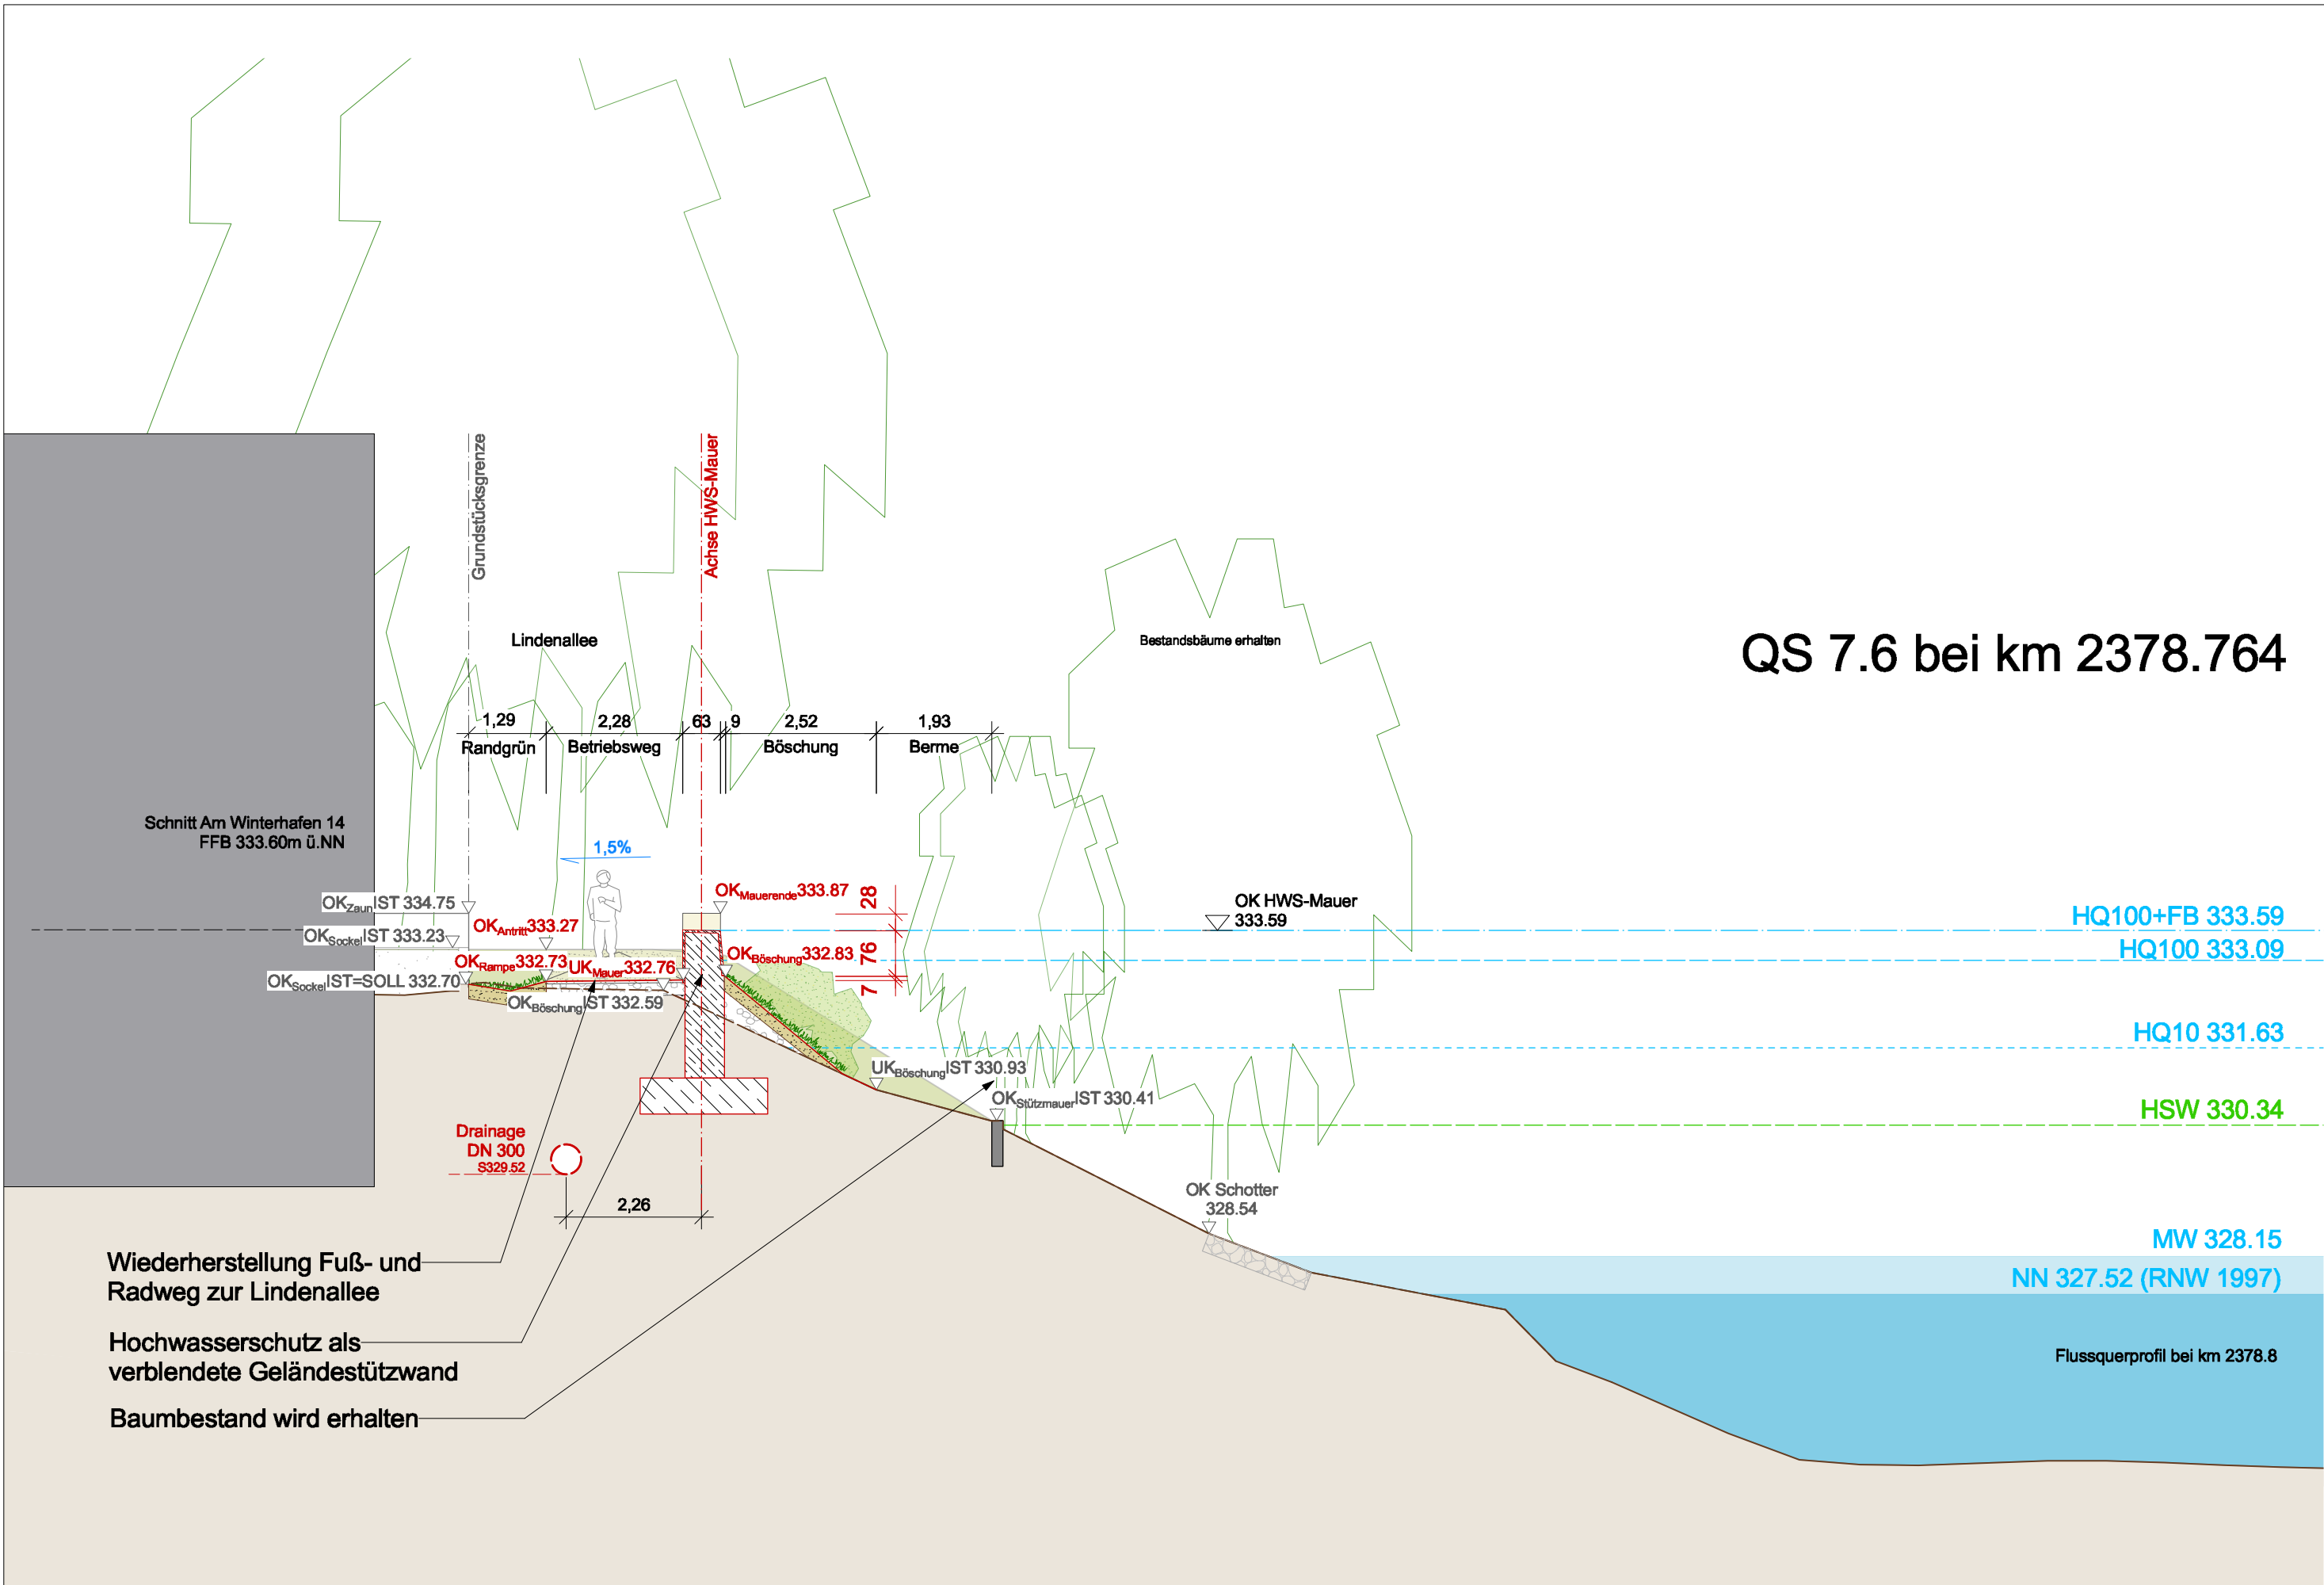

QS 7.6 bei km 2378.764

LEGENDE

OK_{Gel} IST 329.71

Abwasser DN300 S329.70

Straßenentw. verlegt DN300 S329.70

OK_{Gel} 332.50

-0.00

-1.20

-1.50

geplanter Geländeverlauf unterhalb Bestand (Abtrag)

Bestandshöhe
Geländeverlauf im Bestand
mit bestehendem Abwasserkanal/
geplantem Kanal für die Straßen-
entwässerung und bestehender
Versorgertrasse/ Gas/ Trinkwasser

geplante Höhe
geplanter Geländeverlauf
oberhalb Bestand (Aufschüttung)
mit beispielhaftem Bodenaufbau
und beispielhafter neuer
Versorgertrasse/ Gas/ Trinkwasser

geplanter Geländeverlauf
unterhalb Bestand (Abtrag)

Neupflanzung/
Baumbestand

HWS-Maßnahme
(in Schnittachse)

HWS-Mauer
(in der Ansicht)

Untergrundabdichtung

Gründung

Abbruchmaßnahmen/
Entfall Baumstandort

Vermerke Genehmigungsbehörde :

Wasserwirtschaftsamt
Regensburg

STADT
REGENSBURG

c					
b					
a					
Index	Bemerkung	geändert am	Name	geprüft am	Name

Übersichtslageplan

Vorhaben :	Hochwasserschutz Regensburg Abschnitt H Unterer Wöhrd PLANFESTSTELLUNG	Plan-Code : 36200-G-B 7.1.6		
		Anlage : B 7.1.6	Phase : G	
Landkreis/ Stadt :	Regensburg	Plan-Nr. : RB-H- QS 7.6-100		
Vorhabensträger :	Freistaat Bayern, Wasserwirtschaftsamt Landshuter Straße 59, 9053 Regensburg	Vorhabenskennzeichen: G11 3620001015		
Maßstab :	Planinhalt : Planabschnitt (PA) 7 Querschnitt 7.6, Rampe Lindenallee	Lagebezug: GK4 (EPSG 31468)		
		Höhenbezug: Regensburger Höhennetz aus 1927 in m ü.NN(≠ DHH-N12/ 92/ 2016 des LDBV)		
Planung :	Arbeitsgemeinschaft TEAM 3	entw. :	3/2024	team 3
		gez. :	4/2025	UB
		gepr. :	5/2025	WWA

30.04. 2025

Datum

Unterschrift Entwurfsverfasser

26.05. 2025

Datum

Unterschrift Vorhabensträger