




< Planabschnitt (

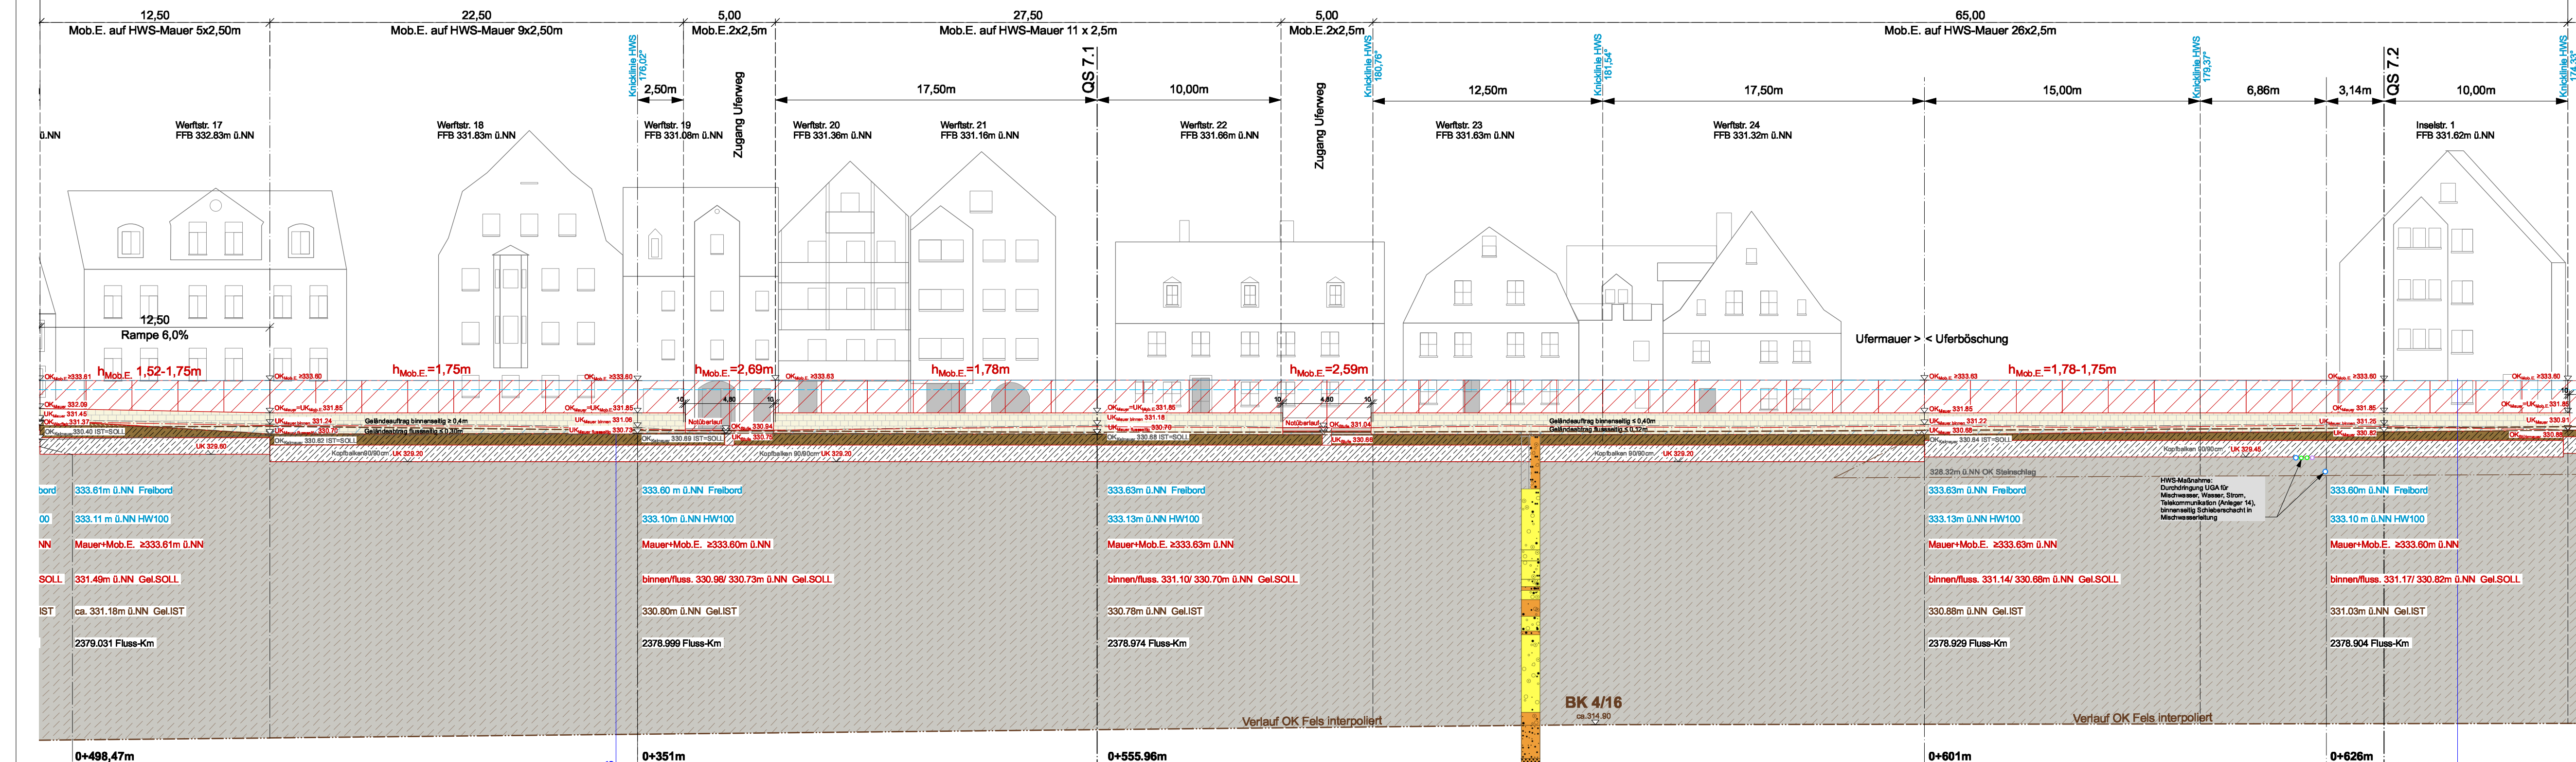

Planabschnitt 7.2

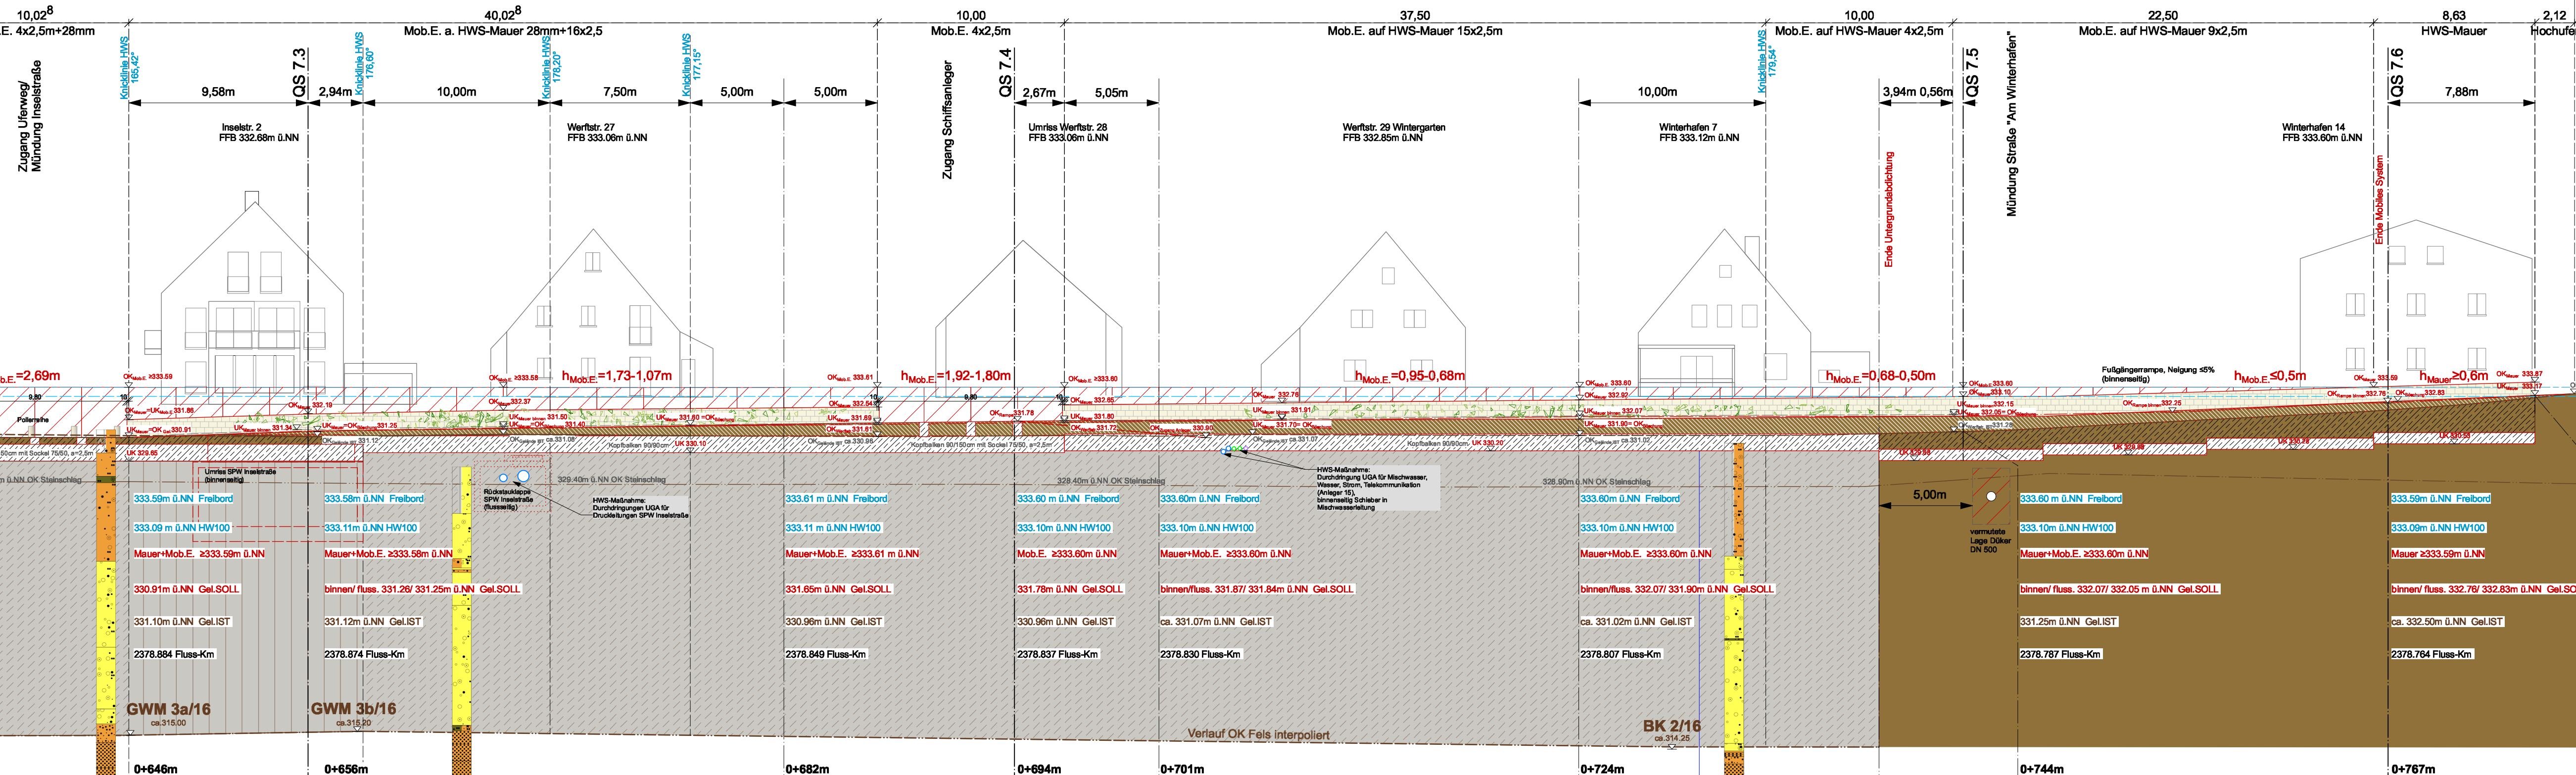

> Planabschnitt 8

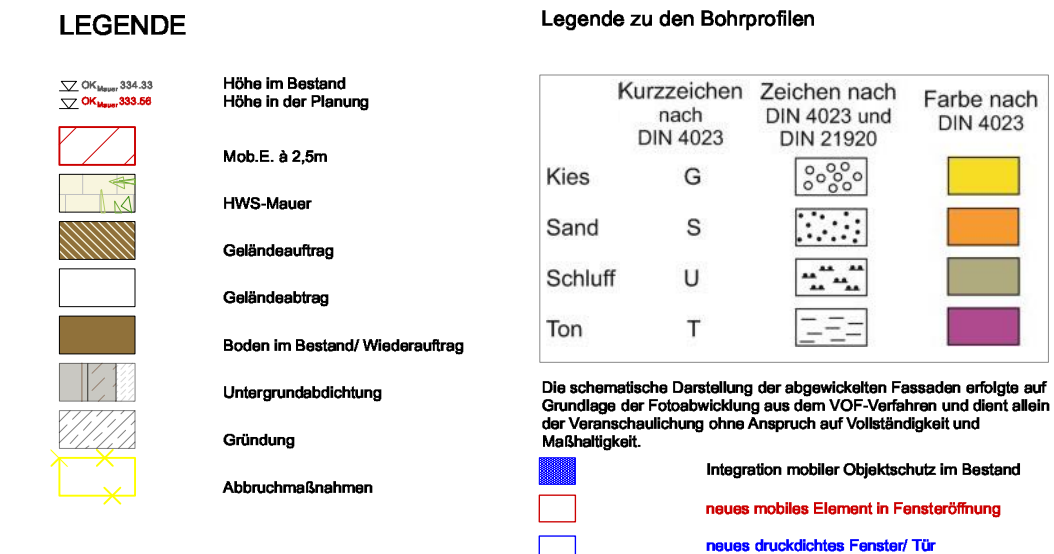

Vermerke Genehmigungsbehörde :

Wasserwirtschaftsamt
Regensburg

STADT
REGENSBURG

c				
b				
a				
Index	Bemerkung	geändert am	Name	geprüft am

Oberachthalgebiet

Vorhaben :	Hochwasserschutz Regensburg Abschnitt H Unterer Wöhrd PLANFESTSTELLUNG	Plan-Code :	36200-G
		Anlage :	B 7.2.0

Landkreis/ Stadt :	Regensburg	Plan-Nr. :	RB-H- LA 7
Vorhabensträger :	Freistaat Bayern, Wasserwirtschaftsamt Landshuter Straße 59, 9053 Regensburg	Vorhabenskenntzeichen:	G11 3820001015

Maßstab : M 1:200	Planinhalt: Planabschnitt (PA) 7 Längsabwicklung Östliche Wertstraße Wertstr. 17 bis Am Winterhafen 14	Lagebezug: GK4 (EPSG 31466) Höhenbezug: Regensburger Höhe 1927 in m ü.NN (+ 2018 des LD8V)
--------------------------	---	---

Planung :		Arbeitsgemeinschaft TEAM 3		anw. : 3/2024	
 INGENIEURGESELLSCHAFT mbH		 architekten und landschaftsarchitekten		gez. : 4/2025	
 Landschaftsarchitekten		gepr. : 5/2025			

30.04.2025		26.05.2025	
Datum	Unterschrift Entwurfsverfasser	Datum	Unterschrift Vorhabensträger