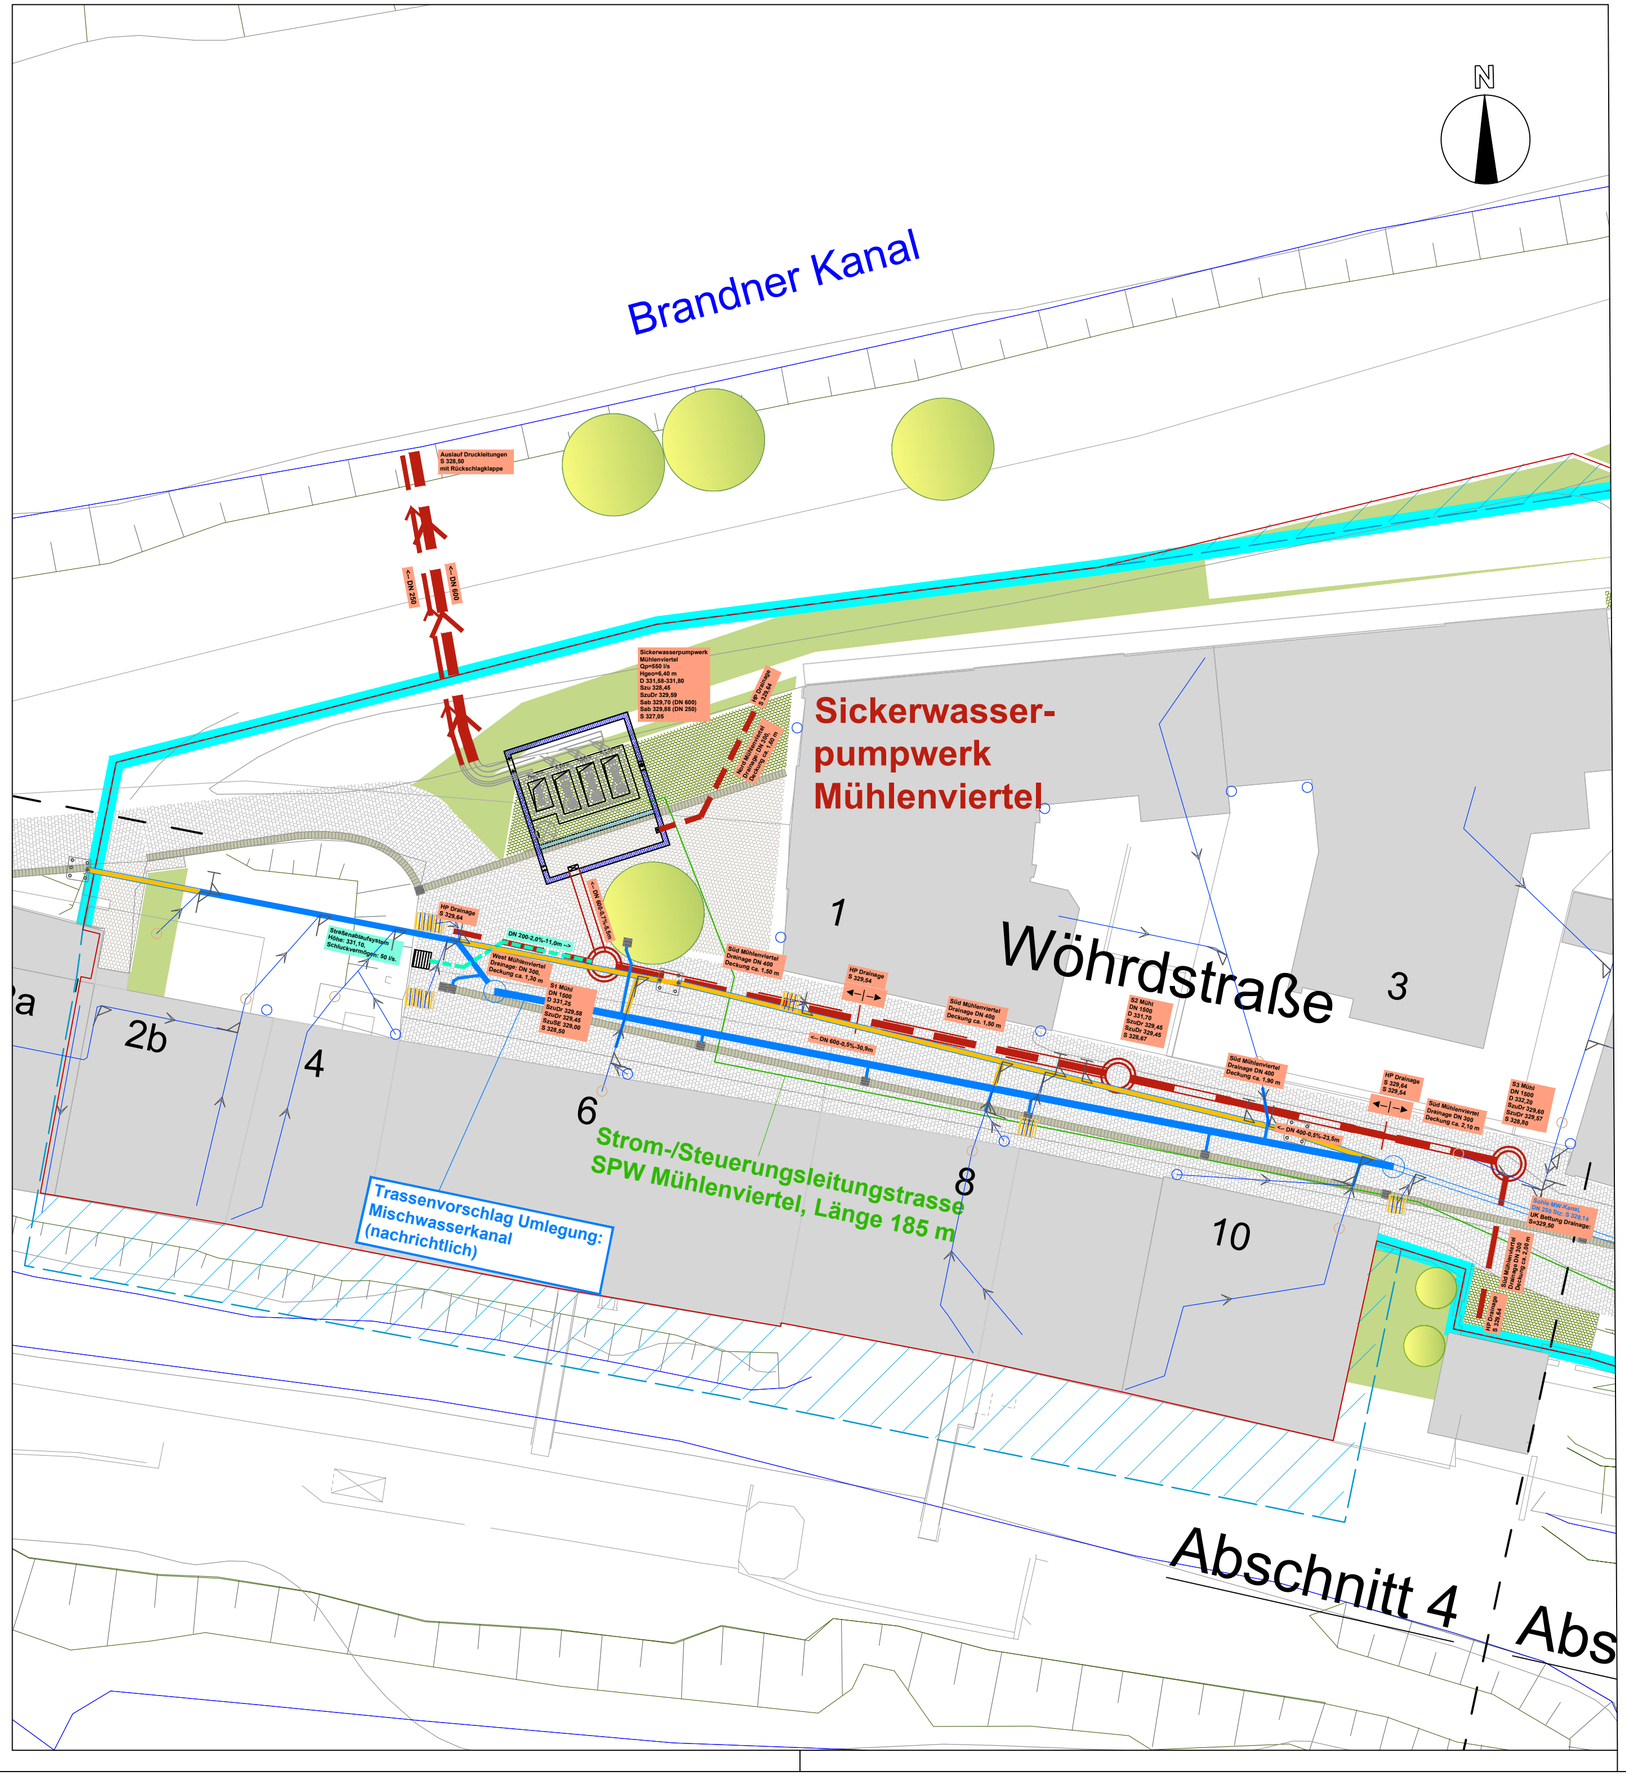

ZEICHENERKLÄRUNG

Planung

- Hochwasserschutzlinie
- Untergrundabdichtung (vertikal und horizontal)
- Kopfbalken
- DN 1000 — Drainagerohr mit Schacht, teilweise mit Transportkanal
- Sickerwasser-/Kompaktpumpwerk mit Druckleitung
- Ablaufsystem für Notüberlauf bei Starkregen
- Straßenablauf mit Muldenrinne
- <-- SE40 — Anschlussleitungen Straßenabläufe
- Ersatztrasse Abwasserkanal mit Anschlussleitung (nachrichtlich) Stadt plant Neuordnung der Entwässerung
- bestehender Abwasserkanal entfällt
- bestehende Kanalhausanschlussleitung entfällt
- bestehender Straßenablauf entfällt

Bestand

- Abwasserkanal
- Kanalhausanschlussleitungen

Vermerke Genehmigungsbehörde :

Wasserwirtschaftsamt Regensburg

STADT REGENSBURG

Index	Bemerkung	geändert am	Name	geprüft am	Name
c					
b					
a					

Übersichtslageplan :

Vorhaben :	Hochwasserschutz Regensburg Abschnitt H Unterer Wöhrd PLANFESTSTELLUNG	Plan-Code :	36200-E- C 1.1.1
		Anlage : C 1.1.1	Phase : G
Landkreis/ Stadt :	Regensburg	Plan-Nr. :	RB-H- PA4 LP 250
Vorhabensträger :	Freistaat Bayern, Wasserwirtschaftsamt Landshuter Straße 59, 9053 Regensburg	Vorhabenskennzeichen:	G1t 3620001015
Maßstab : 1:250	Planinhalt : Planabschnitt (PA) 4 Lageplan Mühlenviertel	Lagebezug:	GK4 (EPSG 31468)
		Höhenbezug:	Regensburger Höhennetz aus 1927 in m ü.NN (# DHHN12/ 92/ 2016 des LDBV)
Planung :	Arbeitsgemeinschaft TEAM 3 schömig plan INGENIEURGESELLSCHAFT mbH · ARCHISCAPE architekten und landschaftsarchitekten · gmr Landschaftsarchitekten	entw. :	3/2024 team 3
		gez. :	3/2024 Nikolai, SP
		gepr. :	5/2025 WWA
30.04.2025 Datum	Unterschrift Entwurfsverfasser	26.05.2025 Datum	Unterschrift Vorhabensträger