Drainage-West Zwickel

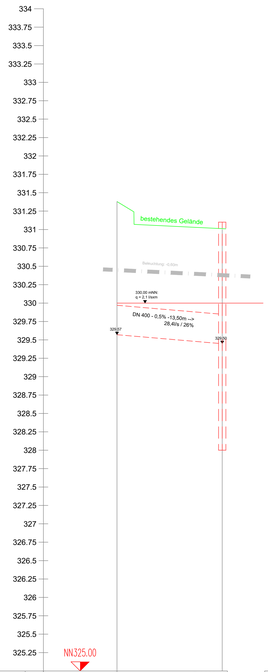

MAßSTAB 1:250/25

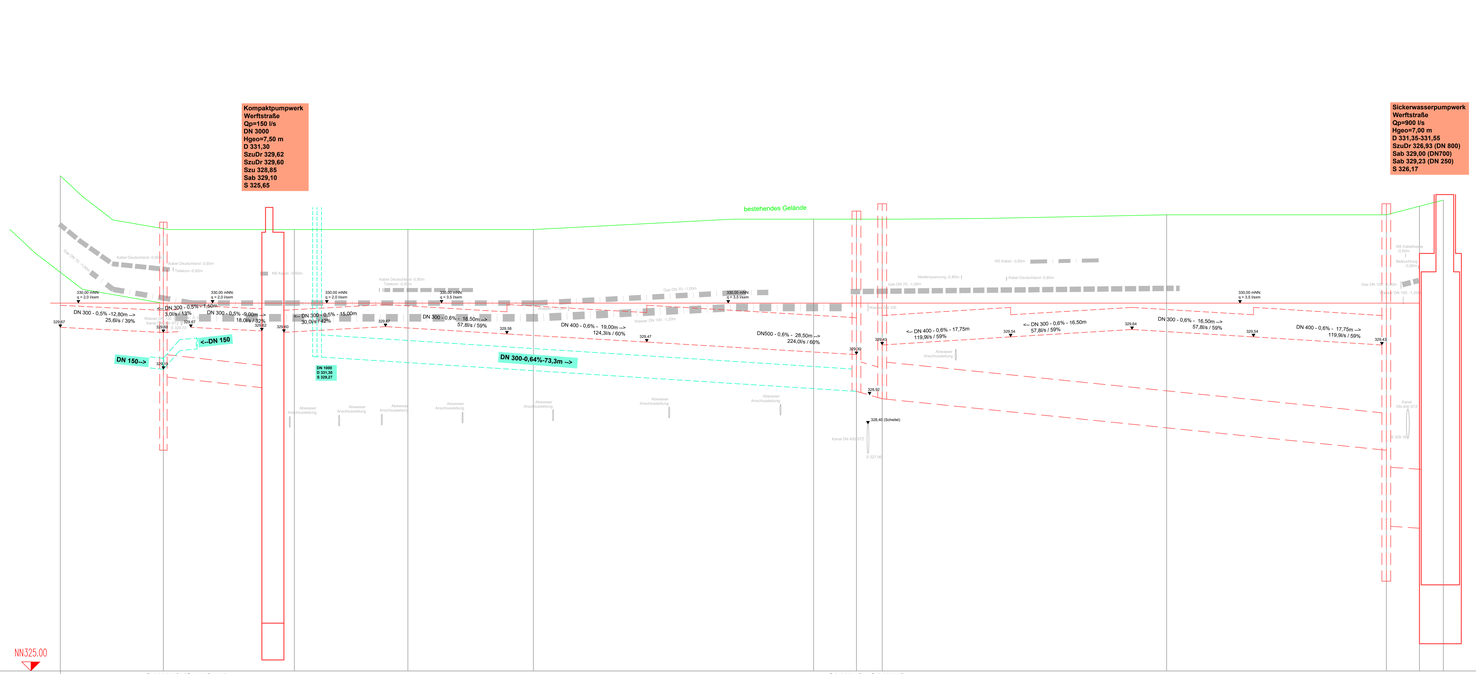

MAßSTAB 1:250/25

| Schacht-Nr. | | | | S4 Werft (Sandfang) | | | |