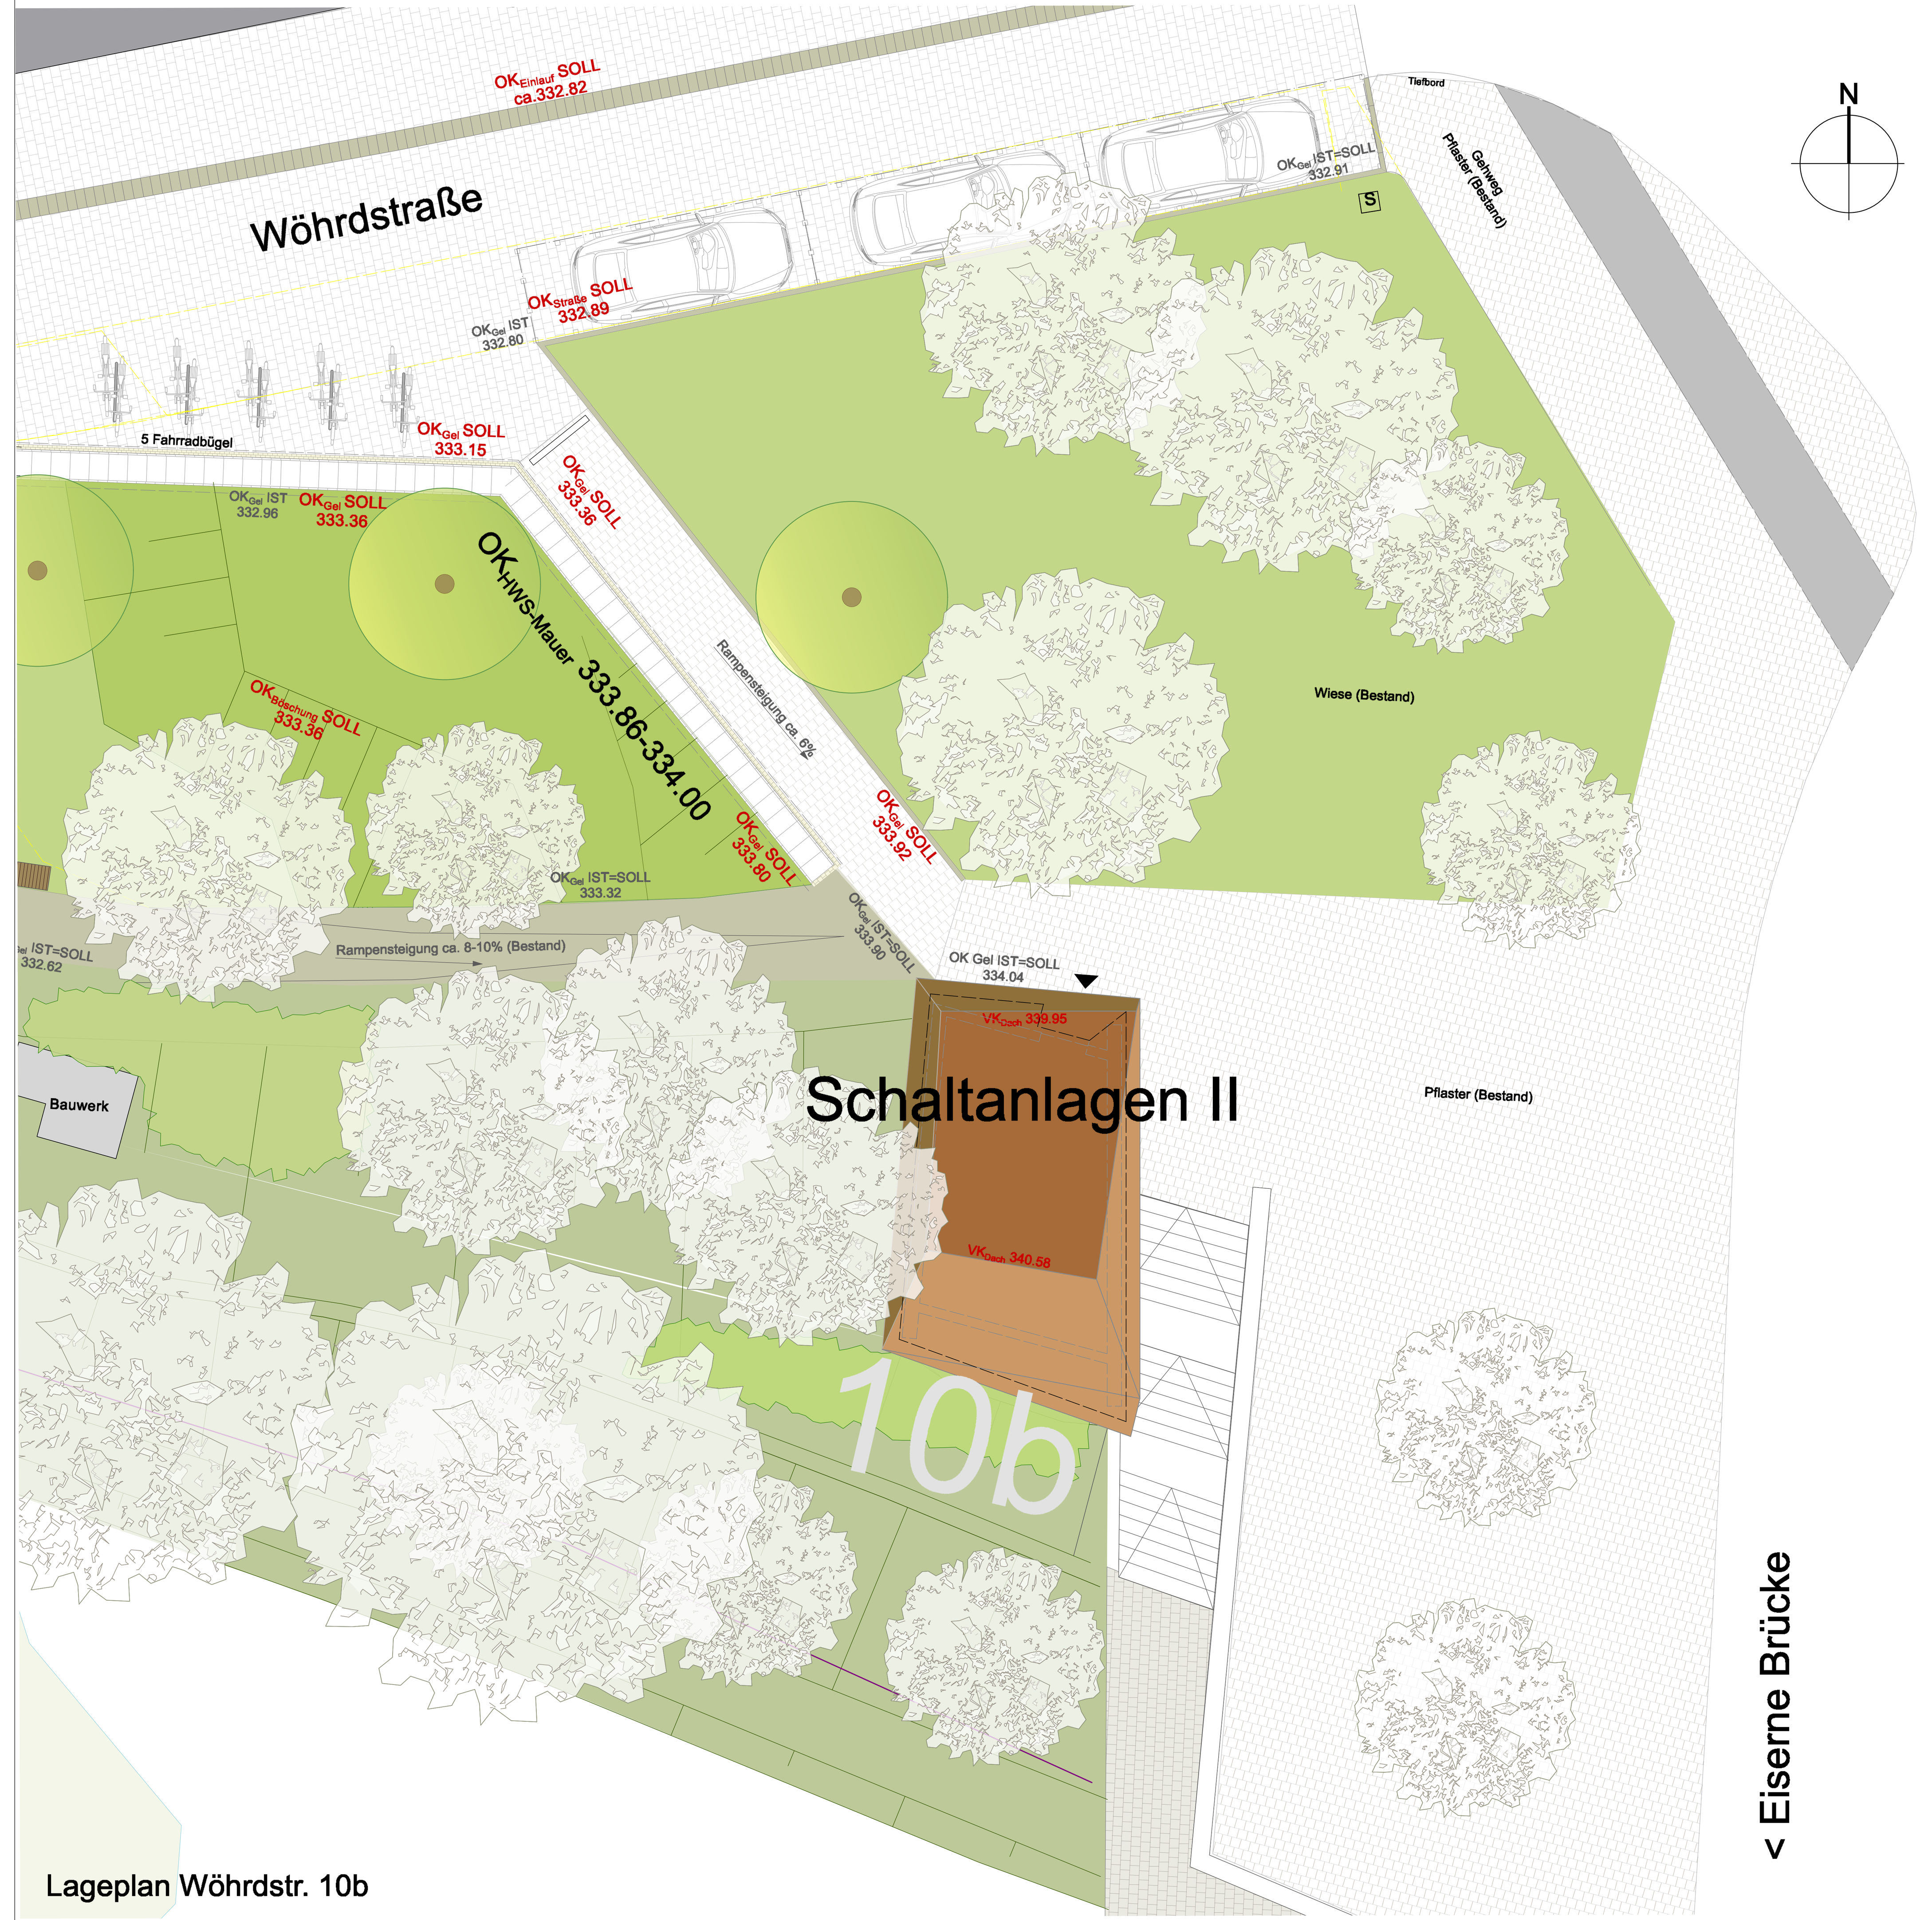

Lageplan Wöhrdstr. 10b

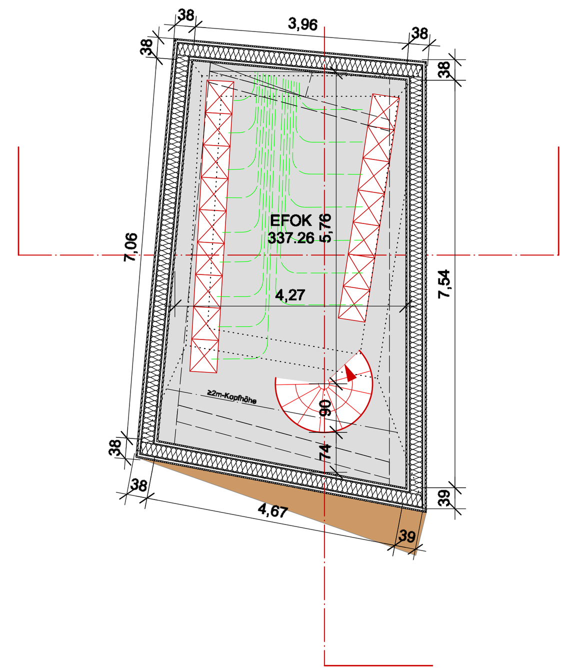

Grundriss Obergeschoss +337.26

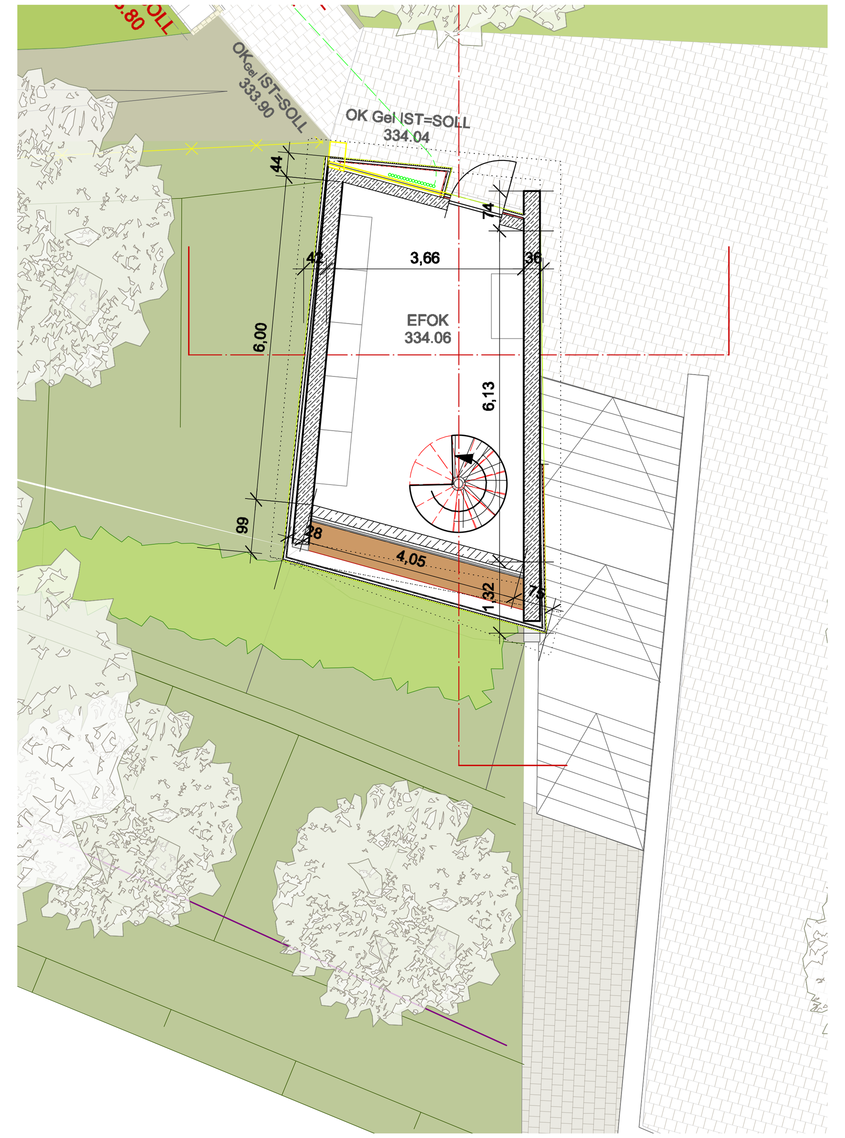

Grundriss EG +334.06

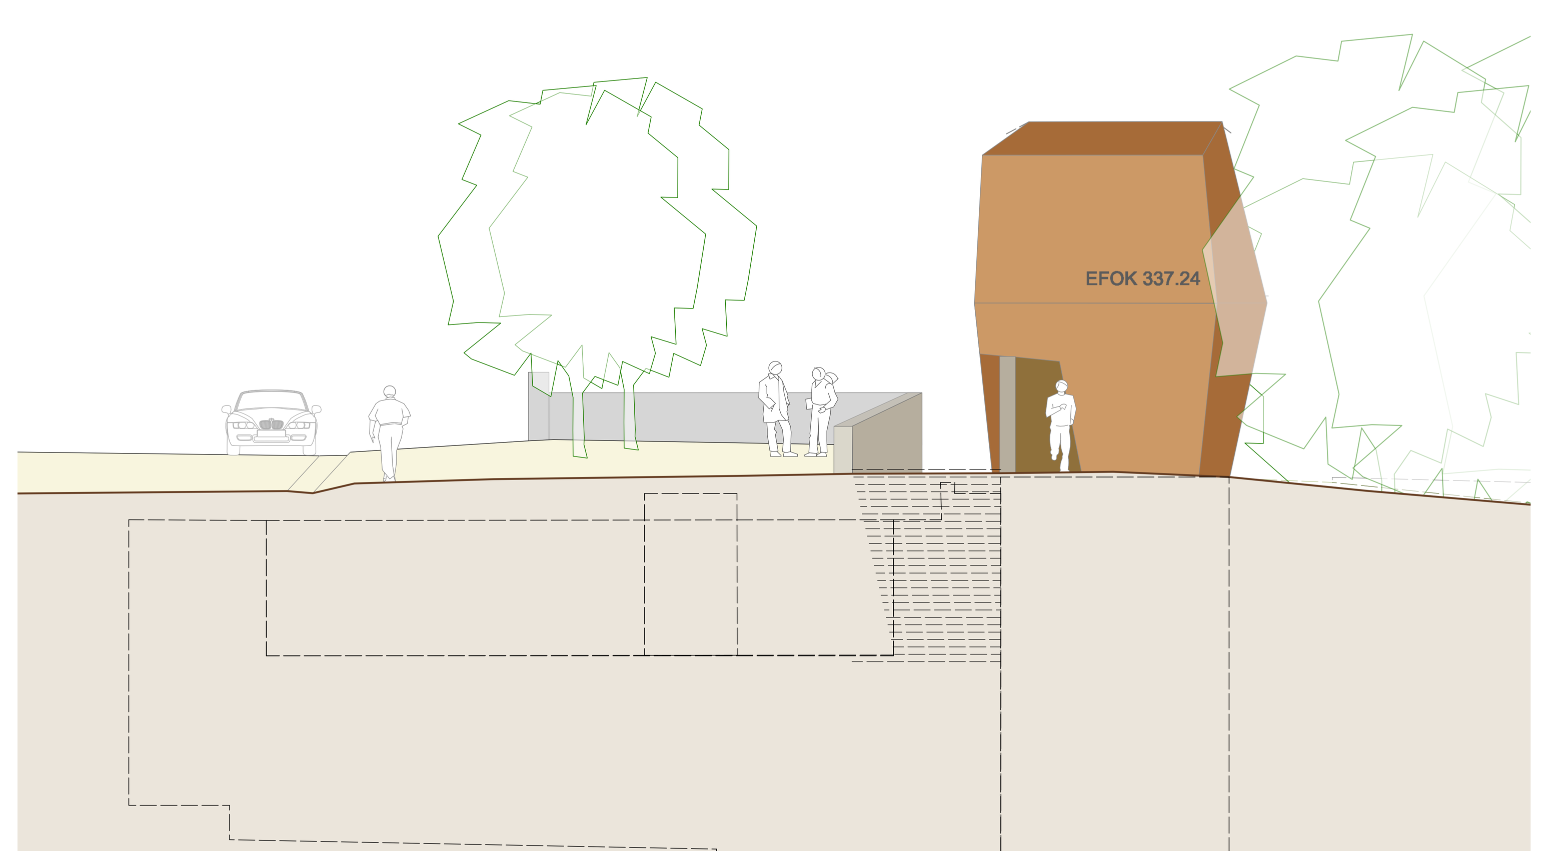

Ansicht aus Norden

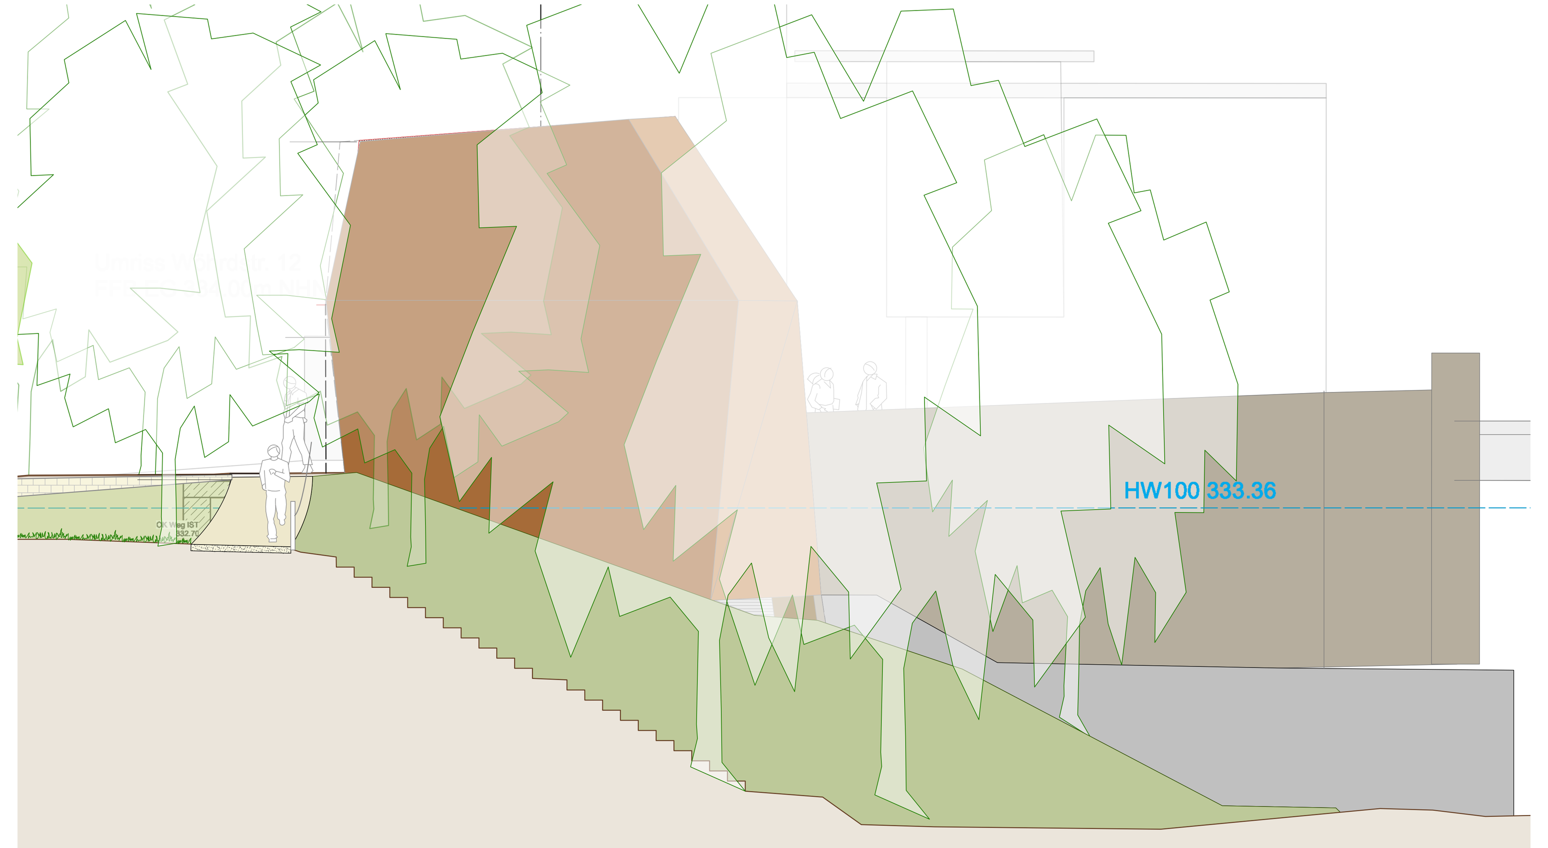

Ansicht aus Westen

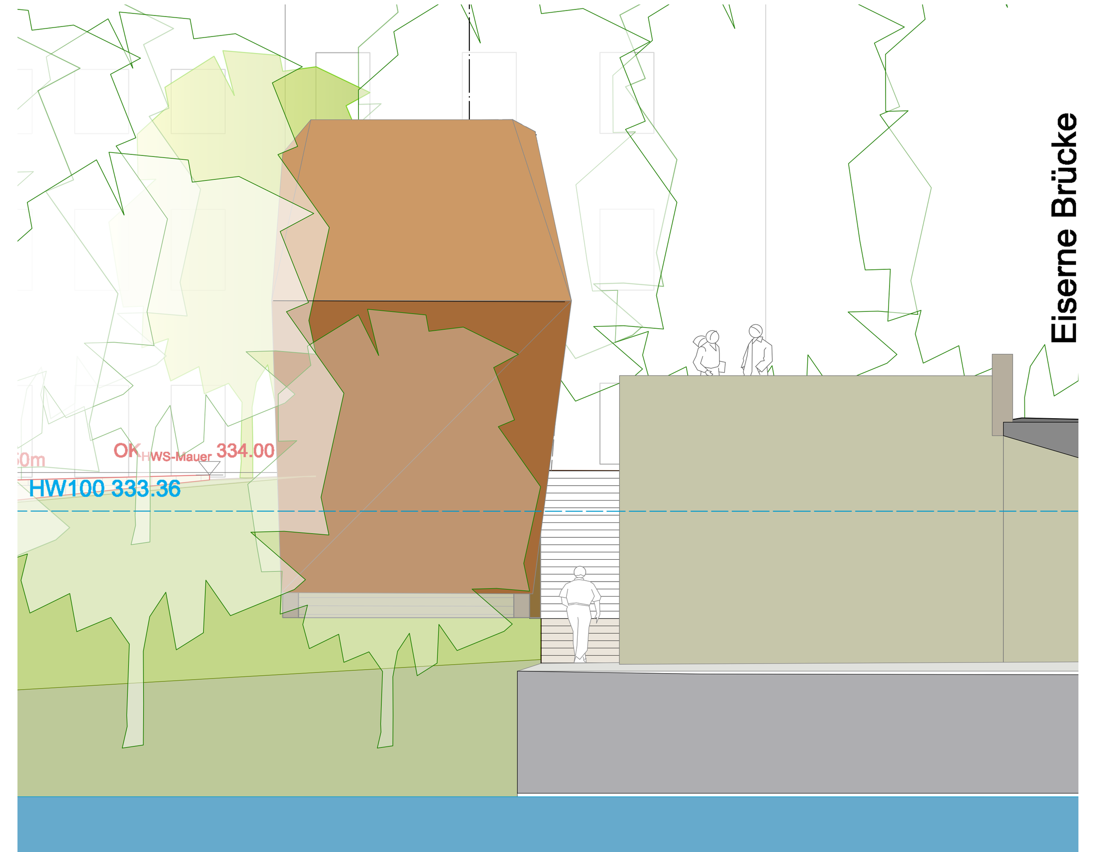

Ansicht aus Süden

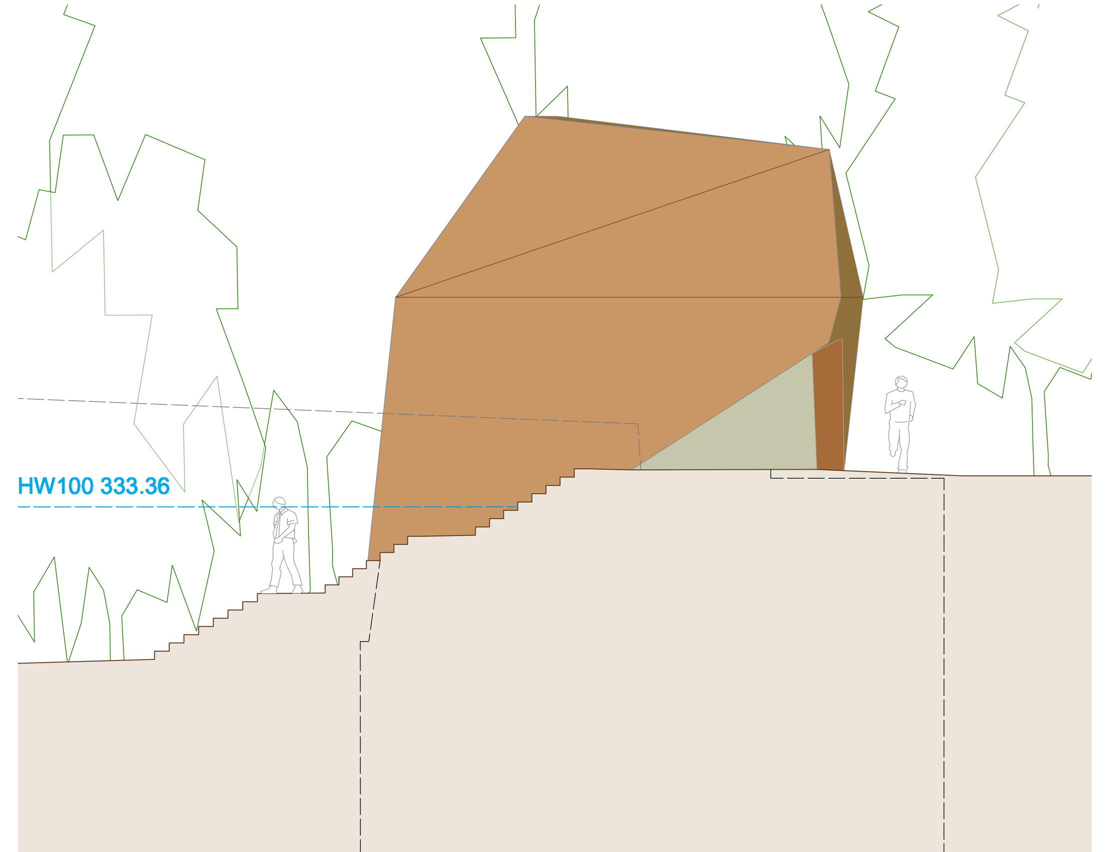

Ansicht aus Osten

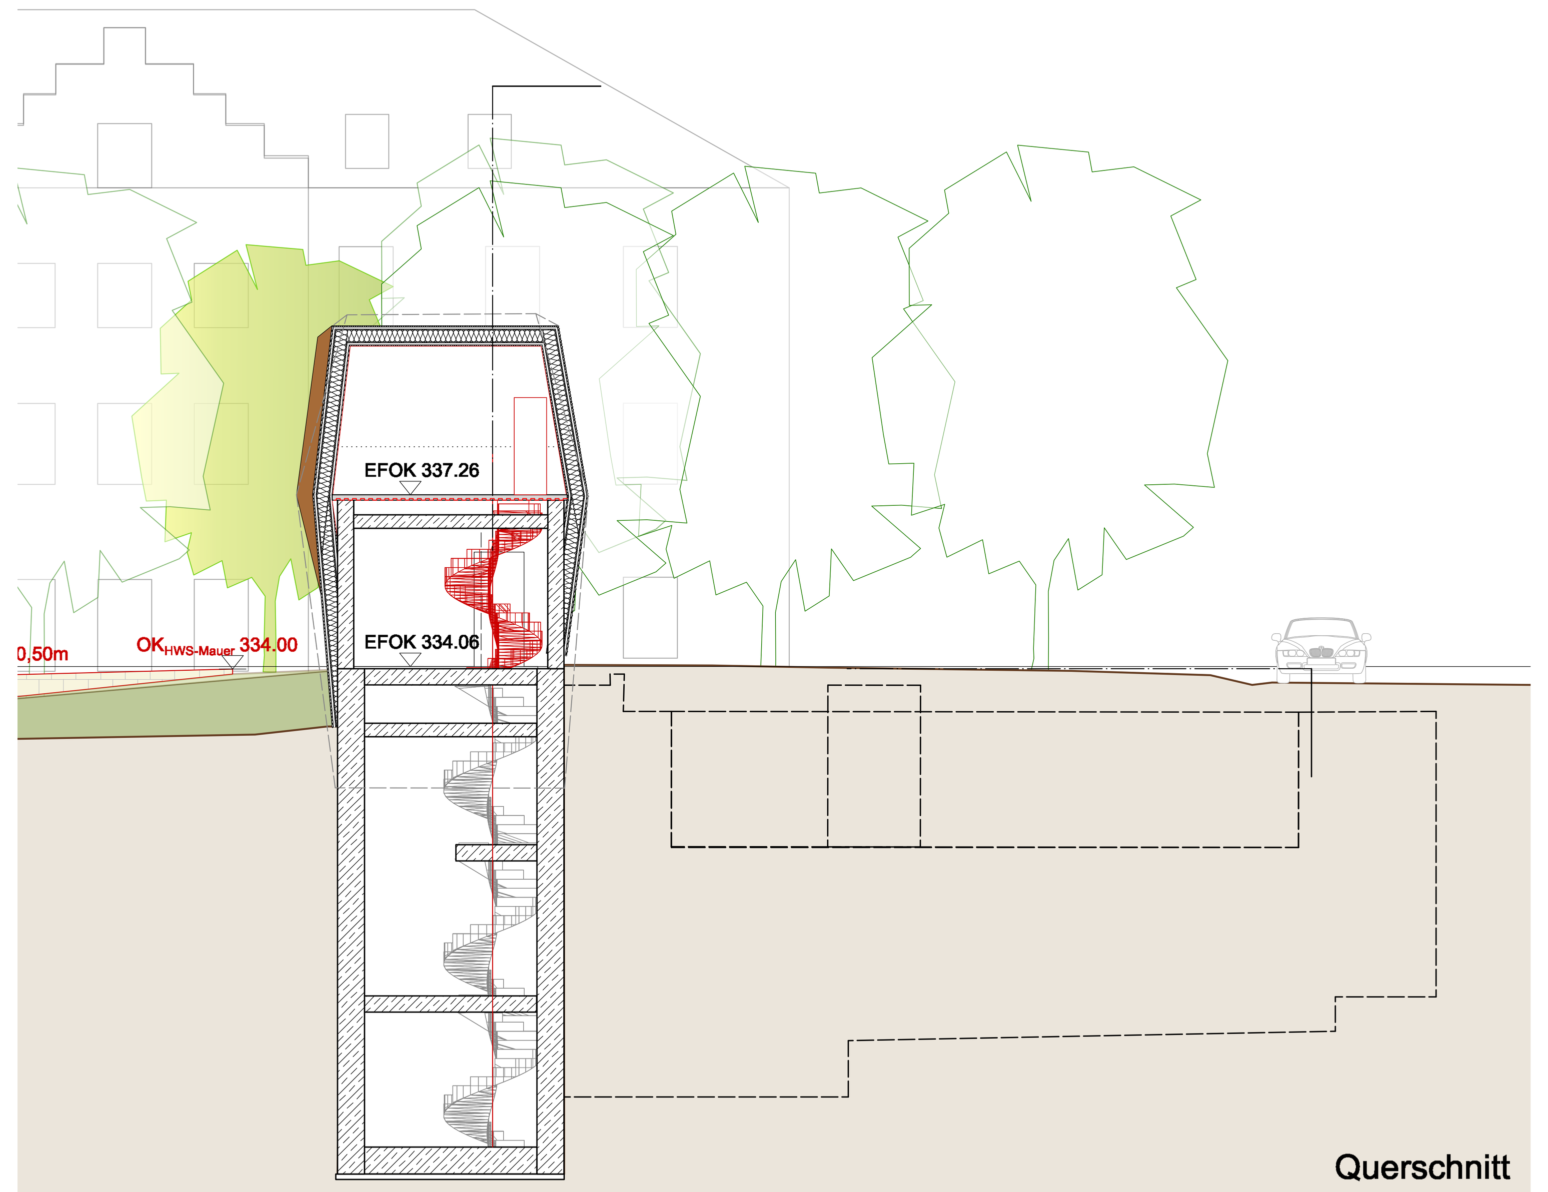

Querschnitt

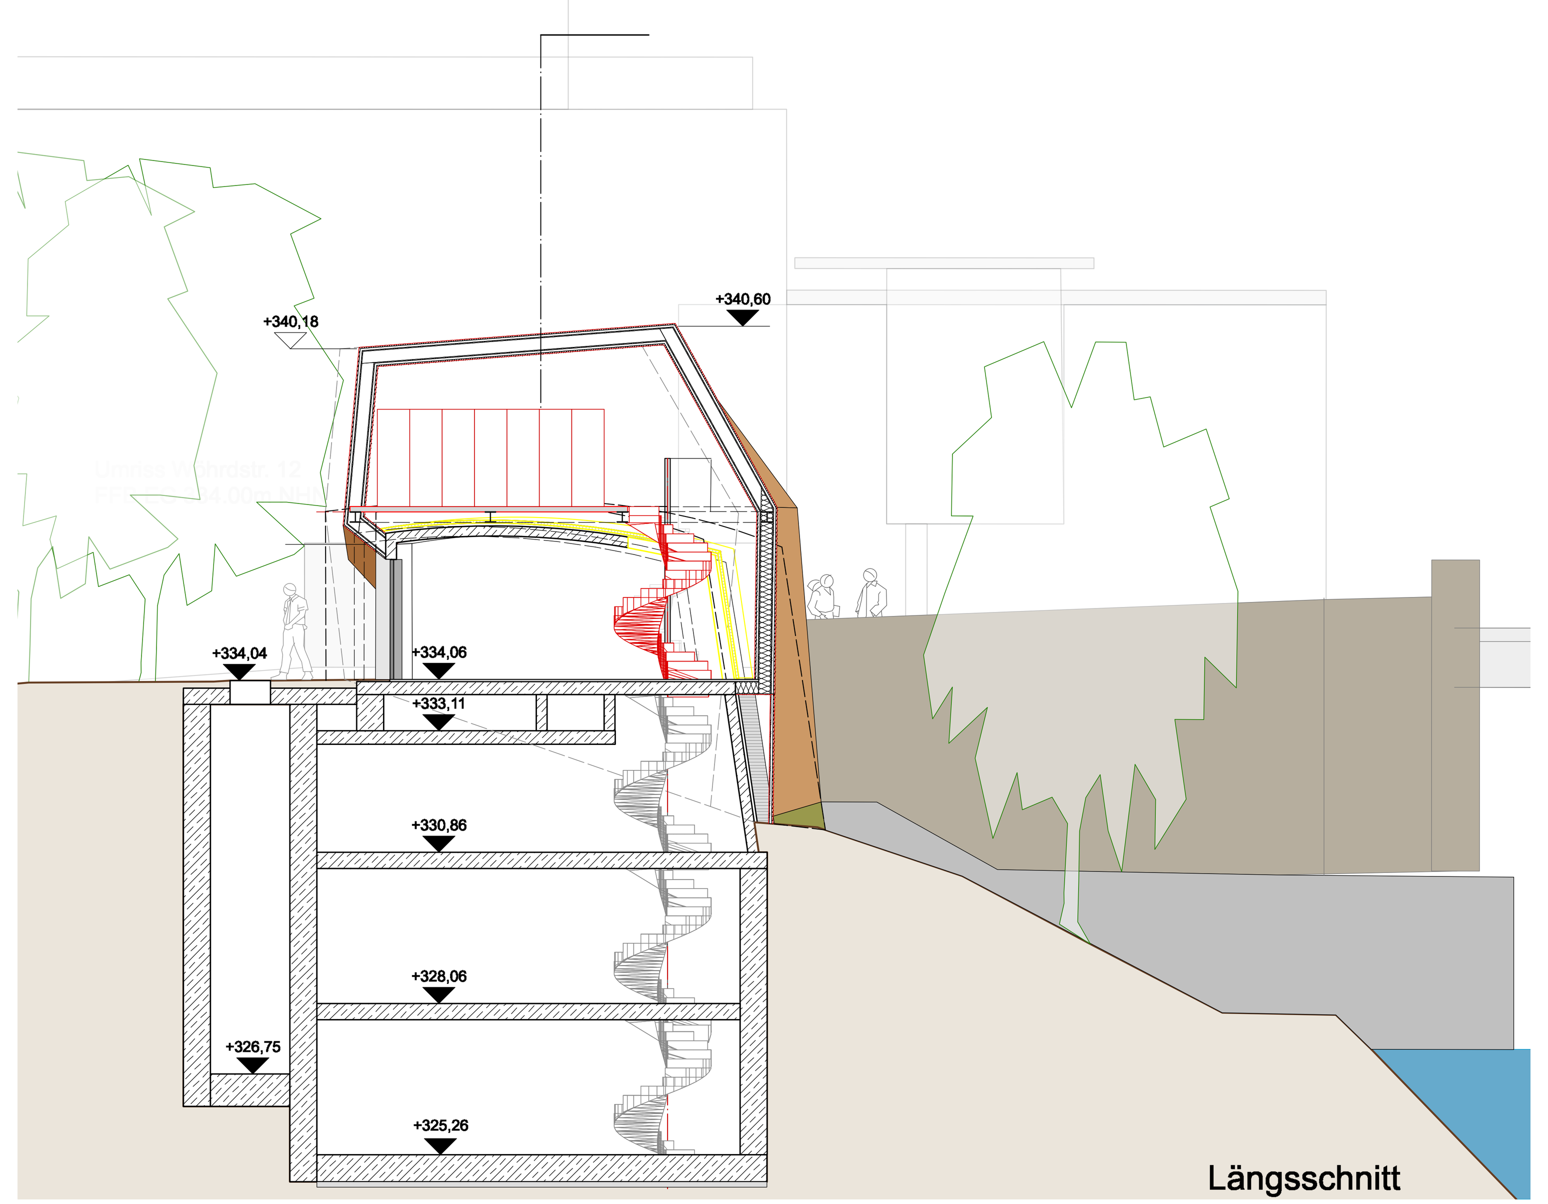

Längsschnitt

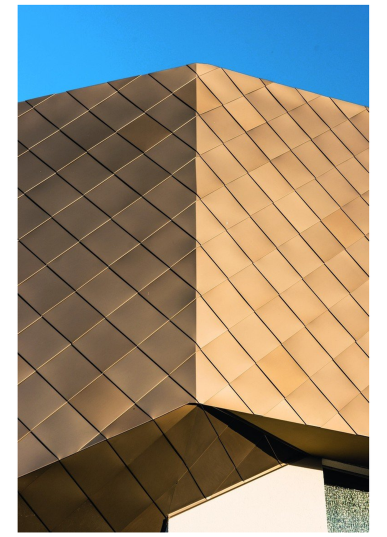

Referenz Fassadenverkleidung: gefalzte Blechschindeln (Kupfer/ Bronze oder eloxiert)

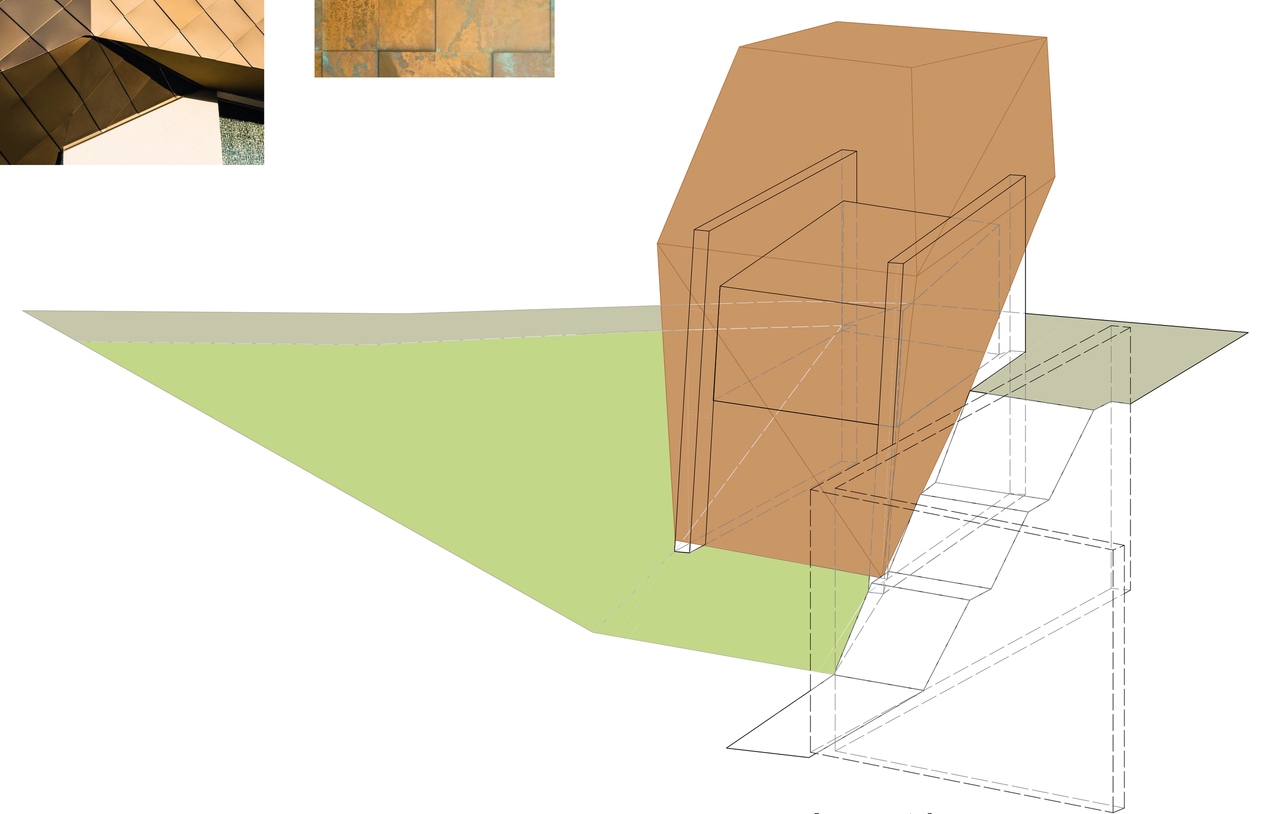

Isometrie

Vermerke Genehmigungsbehörde :

Wasserwirtschaftsamt Regensburg

STADT REGENSBURG

Index	Bemerkung	geändert am	Name	geprüft am	Name
c					
b					
a					

Übersichtslageplan :

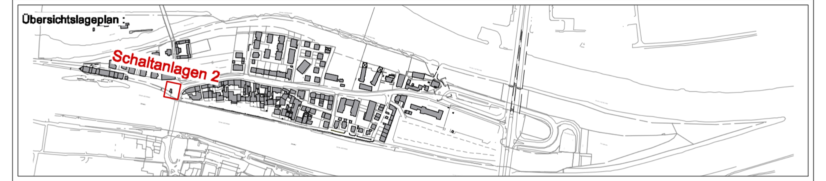

Vorhaben :	Hochwasserschutz Regensburg Abschnitt H Unterer Wöhrd PLANFESTSTELLUNG	Plan-Code : 36200-G-C 5	
		Anlage : C 5	Phase : G
Landkreis/ Stadt :	Regensburg	Plan-Nr. : RB-H-SAG 2-100	
Vorhabensträger :	Freistaat Bayern, Wasserwirtschaftsamt Landshuter Straße 59, 9053 Regensburg	Vorhabenskennzeichen: G1t 3620001015	
Maßstab : M 1:100	Planinhalt : Planabschnitt (PA) 5 Schaltanlagengebäude 2 zu SPW PA 4/ KPW PA 6, Wöhrdstr. 10b (RÜB 19)	Lagebezug: GK4 (EPSG 31468) Höhenbezug: Regensburger Höhennetz aus 1927 in m ü.NN (≠ DHHN12/ 92/ 2016 des LDBV)	
Planung :	Arbeitsgemeinschaft TEAM 3 schömigplan INGENIEURGESELLSCHAFT mbH archiscape architekten und landschaftsarchitekten tgmr. Landschafts architekten	entw. : 3/2024	team 3
		gez. : 4/2025	UB
		gepr. : 5/2025	WWA

30.04. 2025		26.05. 2025	
Datum	Unterschrift Entwurfsverfasser	Datum	Unterschrift Vorhabensträger