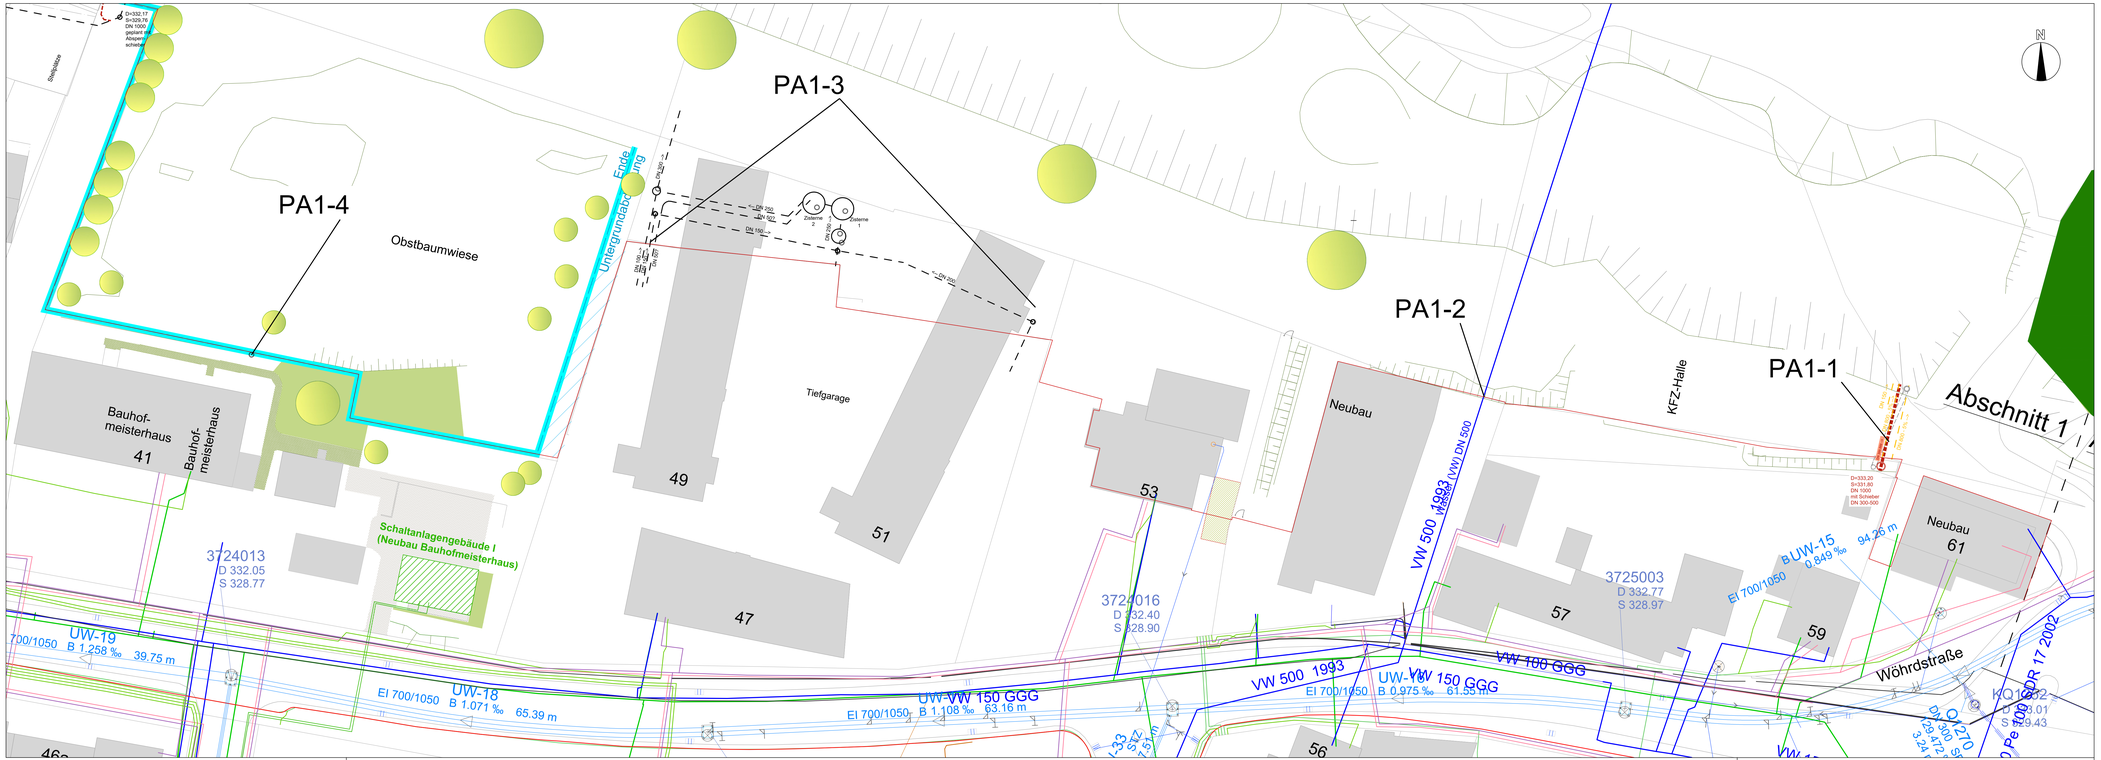

ZEICHENERKLÄRUNG

Planung

- Hochwasserschutzlinie
- Untergrundabdichtung (vertikal und horizontal)
- Kopfbalken
- Drainagerohr mit Schacht, teilweise mit Transportkanal
- Sickerwasser-/Kompaktpumpwerk mit Druckleitung
- Strom-/ Steuerleitungstrasse mit Schaltanlage
- Straßenablauf mit Muldenrinne
- Anschlussleitungen Straßenabläufe
- Regenwasserkanal für Oberflächenentwässerung
- Umlegung Abwasserkanal mit Anschlussleitung
- Umlegung Kanalhausanschlussleitung
- bestehender Abwasserkanal entfällt
- bestehende Kanalhausanschlussleitung entfällt
- bestehender Straßenablauf entfällt
- Vorschlag Trasse Umlegung Versorgungsleitung

Bestand

- Abwasserkanal
- Kanalhausanschlussleitungen
- Wasserleitung
- Gasleitung
- Stromkabel - Mittelspannung
- Stromkabel - Niederspannung
- Stromkabel - Hausanschluss Niederspannung
- Lichtwellenleiterkabel - Leerrohr
- Telekomkabel (graphisch entnommen)
- Kabel Deutschland (graphisch entnommen)
- Straßenbeleuchtung (graphisch entnommen)

Vermerke Genehmigungsbehörde :

Wasserwirtschaftsamt Regensburg

STADT REGENSBURG

Index	Bemerkung	geändert am:	Name:	gezeichnet am:	Name:
a					
b					
c					

Übersichtslageplan

Vorhaben:	Hochwasserschutz Regensburg Abschnitt H Unterer Wöhrd PLANFESTSTELLUNG	Plan-Code:	36200-E- C 8.1.1
		Anlage:	C 8.1.1 Phase: G
Landkreis/ Stadt:	Regensburg	Plan-Nr:	RB-H- PA1-O KLP 250
Vorhabenträger:	Freistaat Bayern, Wasserwirtschaftsamt Landshuter Straße 58, 9003 Regensburg	Vorhabenskennzeichen:	G1 362000101/0
Maßstab: 1:250	Planart: Planabschnitt (PA) 1 Lageplan Konflikte Sparten PA 1 - Ost	Lagebezug:	GK4 (DHDN 3-Meß)
		Höhenbezug:	Bezugshöhe (Höhenstatt) ana NN2 in ü.DNN (# DHHN12 für 2016 des LDBV)
Planung:	Arbeitsgemeinschaft TEAM 3 SCHWINGER INGENIEURGESELLSCHAFT MBH · BPOHIBGDBPE · tyrr landschaft architektur	erst.:	3/2024 team 3
		gez.:	3/2024 Nikolai, SP
		gepr.:	5/2025 WWA
30.04.2025 Datum	Unterschrift Entwurfsverfasser	26.05.2025 Datum	Unterschrift Vorhabenträger