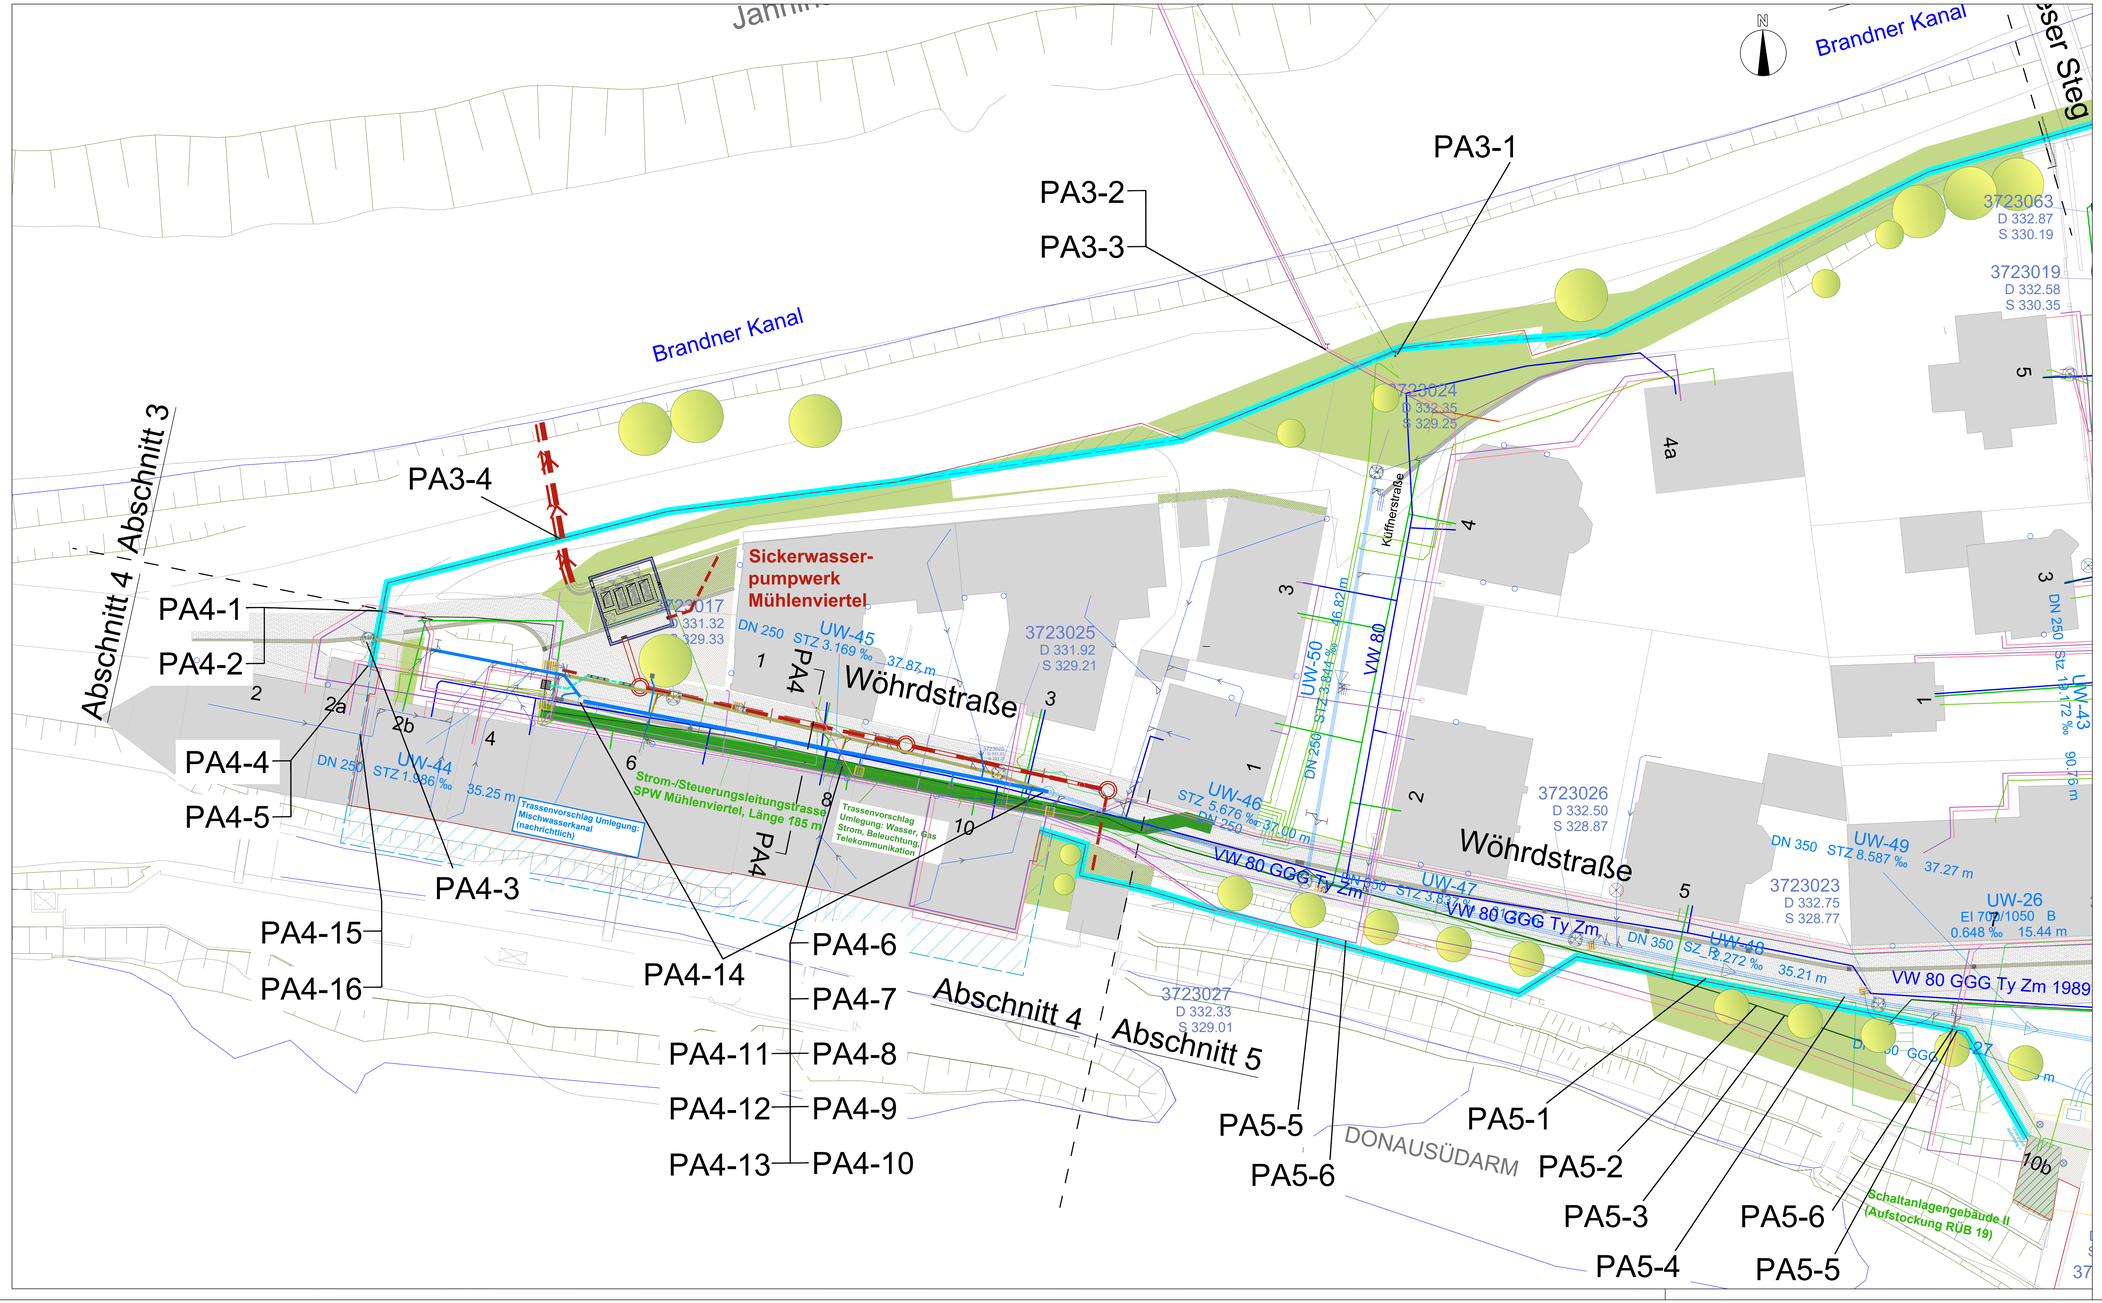


## ZEICHENERKLÄRUNG

### Planung

- Hochwasserschutzlinie
- Untergrundabdichtung (vertikal und horizontal)
- Kopfbalken
- Drainagerohr mit Schacht, teilweise mit Transportkanal
- Sickerwasser-Kompaktpumpwerk mit Druckleitung
- Strom-/ Steuerleitungstrasse mit Schaltanlage
- Straßenablauf mit Muldenrinne
- Anschlussleitungen Straßenabläufe
- Regenwasserkanal für Oberflächenentwässerung
- Ersatztrasse Abwasserkanal mit Anschlussleitung (nachrichtlich) Stadt plant Neuordnung der Entwässerung
- Umlegung Kanalhausanschlussleitung
- bestehender Abwasserkanal entfällt
- bestehende Kanalhausanschlussleitung entfällt
- bestehender Straßenablauf entfällt
- Vorschlag Trasse Umlegung Versorgungsleitung

### Bestand

- Abwasserkanal
- Kanalhausanschlussleitungen
- Wasserleitung
- Gasleitung
- Stromkabel - Mittelspannung
- Stromkabel - Niederspannung
- Stromkabel - Hausanschluss Niederspannung
- Lichtwellenleiterkabel - Leerrohr
- Telekomkabel (graphisch entnommen)
- Kabel Deutschland (graphisch entnommen)
- Straßenbeleuchtung (graphisch entnommen)

Vermerke Genehmigungsbehörde :

Wasserwirtschaftsamt Regensburg

STADT REGENSBURG

| Index | Bemerkung | geändert am | Name | geprüft am | Name |
|---|---|---|---|---|---|
| c | | | | | |
| b | | | | | |
| a | | | | | |

Übersichtsplan

| | | | |
|---|---|---|---|
| Vorhaben : | Hochwasserschutz Regensburg<br>Abschnitt H Unterer Wöhrd<br>PLANFESTSTELLUNG | Plan-Code : | 36200-E- C 8.3.1 |
| | | Anlage : C 8.3.1 | Phase : G |
| Landkreis/ Stadt : | Regensburg | Plan-Nr : | RB-H- PA3-5 KLP 250 |
| Vorhabenträger : | Freistaat Bayern, Wasserwirtschaftsamt<br>Landshuter Straße 59, 9053 Regensburg | Vorhabenskennzeichen : | G1: 3620001315 |
| Maßstab : 1:250 | Planinhalt : Planabschnitt (PA) 3-5<br>Lageplan Konflikte Sparten PA 3-5 | Lagebezug : | GK4 (EPSG 31468) |
| | | Höhenbezug : | Regensburger Höhennetz: aus 16DT.m in (LN4 v DHHN12 SO 2016 des LDBV) |
| Planung : | Arbeitsgemeinschaft TEAM 3 | erfst : 3/2024 | team 3 |
| | | gez. : 3/2024 | Nikolai, SP |
| | | gepr. : 5/2025 | WWA |
| 30.04.2025 | | 26.05.2025 | |
| Datum | Unterschrift Entwurfsverfasser | Datum | Unterschrift Vorhabenträger |