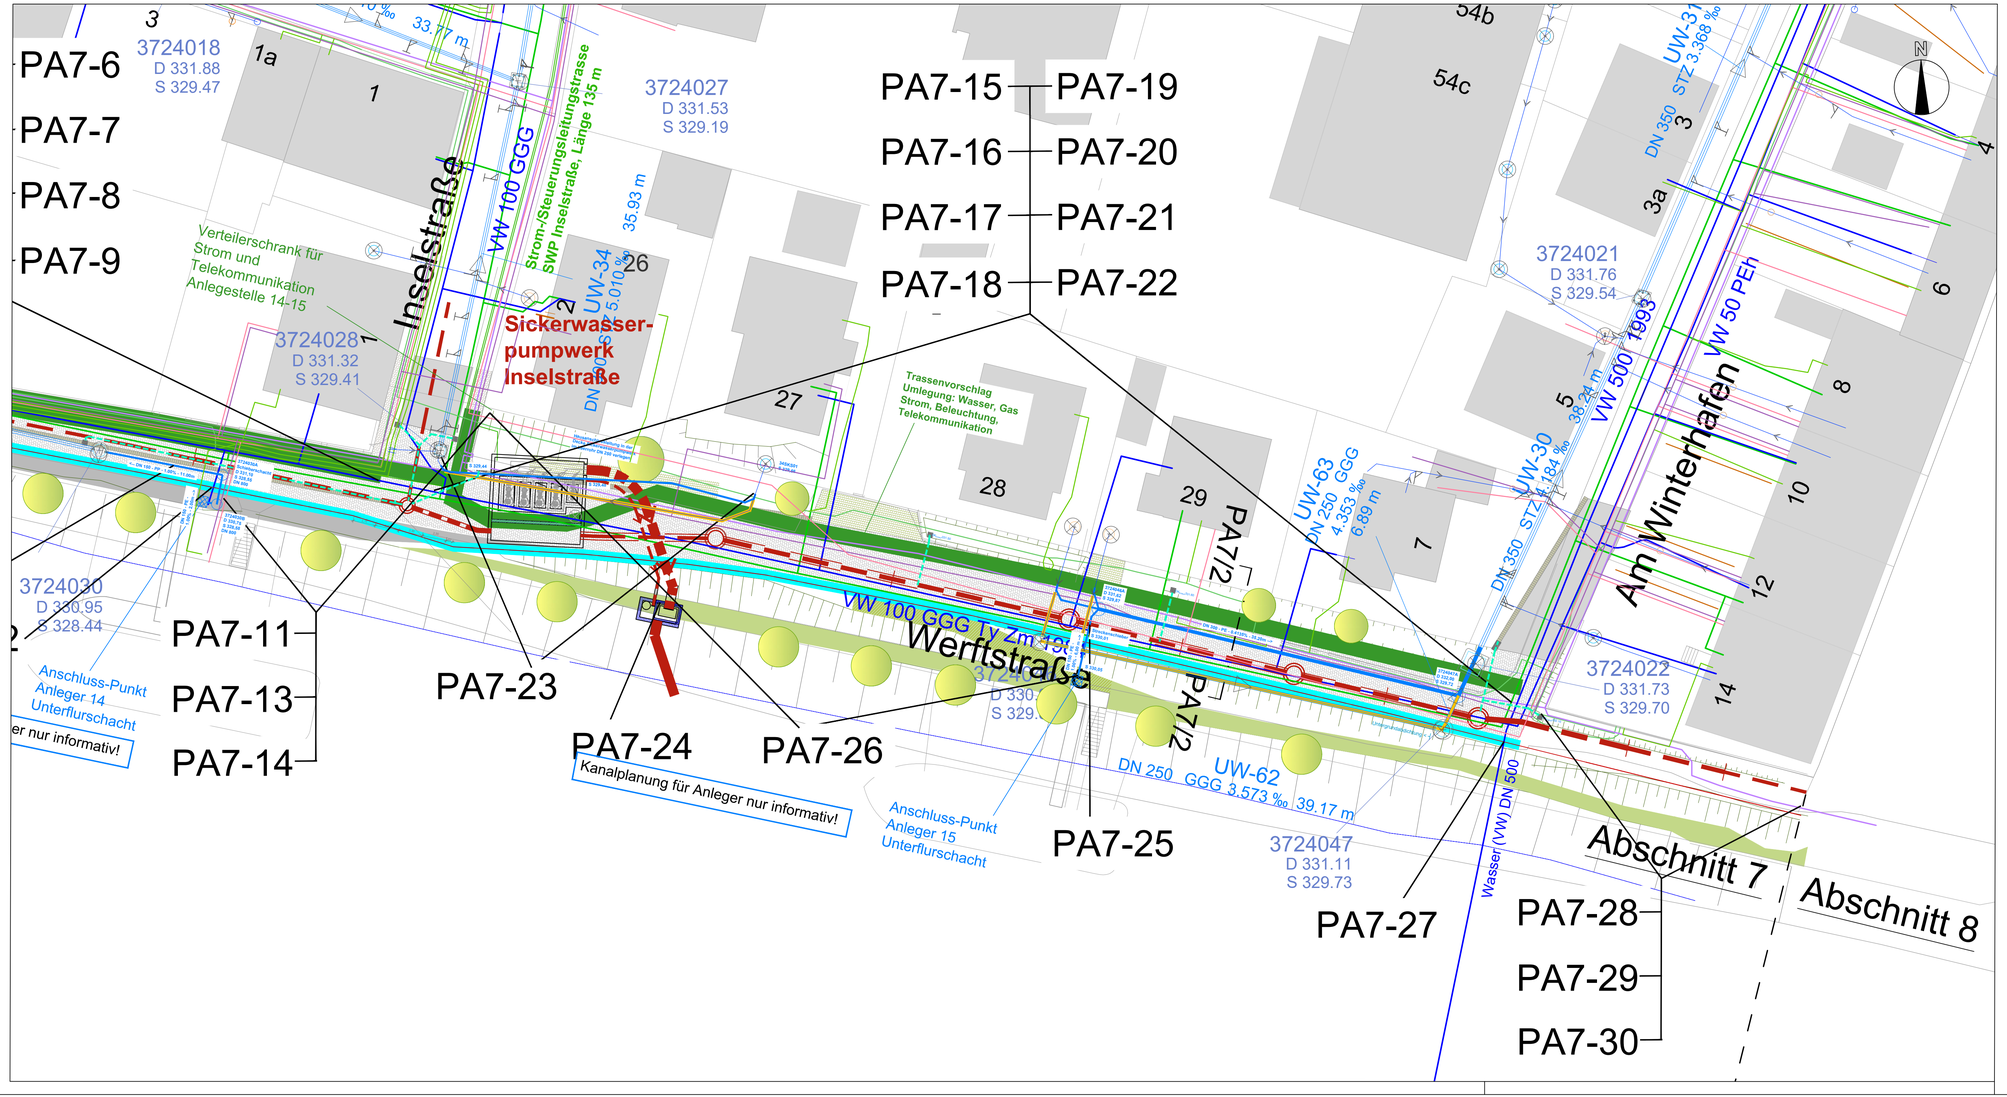

ZEICHENERKLÄRUNG

Planung

- Hochwasserschutzlinie
- Untergrundabdichtung (vertikal und horizontal)
- Kopfbalken
- Drainagerohr mit Schacht, teilweise mit Transportkanal
- Sickerwasser-/Kompaktpumpwerk mit Druckleitung
- Strom-/ Steuerleitungstrasse mit Schaltanlage
- Straßenablauf mit Muldenrinne
- Anschlussleitungen Straßenabläufe
- Regenwasserkanal für Oberflächenentwässerung
- Umlegung Abwasserkanal mit Anschlussleitung
- Umlegung Kanalhausanschlussleitung
- bestehender Abwasserkanal entfällt
- bestehende Kanalhausanschlussleitung entfällt
- bestehender Straßenablauf entfällt
- Vorschlag Trasse Umlegung Versorgungsleitung

Bestand

- Abwasserkanal
- Kanalhausanschlussleitungen
- Wasserleitung
- Gasleitung
- Stromkabel - Mittelspannung
- Stromkabel - Niederspannung
- Stromkabel - Hausanschluss Niederspannung
- Lichtwellenleiterkabel - Leerrohr
- Telekomkabel (graphisch entnommen)
- Kabel Deutchland (graphisch entnommen)
- Straßenbeleuchtung (graphisch entnommen)

Vermerke Genehmigungsbehörde :

Wasserwirtschaftsamt Regensburg

STADT REGENSBURG

Index	Bemerkung	geändert am	Name	geprüft am	Name
c					
b					
a					

Übersichtslageplan

Vorhaben :	Hochwasserschutz Regensburg Abschnitt H Unterer Wöhrd PLANFESTSTELLUNG	Plan-Code:	36200-E- C 8.5.1
		Anlage : C 8.5.1	Phase : G
Landkreis/ Stadt :	Regensburg	Plan-Nr. :	RB-H- PA7-O KLP 250
Vorhabensträger :	Freistaat Bayern, Wasserwirtschaftsamt Landshuter Straße 59, 9053 Regensburg	Vorhabenskennzeichen:	G1L3020001015
Maßstab : 1:250	Planinhalt : Planabschnitt (PA) 7 Lageplan Konflikte Sparten PA 7 - Ost	Lagebezug:	GK4 (EPSG:31468)
		Höhenbezug:	Regensburger Höhennetz aus 1927 in m ü.NN (# DHHN12/ 92/ 2016 des LDBV)
Planung :	Arbeitsgemeinschaft TEAM 3	erbr. :	3/2024 team 3
		gez. :	3/2024 Nikolai, SP
		gepr. :	5/2025 WWA
30.04.2025 Datum	Unterschrift Entwurfsverfasser	26.05.2025 Datum	Unterschrift Vorhabensträger