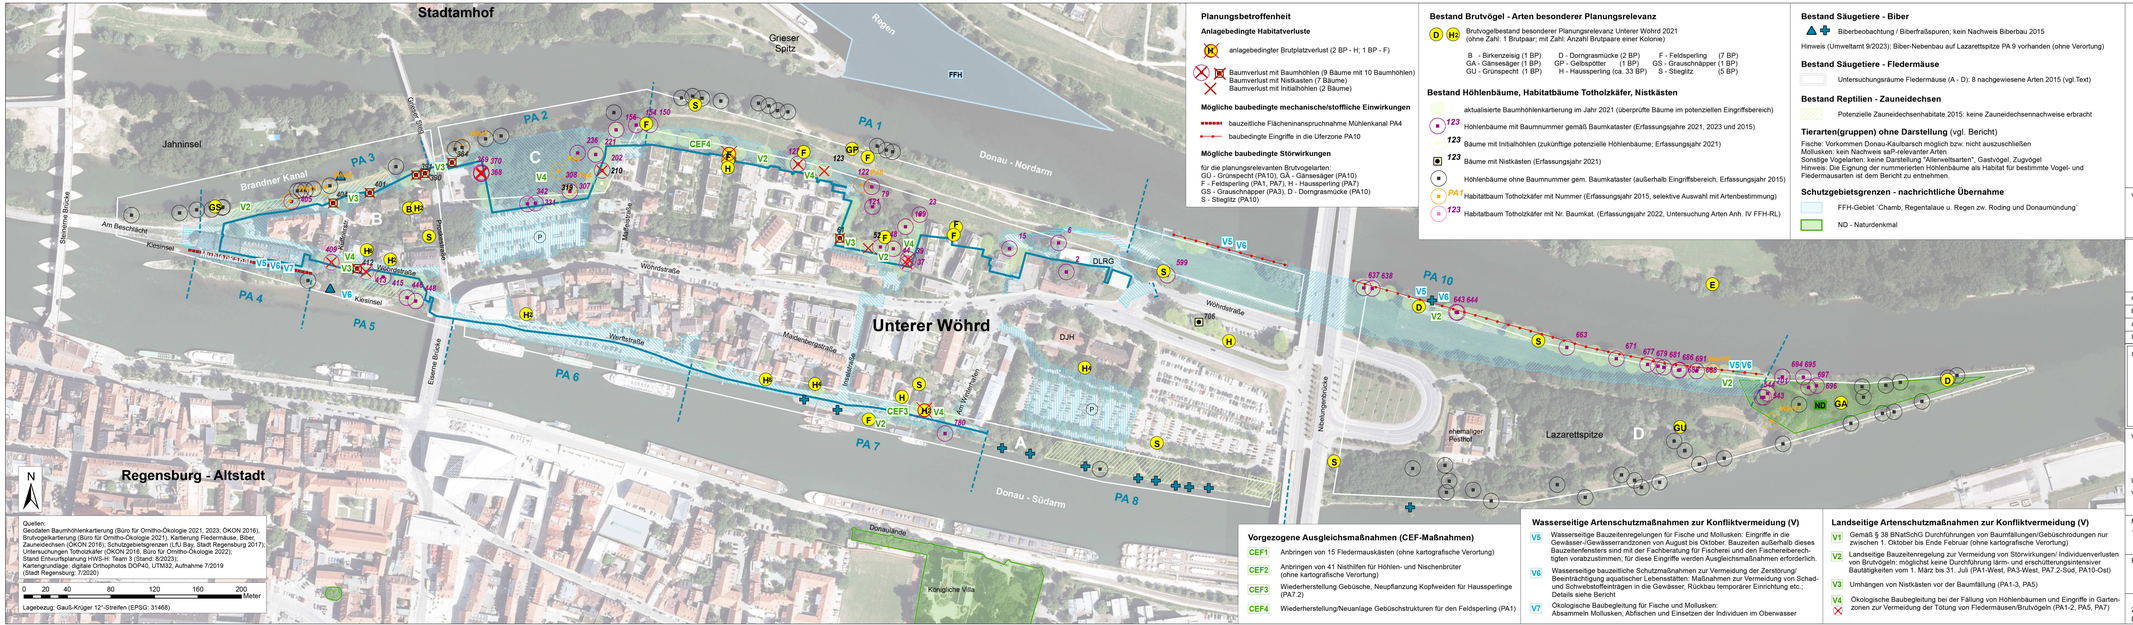

Quellen:
Geodaten Baumhöhlenkartierung (Büro für Ornitho-Ökologie 2021, 2023; ÖKON 2016), Brutvogelkartierung (Büro für Ornitho-Ökologie 2021), Kartierung Fledermäuse, Biber, Zauneidechsen (ÖKON 2016); Schutzgebietsgrenzen (LfU Bay. Stadt Regensburg 2017); Untersuchungen Totholzkäfer (ÖKON 2016, Büro für Ornitho-Ökologie 2022); Stand Entwurfsplanung HWS-H: Team 3 (Stand: 8/2023); Kartengrundlage: digitale Orthophotos DOP40, UTM32, Aufnahme 7/2019 (Stadt Regensburg: 7/2020)

Planungsbetroffenheit

Anlagebedingte Habitatverluste

- H – anlagebedingter Brutplatzverlust (2 BP - H; 1 BP - F)
- B – Baumverlust mit Baumhöhlen (9 Bäume mit 10 Baumhöhlen)
- Baumverlust mit Nistkasten (7 Bäume)
- H – Baumverlust mit Initialhöhlen (2 Bäume)

Mögliche baubedingte mechanische/stoffliche Einwirkungen

- bauzeitliche Flächeninanspruchnahme Mühlenkanal PA4
- baubedingte Eingriffe in die Uferzone PA10

Mögliche baubedingte Störwirkungen

für die planungsrelevanten Brutvogelarten:
GU - Grünspecht (PA10), GÄ - Gänsesäger (PA10)
F - Feldsperling (PA1, PA7), H - Haussperling (PA7)
GS - Grauschnäpper (PA3), D - Dorngrasmücke (PA10)
S - Stieglitz (PA10)

Bestand Brutvögel - Arten besonderer Planungsrelevanz

D H – Brutvogelbestand besonderer Planungsrelevanz Unterer Wöhrd 2021 (ohne Zahl: 1 Brutpaar; mit Zahl: Anzahl Brutpaare einer Kolonie)

B - Birkenzeisig (1 BP) D - Dorngrasmücke (2 BP) F - Feldsperling (7 BP)
GA - Gänsesäger (1 BP) GP - Gelbspötter (1 BP) GS - Grauschnäpper (1 BP)
GU - Grünspecht (1 BP) H - Haussperling (ca. 33 BP) S - Stieglitz (5 BP)

Bestand Höhlenbäume, Habitatbäume Totholzkäfer, Nistkästen

- aktualisierte Baumhöhlenkartierung im Jahr 2021 (überprüfte Bäume im potenziellen Eingriffsbereich)
- 123 – Höhlenbäume mit Baummummer gemäß Baumkataster (Erfassungsjahre 2021, 2023 und 2015)
- 123 – Bäume mit Initialhöhlen (zukünftige potenzielle Höhlenbäume; Erfassungsjahr 2021)
- 123 – Bäume mit Nistkästen (Erfassungsjahr 2021)
- Höhlenbäume ohne Baumnummer gem. Baumkataster (aufgrund Eingriffsbereich, Erfassungsjahr 2015)
- PA1 – Habitatbaum Totholzkäfer mit Nummer (Erfassungsjahr 2015, selektive Auswahl mit Artenbestimmung)
- 123 – Habitatbaum Totholzkäfer mit Nr. Baumkat. (Erfassungsjahr 2022, Untersuchung Arten Anh. IV FFH-RL)

Bestand Säugetiere - Biber

Biberbeobachtung / Biberfraßspuren; kein Nachweis Biberbau 2015

Hinweis (Umweltamt 9/2023): Biber-Nebenbau auf Lazarettspitze PA 9 vorhanden (ohne Verortung)

Bestand Säugetiere - Fledermäuse

Untersuchungsräume Fledermäuse (A - D): 8 nachgewiesene Arten 2015 (vgl.Text)

Bestand Reptilien - Zauneidechsen

Potenzielle Zauneidechsenhabitate 2015: keine Zauneidechsennachweise erbracht

Tierarten(gruppen) ohne Darstellung (vgl. Bericht)

Fische: Vorkommen Donau-Kaulbarsch möglich bzw. nicht auszuschließen
Mollusken: kein Nachweis saP-relevanter Arten
Sonstige Vogelarten: keine Darstellung "Allerweltsarten", Gastvögel, Zugvögel
Hinweis: Die Eignung der nummerierten Höhlenbäume als Habitat für bestimmte Vogel- und Fledermausarten ist dem Bericht zu entnehmen.

Schutzgebietsgrenzen - nachrichtliche Übernahme

- FFH-Gebiet ´Chamb, Regentalaue u. Regen zw. Roding und Donaumündung´
- ND - Naturdenkmal

Vorgezogene Ausgleichsmaßnahmen (CEF-Maßnahmen)

- CEF1 – Anbringen von 15 Fledermauskästen (ohne kartografische Verortung)
- CEF2 – Anbringen von 41 Nisthilfen für Höhlen- und Nischenbrüter (ohne kartografische Verortung)
- CEF3 – Wiederherstellung Gebüsche, Neupflanzung Kopfweiden für Haussperlinge (PA7.2)
- CEF4 – Wiederherstellung/Neuanlage Gebüschstrukturen für den Feldsperling (PA1)

Wasserseitige Artenschutzmaßnahmen zur Konfliktvermeidung (V)

- V5 – Wasserseitige Bauzeitenregelungen für Fische und Mollusken: Eingriffe in die Gewässer-/Gewässerrandzonen von August bis Oktober. Bauzeiten außerhalb dieses Bauzeitenfensters sind mit der Fachberatung für Fischerei und den Fischereiberechtigten vorabzustimmen; für diese Eingriffe werden Ausgleichsmaßnahmen erforderlich.
- V6 – Wasserseitige bauzeitliche Schutzmaßnahmen zur Vermeidung der Zerstörung/Beeinträchtigung aquatischer Lebensstätten: Maßnahmen zur Vermeidung von Schad- und Schwebstoffeinträgen in die Gewässer, Rückbau temporärer Einrichtung etc.; Details siehe Bericht
- V7 – Ökologische Baubegleitung für Fische und Mollusken: Absammeln Mollusken, Abfischen und Einsetzen der Individuen im Oberwasser

Landseitige Artenschutzmaßnahmen zur Konfliktvermeidung (V)

- V1 – Gemäß § 38 BNatSchG Durchführungen von Baumfällungen/Gebüschrodungen nur zwischen 1. Oktober bis Ende Februar (ohne kartografische Verortung)
- V2 – Landseitige Bauzeitenregelung zur Vermeidung von Störwirkungen/ Individuenverlusten von Brutvögeln: möglichst keine Durchführung lärm- und erschütterungsintensiver Bautätigkeiten vom 1. März bis 31. Juli (PA1-West, PA3-West, PA7.2-Süd, PA10-Ost)
- V3 – Umhängen von Nistkästen vor der Baumfällung (PA1-3, PA5)
- V4 – Ökologische Baubegleitung bei der Fällung von Höhlenbäumen und Eingriffe in Gartenzonen zur Vermeidung der Tötung von Fledermäusen/Brutvögeln (PA1-2, PA5, PA7)

Vorhaben

- Hochwasserschutz-Abschnitte (PA 1 - 10)
- Geplante Hochwasser-Schutzlinie Unterer Wöhrd (ca. 2 km)

Vorhabensbereich (ca. 6,87 ha)

- Hochwasserschutz-Maßnahmen (ca. 3,74 ha)
- Maßnahmen "Auenmodellierung" (ca. 2,16 ha)
- Baustelleneinrichtungsflächen (ca. 0,9 ha)
- Gesonderte Baustellenzufahrten (ca. 0,07 ha)

Quelle: Hochwasserschutz Regensburg, Abschnitt H Unterer Wöhrd, Entwurfsplanung (Team 3, März 2024)

Vermerke Genehmigungsbehörde:

Wasserwirtschaftsamt Regensburg

STADT REGENSBURG

Index	Bemerkung	geändert am	Name	geprüft am	Name
c					
b					
a					

Übersichtslageplan

Vorhaben:	**Hochwasserschutz Regensburg / Abschnitt H Unterer Wöhrd** UMWELTPLANUNG	Plan-Code:	36200-E-D 3.1
		Anlage: D 3.1	Phase: E
Landkreis/Stadt:	Regensburg	Plan-Nr.:	HWS-H_D3.1_saP_Plan
Vorhabensträger:	Freistaat Bayern, Wasserwirtschaftsamt Landshuter Straße 59, 93053 Regensburg	Vorhabenskennzeichen:	G11.3620001015
Maßstab: 1:2.000	Planinhalt: **Spezielle artenschutzrechtliche Prüfung (saP)** Bestand/Betroffenheit planungsrelevanter Arten Artenschutzmaßnahmen	Lagebezug:	GK4 (EPSG 31468)
		Höhenbezug:	Regensburger Höhennetz aus 1927 m n ü. NN (≈ DHHN 12/ 92/ 2016 des LDBV)
Planung:	Arbeitsgemeinschaft TEAM 3	enhc.:	3/2024 bgmr/Hain
		gez.:	3/2024 bgmr/Hain
28.03.2024 Datum	Unterschrift Entwurfsverfasser	26.05.2025 Datum	gepr.: 3/2024 bgmr/Becker Unterschrift Vorhabensträger