


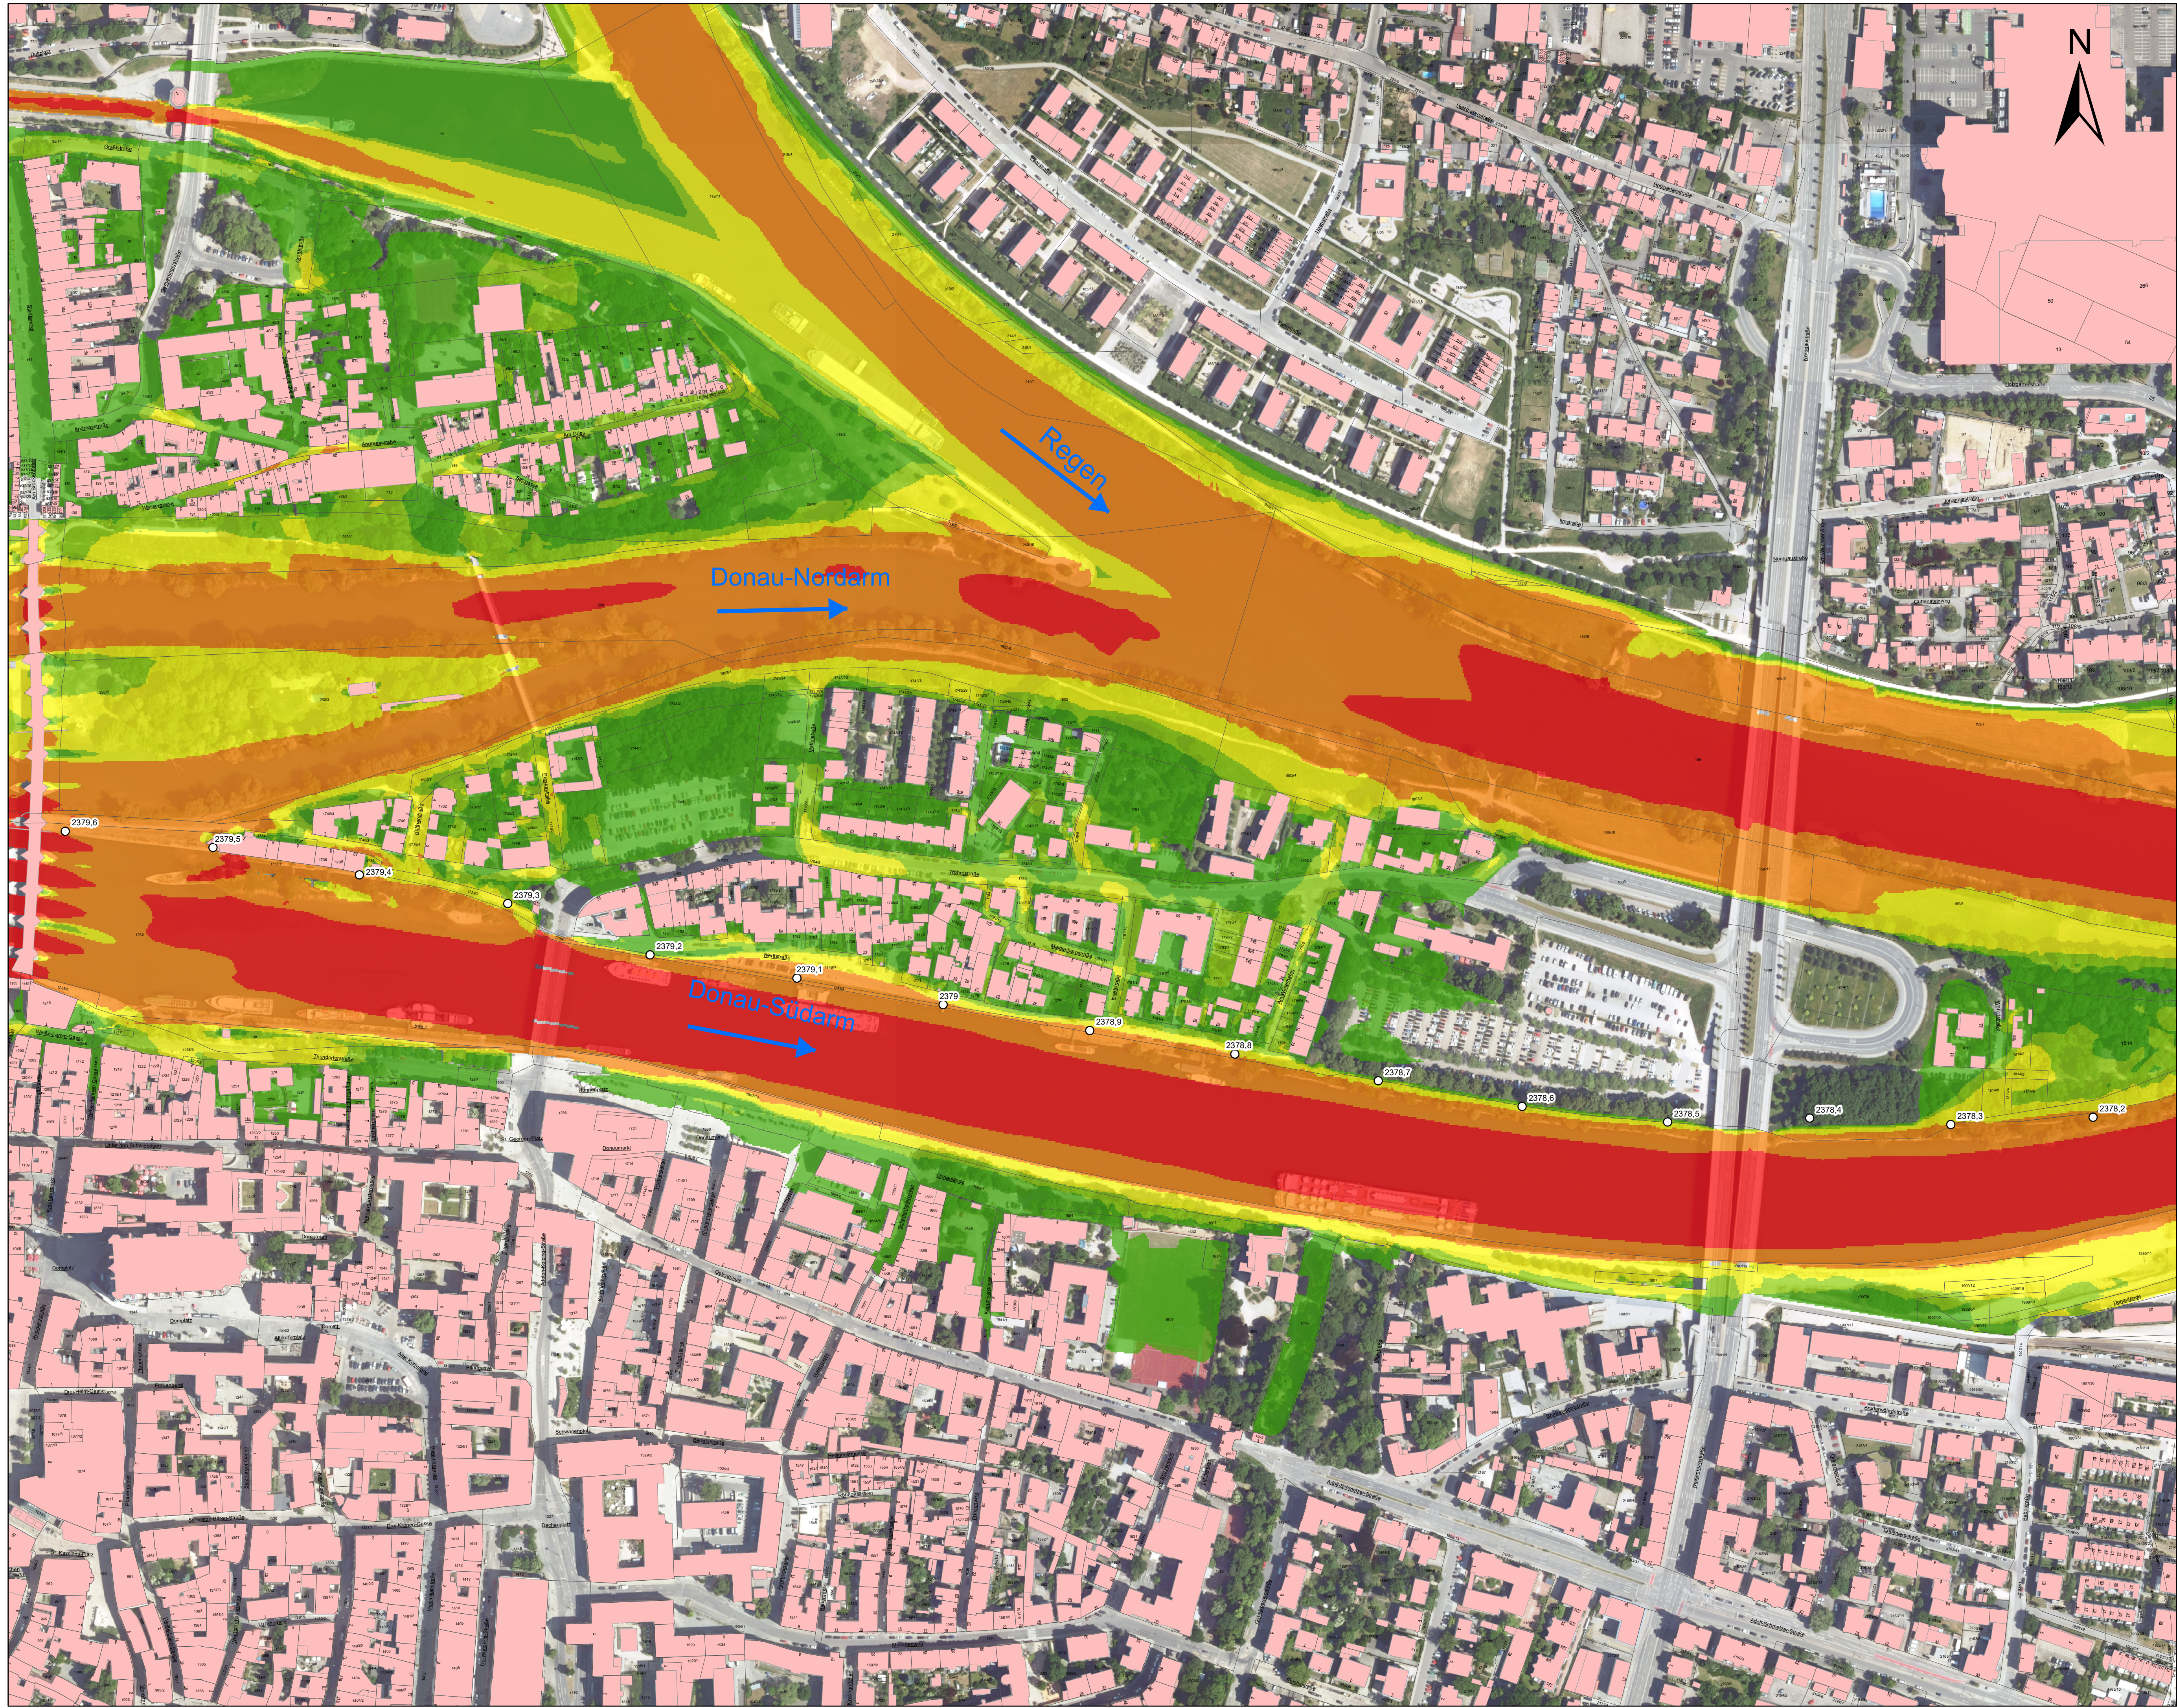


Zeichenerklärung:
Ergebnisse hydraulische Wasserspiegellagenberechnung
Wasserspiegel 1: HQ₁₀₀ Donau stationär; Q_{Donau} = 3.000 m³/s; Q_{Regen} = 400 m³/s
Wasserspiegel 2: HQ₁₀₀ Regen stationär; Q_{Donau} = 2.650 m³/s; Q_{Regen} = 750 m³/s
dargestellt ist der maximale der beiden Wasserspiegel je Knoten
(Stand September 2024)

berechnete max. Fließgeschwindigkeiten [m/s]

- HQ₁₀₀ Istzustand
- < 0,30
 - 0,30 - 0,50
 - 0,50 - 1,00
 - 1,00 - 2,00
 - > 2,00

2378.1
O Flusskilometer Donau

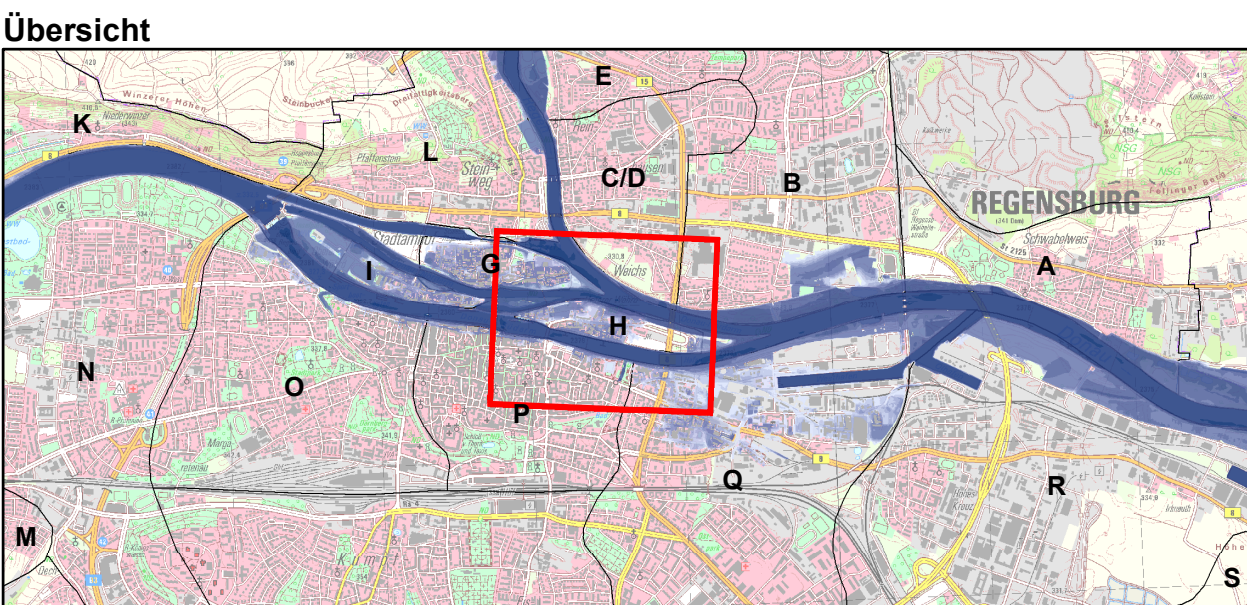

0 100 200 300 m



BCI
BJÖRNSEN BERATENDE INGENIEURE

Vorhaben:	Hochwasserschutz Regensburg Abschnitt H - Unterer Wöhrd Hydraulik	Anlage:	F-3.1.2
Vorhabensträger:	Freistaat Bayern	Plan-Nr.:	3.1.2
Landkreis:	Regensburg	Schutzvermerk/Dateiname:	F_3_1_2_HQ100_Ist_Velocity.mxd
Vorhabenskennzeichen (BAYIS):		entw.	Sept. 2024 Koy
Maßstab:	Istzustand HQ ₁₀₀ max. Fließgeschwindigkeiten	gez.	Sept. 2024 Weidinger
1 : 2.000		gepr.	Sept. 2024 Weise
Entwurfsverfasser:	BJörnSEN Beratende Ingenieure GmbH, Niederlassung Augsburg Monsieustr. 33, 86150 Augsburg Telefon Nr.: 0821/3194908-0, Fax Nr.: 0821/3194908-17		

Sept. 2024 ppa. Sept. 2024
Datum Dipl.-Ing. (FH) Sebastian Weise Datum Bauberrat R. Zimmermann
Geobasisdaten: © Bayerische Vermessungsverwaltung (Darstellung der Flurkarte als Eigentumsnachweis nicht geeignet)