


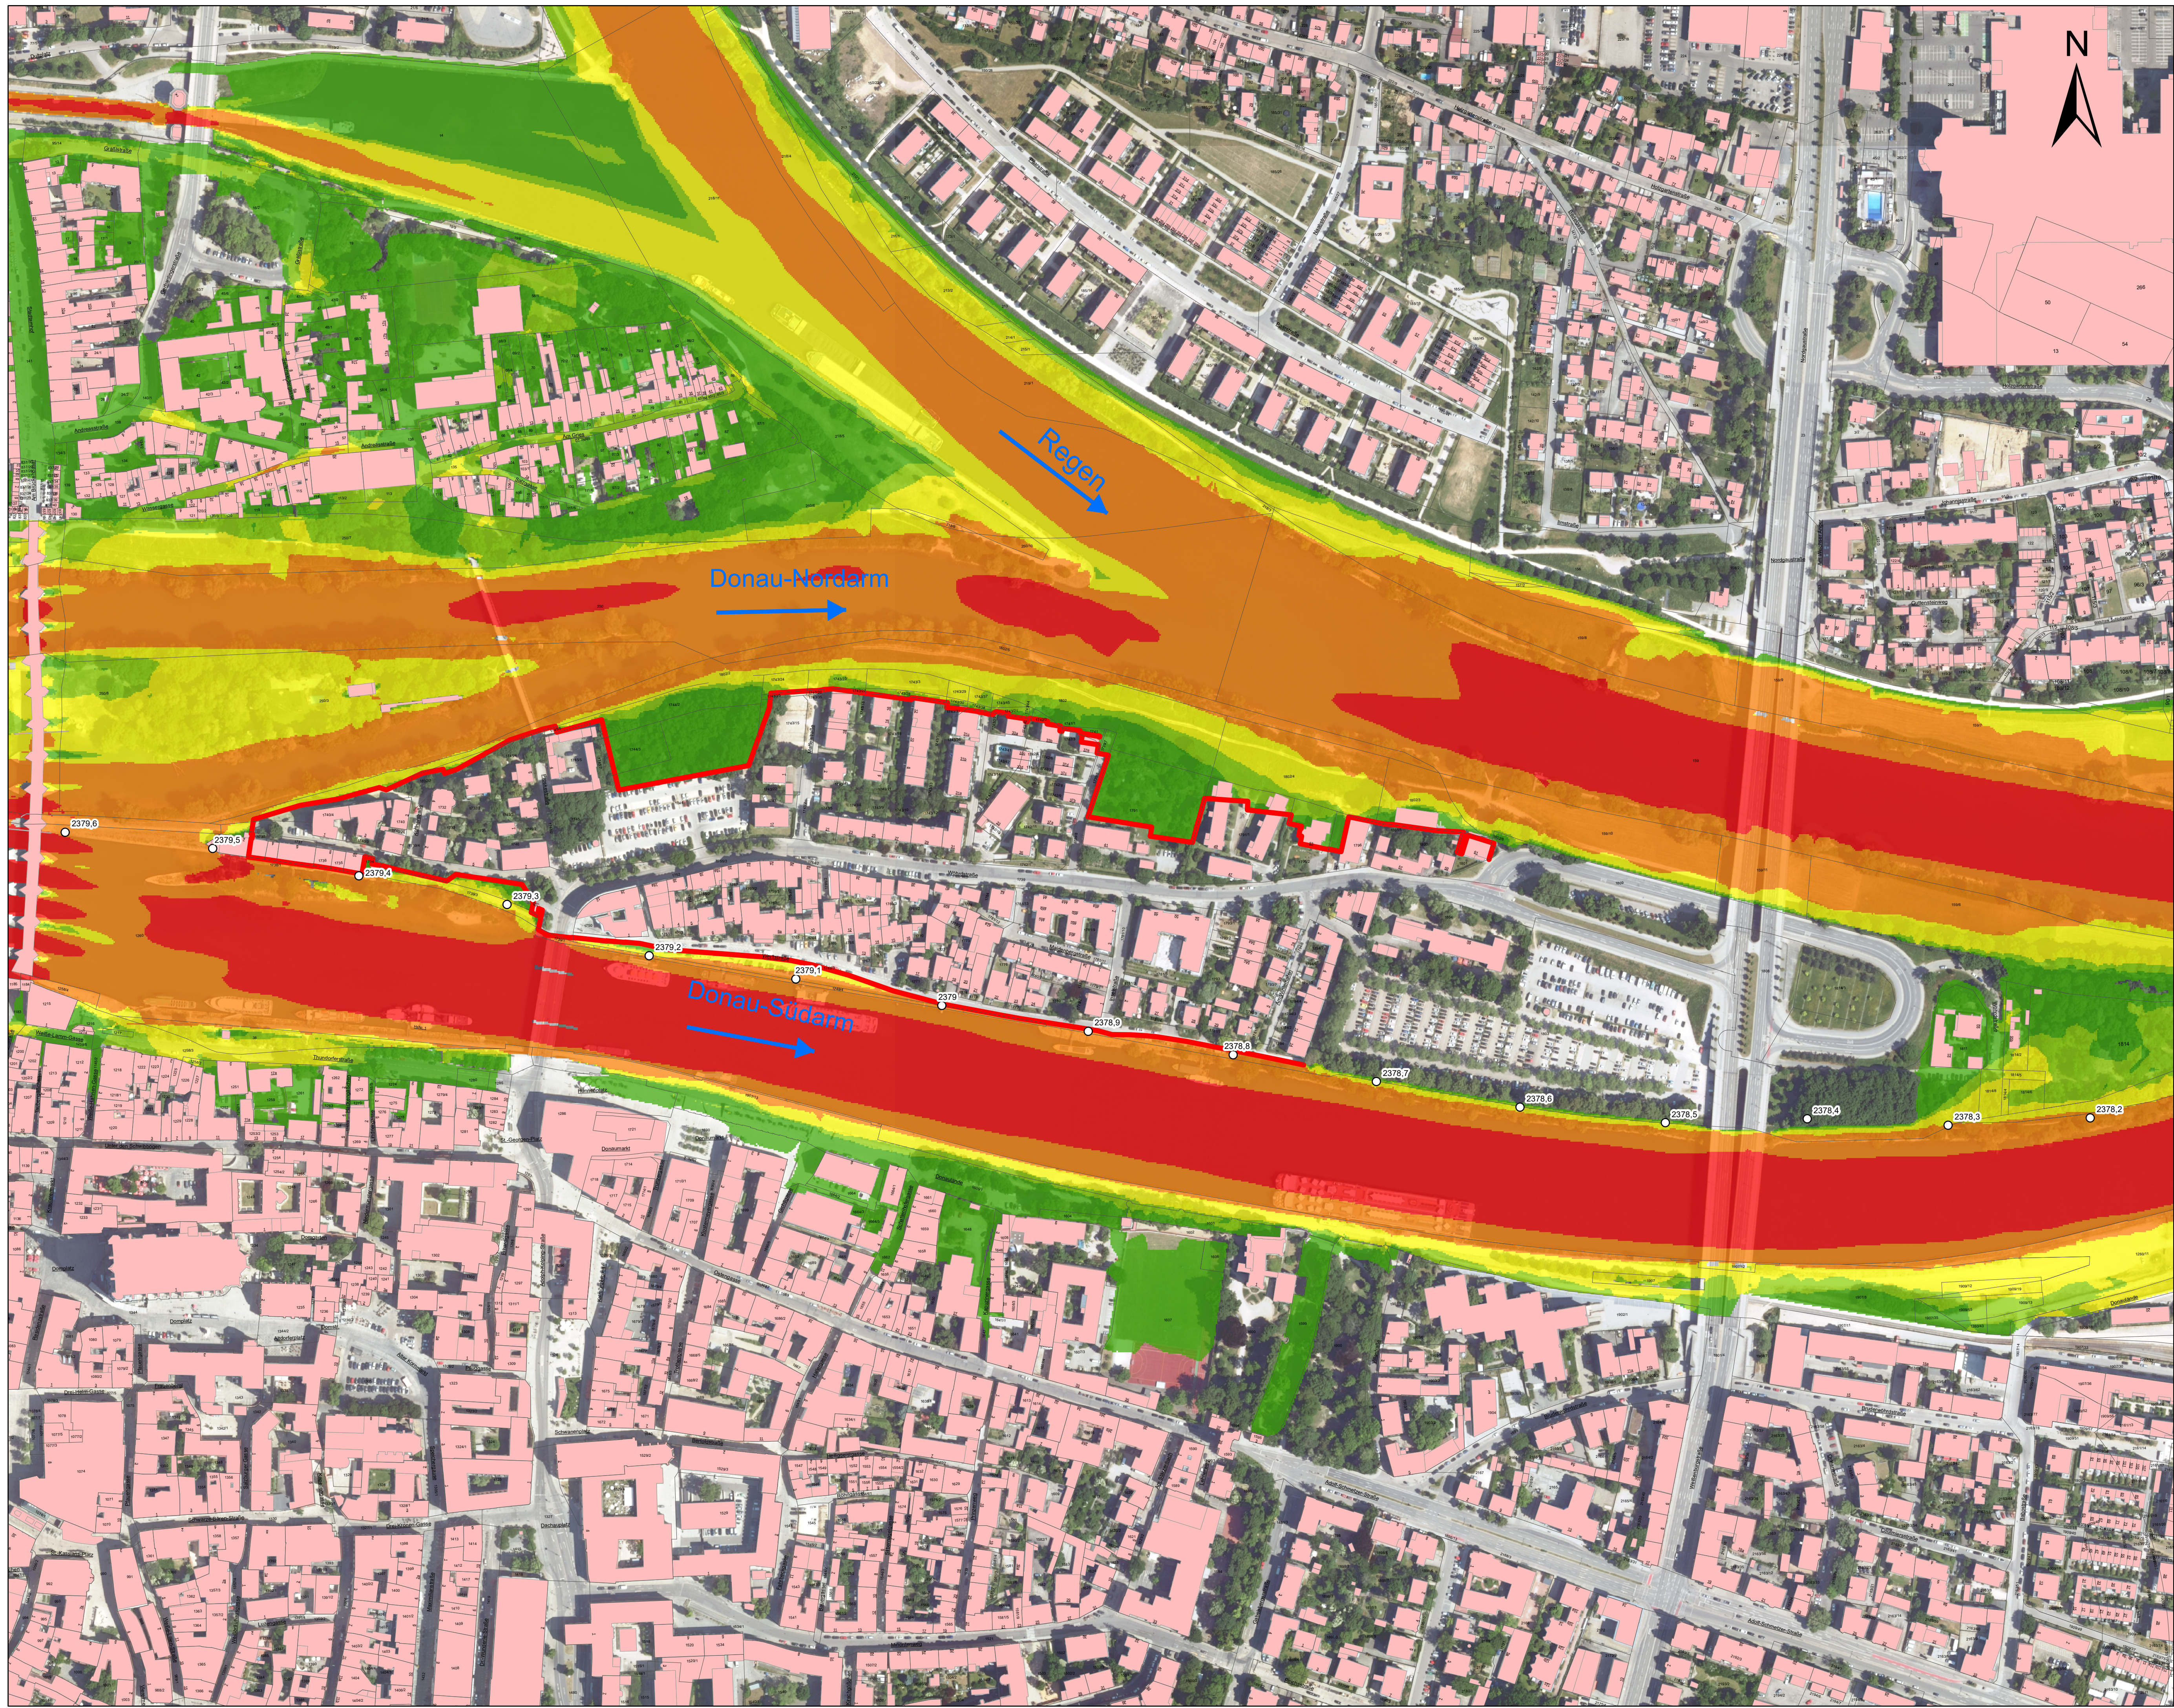

Zeichenerklärung:
Ergebnisse hydraulische Wasserspiegellagenberechnung
Wasserspiegel 1: HQ₁₀₀ Donau stationär; Q_{Donau} = 3.000 m³/s; Q_{Regen} = 400 m³/s
Wasserspiegel 2: HQ₁₀₀ Regen stationär; Q_{Donau} = 2.650 m³/s; Q_{Regen} = 750 m³/s
dargestellt ist der maximale der beiden Wasserspiegel je Knoten
(Stand September 2024)

berechnete max. Fließgeschwindigkeiten [m/s]

HQ₁₀₀ Planzustand

- < 0,30
- 0,30 - 0,50
- 0,50 - 1,00
- 1,00 - 2,00
- > 2,00



Hochwasserschutz (geplant)

HWS Trasse

Sonstiges

2378,1
O Flusskilometer Donau

Übersicht

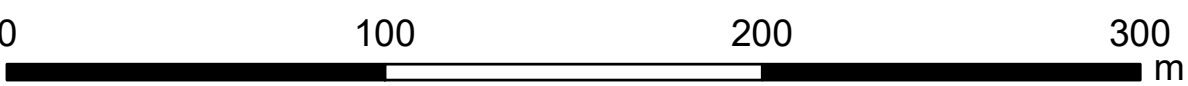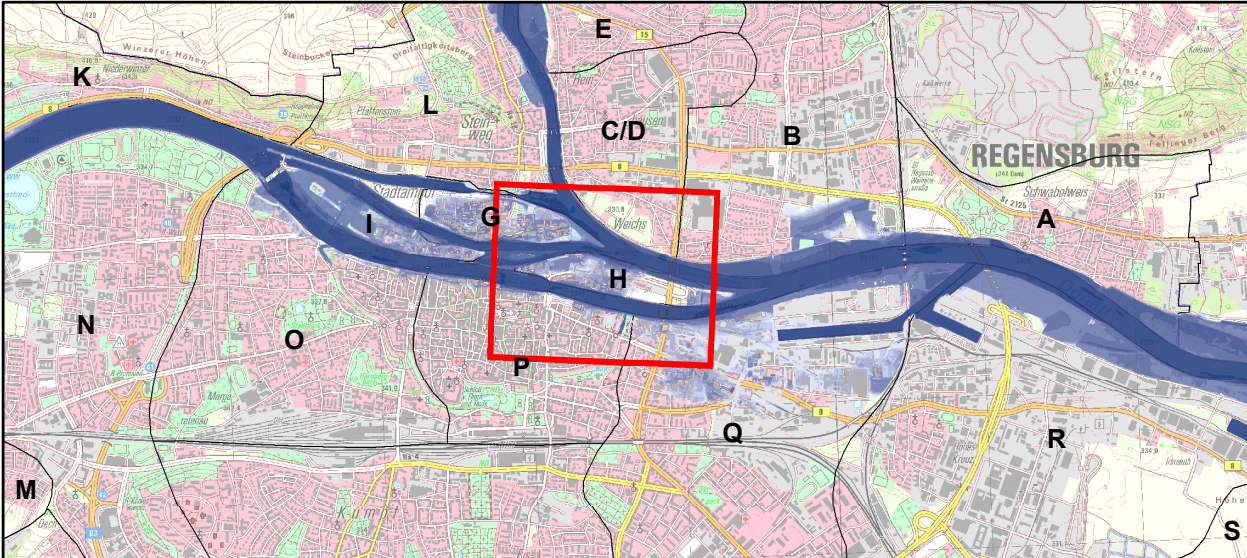

Vorhaben:	Hochwasserschutz Regensburg Abschnitt H - Unterer Wöhrd Hydraulik	Anlage:	F-3.1.4
Vorhabenträger:	Freistaat Bayern	Plan-Nr.:	3.1.4
Landkreis:	Regensburg	Schutzvermerk/Dateiname:	F_3_1_4_HQ100_Pla_Velocity.mxd
Stadt:	Regensburg	Maßstab:	1 : 2.000
Vorhabenskennzeichen (BAYIS):		entw.	Sept. 2024
		gez.	Sept. 2024
		gepr.	Sept. 2024
Entwurfsverfasser:	BJörnsen Beratende Ingenieure GmbH, Niederlassung Augsburg Monsieustr. 33, 86159 Augsburg Telefon Nr.: 0821/3194908-0, Fax Nr.: 0821/3194908-17	Koy	Weidinger
		Weise	

Sept. 2024 ppa. Sept. 2024
Datum Dipl.-Ing. (FH) Sebastian Weise Datum Bauberrat R. Zimmermann
Geobasisdaten: © Bayerische Vermessungsverwaltung (Darstellung der Flurkarte als Eigentumsnachweis nicht geeignet)