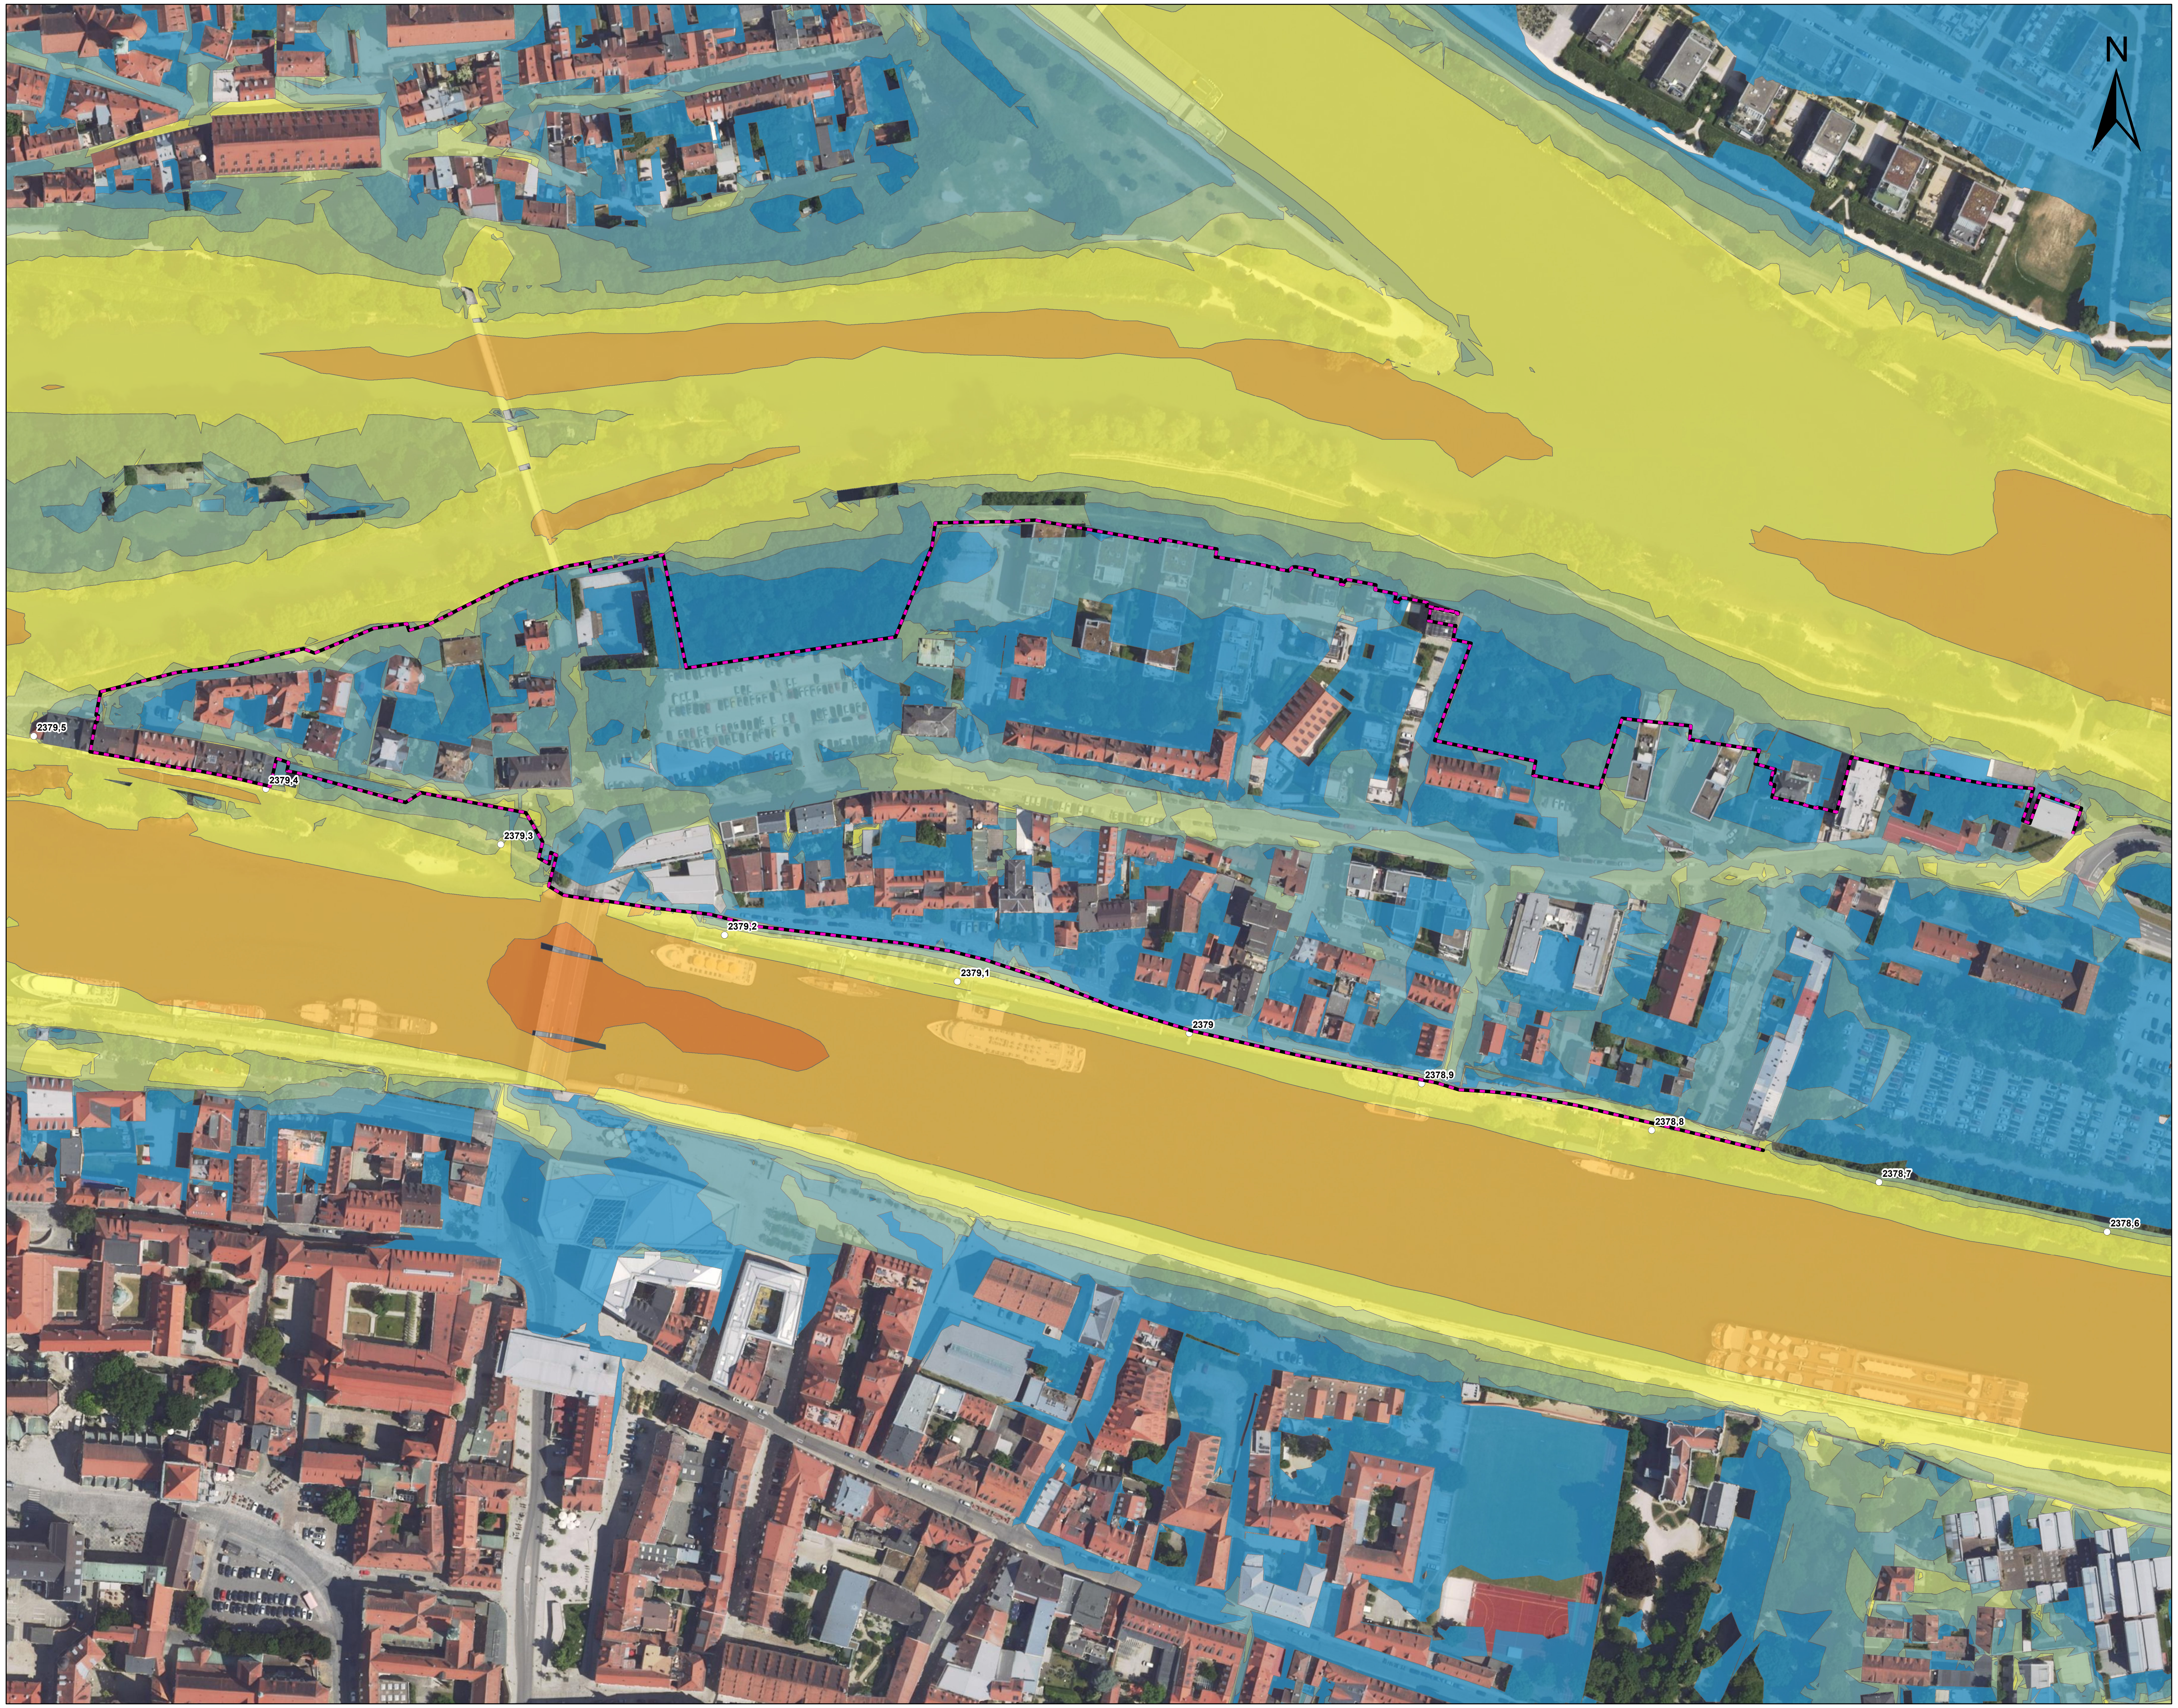

Zeichenerklärung

9+600 Flußkilometer Donau

Flurstücke

HWS Trasse (Stand 02/2024)

max. Fließgeschwindigkeiten [m/s]
Planzustand HQextrem instationär

- 0.010 - 0.250
- 0.250 - 0.500
- 0.500 - 0.750
- 0.750 - 1.000
- 1.000 - 2.000
- 2.000 - 3.000
- 3.000 - 5.000
- 5.000 - 10.000
- > 10.000

Übersicht

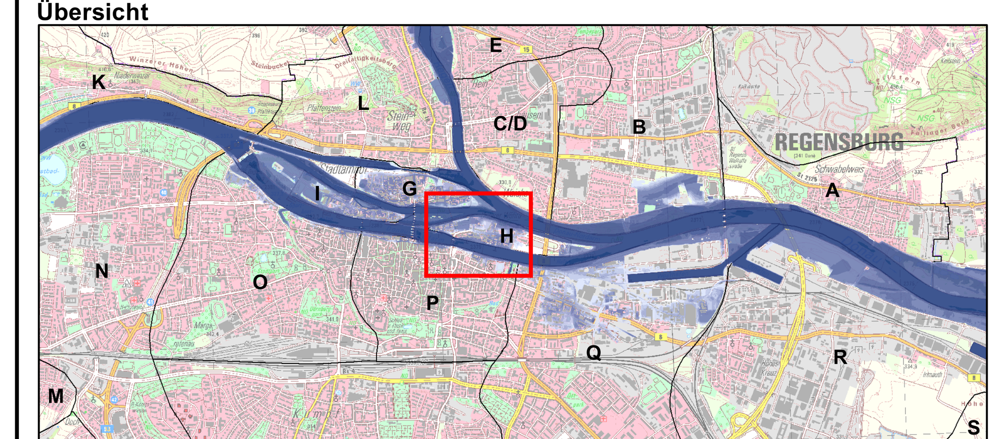

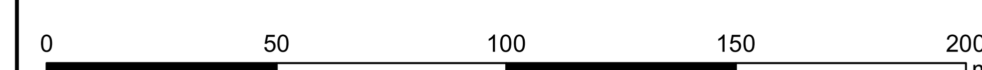

STADT REGENSBURG

Wasserwirtschaftsamt Regensburg

BJÖRNSEN BERATENDE INGENIEURE

Index	Bemerkung	geänd. am	Name	gepr. am	Name
c					
b					
a					

Vorhaben: Hochwasserschutz Regensburg
Abschnitt H - unterer Wöhrd
- Hydraulik -

Anlage: **F- 3.4.3**

Vorhabensträger: Freistaat Bayern

Plan-Nr.: **3.4.3**

Landkreis:

Stadt: Regensburg

Schutzvermerk/Dateiname: Veloc_HQext.mxd

Vorhabenskennzeichen (BAYIFS):

Maßstab: 1:1.250

Planzustand HQextrem
max. Fließgeschwindigkeiten

entw.	Mai 2019	Koy
gez.	Mai 2019	Seybold
gepr.	Mai 2019	Reichel

Entwurfsverfasser: Björnsen Beratende Ingenieure GmbH, Niederlassung Augsburg
Morellstraße 33, 86159 Augsburg
Telefon Nr.: 0821/3194908-0, Fax Nr.: 0821/3194908-17

Mai 2019 — Datum — gez. Dipl.-Ing. Architekt M. Bjørnsen

Mai 2019 — Datum — gez. G. Strobl

Geobasisdaten: © Bayerische Vermessungsverwaltung (Darstellung der Flurkarte als Eigentumsnachweis nicht geeignet)

24.02.2025 10:03:32 Uhr, M 1:1250, koy
K:\yrh1807836\04_Pl\10_GIS\02_mxd\work\Veloc_HQext.mxd, 93,0cm x 58,4cm