


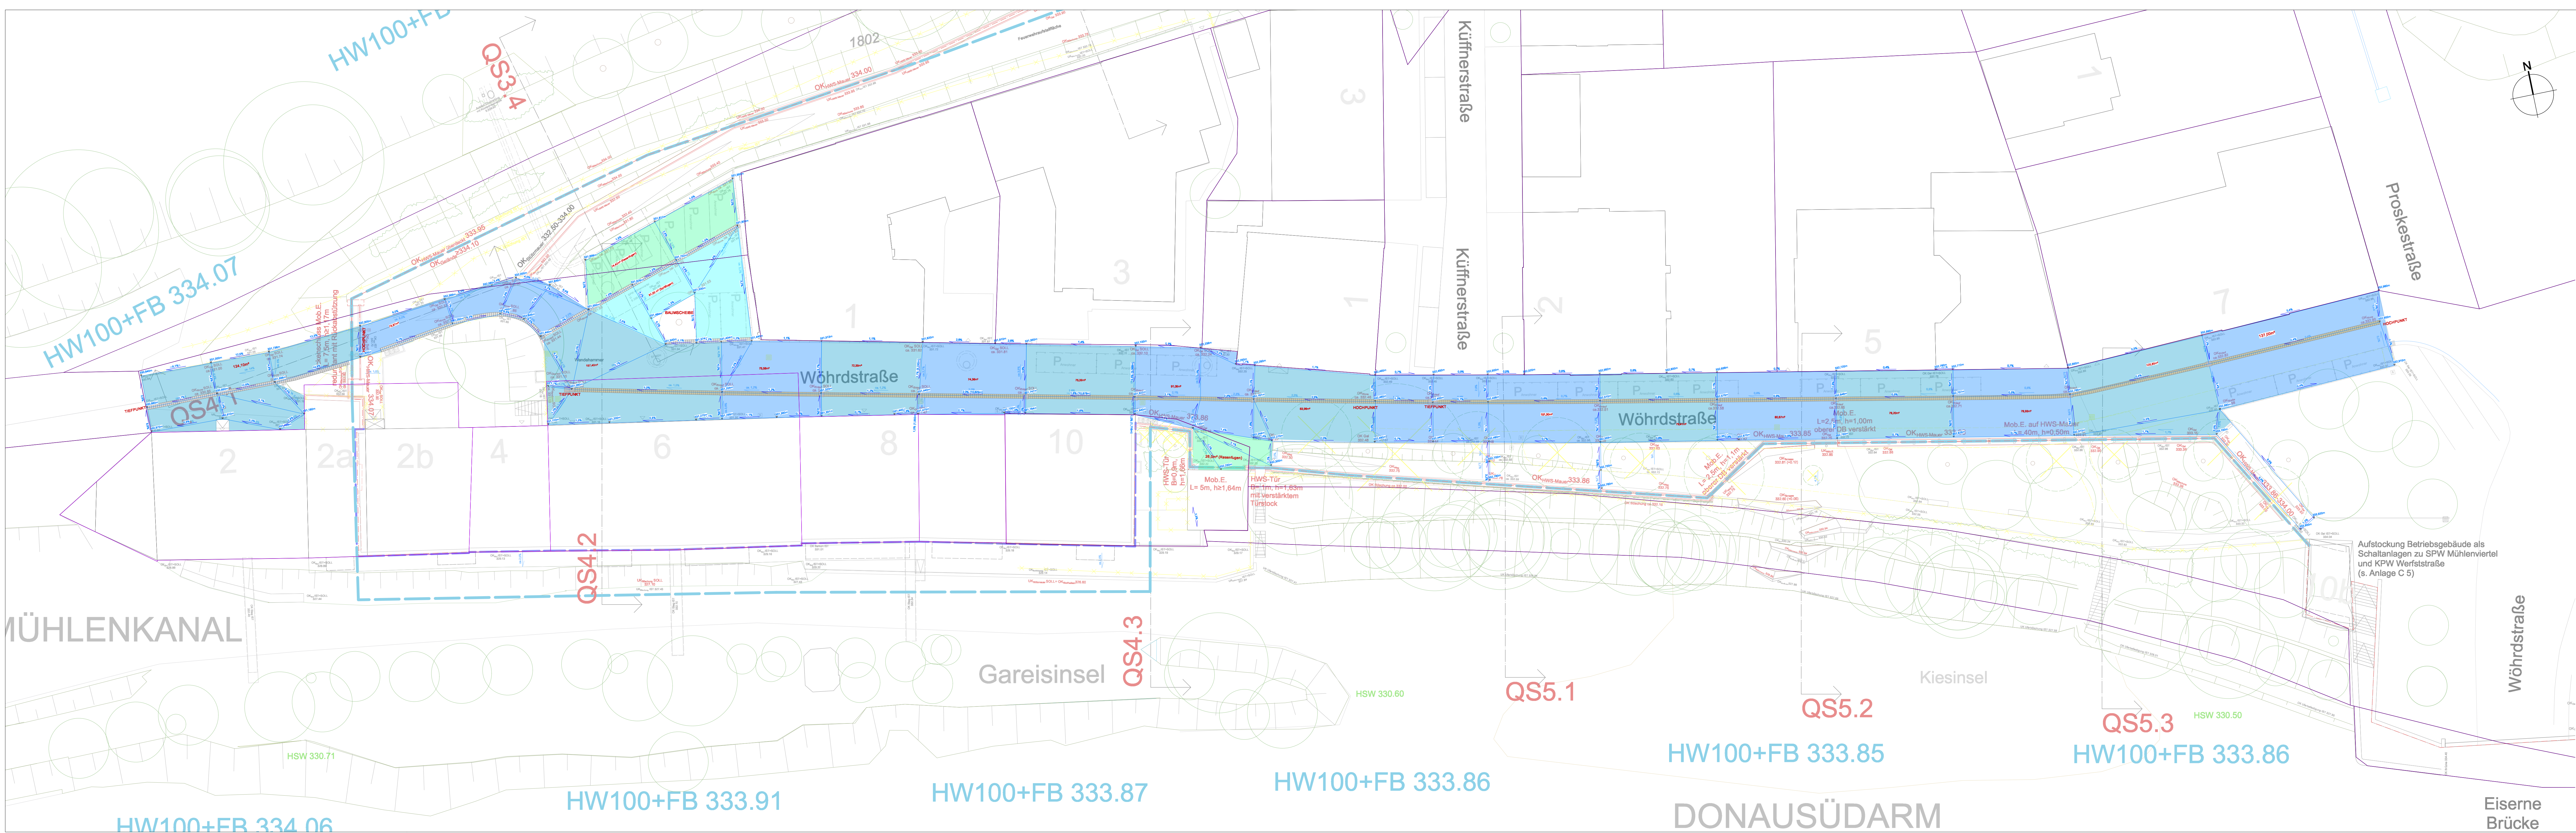

Vermerk Genehmigungsbehörde:			
Wasserwirtschaftsamt Regensburg STADT REGENSBURG			
a			
b			
c			
d			
e			
f			
Index	Bemerkung	geändert am	Name
Übersichtsplan			
Planabschnitt 4+5 Übersichtsplan			
Vorbau:	Hochwasserschutz Regensburg Abschnitt H Unterer Wöhrd PLANFESTSTELLUNG	Plan-Code:	36200-G-I 1.1
Landkreis/ Stadt:	Regensburg	Anlage:	I 1.1
Vorbauvertrager:	Freistaat Bayern, Wasserwirtschaftsamt Landshuter Straße 59, 93053 Regensburg	Plan-Nr.:	RB-H-GP 4+5-200
Maßstab:	M 1:200	Vorbauvertragsnummer:	011362001015
Planinhalt:	Planabschnitt (PA) 4+5 Gefälleplanung Westliche Wöhrdstraße	Lagebezug:	GK4 (BPG 31488)
Planung:	Arbeitsgemeinschaft TEAM 3 schöngarten architektur und landschaftsbau grünhof architektur gym architektur	entw.:	3/2024
Datum:	30.04.2025	gepr.:	4/2025
	Unterschrift Entwurfsverfasser	gepr.:	5/2025
		Unterschrift Vorbauvertrager	