16
17
18
19
20
21
22
23
24
3a
3
a
1
2
27
28
29
5
8
10
12
14
Inselstraße
Am Winterhafen
Werftstraße
Werftstraße
Hochufer
Linde
DONAUSÜDARM
HW100+FB 333.63
HW100+FB 333.60
HW100+FB 333.61
HW100+FB 333.60
HW100+FB 333.
HSW 333.40
HSW 333.39
HSW 333.34
QS7.1
QS7.2
QS7.3
QS7.4
QS7.5
QS7.6
S.5
Mob.E. auf HWS-Mauer L=35m,1,52m<h<1,75m
OKHWS-Mauer 332.09 bis 331.85
Fläche: 188,0qm
Fläche: 244,2qm
OKHWS-Mauer 331.85
Mob.E. L=10m, h≥2,69m
Festlegung: Gartenweg darf eingestaut werden (EFOK liegt oberhalb) HAmax 331.08
Überlauf
hist. Schiffspoller
Fläche: 20,8qm
HAmax 331.14
Mob.E. auf HWS-Mauer L= 27,5m h≥1,78m
Fläche: 125,5qm
Mob.E. L=5,0m, h≥2,59m
Fläche: 110,3qm
Mob.E. auf HWS-Mauer L= 65m, h≥1,78m
Fläche: 111,9qm
HAmax 331.16
Fläche: 196,2qm
SPW Inselstraße
Rückstauklappe SPW Inselstraße OK 330.80
Fläche: 418,3qm
OKHWS-Mauer 331.86
OKHWS-Mauer 332.37
Mob.E. L= 40m,1,73m≥h≥1,07m
OKHWS-Mauer 332.54
Mob.E. L= 10m,1,8m≤h≤1,92m
Fläche: 146,9qm
OKHWS-Mauer 332.65
Fläche: 200,0qm
Mob.E. L= 47,5m; 0,95m≥h≥0,50m
OKHWS-Mauer 332.94
OKHWS-Mauer 333.10
Mob.E. L= 22,5m; h≤0,50m
HWS-Mauer L=8,6m; h≥0,60m
OKHWS-Mauer 333.59
OKHWS-Mauer 333.77
N

Vermerke Genehmigungsbehörde :

Wasserwirtschaftsamt Regensburg

STADT REGENSBURG

| Index | Bemerkung | geändert am | Name | geprüft am | Name |
|---|---|---|---|---|---|
| c | | | | | |
| b | | | | | |
| a | | | | | |

Übersichtslageplan :

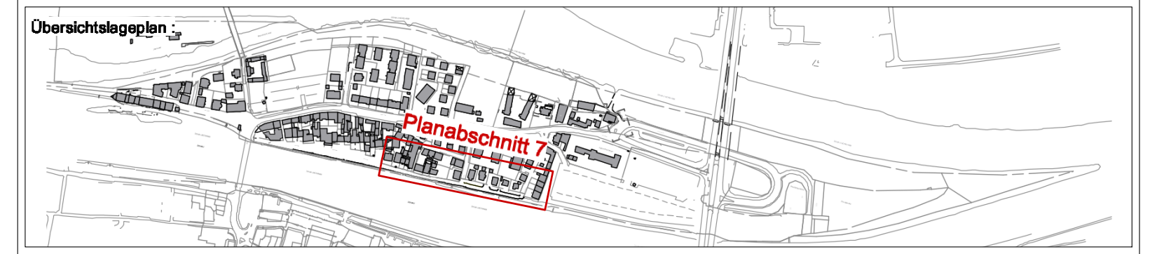
Planabschnitt 7

Vorhaben : **Hochwasserschutz Regensburg**
**Abschnitt H Unterer Wöhrd**
PLANFESTSTELLUNG

Plan-Code : 36200-G-I 1.3
Anlage : I 1.3
Phase : G
Plan-Nr. : RB-H- GP 7-200

Landkreis/ Stadt : Regensburg

Vorhabensträger : Freistaat Bayern, Wasserwirtschaftsamt
Landshuter Straße 59, 9053 Regensburg

Vorhabenskennzeichen: G1t 3620001015

Maßstab : M 1:200

Planinhalt : Planabschnitt (PA) 7
Gefälleplanung Östliche Werftstraße

Lagebezug: GK4 (EPSG 31468)
Höhenbezug: Regensburger Höhennetz aus 1927 in m ü.NN (≠ DHHN12/ 92/ 2016 des LDBV)

Planung : Arbeitsgemeinschaft TEAM 3
schömigplan INGENIEURGESELLSCHAFT mbH
archiscape architekten und landschaftsarchitekten
gm. Landschafts architekten

| | | |
|---|---|---|
| entw. : | 3/2024 | team 3 |
| gez. : | 4/2025 | UB |
| gepr. : | 5/2025 | WWA |

30.04. 2025
Datum
Unterschrift Entwurfsverfasser

26.05. 2025
Datum
Unterschrift Vorhabensträger