LEGENDE

- Flurstücksgrenze
- Gehölzbestand, Erhalt
- Sträucher/ Hecke im Bestand, Erhalt
- 333.60 Höhe im Bestand
- Böschung im Bestand
- Asphaltbelag im Bestand
- Terrasse im Bestand (Erhalt/ Wiederherstellen)
- ungebundener Belag (Schotter) im Bestand
- Abbruch
- Gebäude im Bestand
- Tiefgarage im Bestand
- Denkmal im Bestand
- Extensive Wiese im Bestand (Erhalt/ Wiederherstellen)
- Ufermauer, saniert
- Mauer im Bestand
- Gehölzstandort, Entfall
- Neupflanzung Gehölz Standort verschieblich
- Neupflanzung Strauch/ Hecke Standort verschieblich
- 333.60 geplante Höhe
- Böschung, neu
- neuer Pflasterbelag gebunden, geschnitten/ behauen
- neuer Pflasterbelag, ungebunden mit Splittfuge/ Rasenfuge
- neue Schotterdecke/ wassergebundene Decke
- Rasengittersteine, neu
- Schotterrasen, neu (Betriebsweg)
- Wiese mit hohem Blühanteil (Gräser/ Stauden), neu
- wechselfeuchte Wiese, neu
- extensiv gepflegte Wiese, neu
- intensiv gepflegte Wiese, neu
- Wasserbausteine/ Trockenmauer, neu
- Achse mobiler HWS (Mobile Elemente)
- mobiler HWS (Tor/ einachsiges Mob.E.)
- stationärer HWS (überirdische Mauer)
- stationärer HWS mit aufgesetzten mobilen Elementen
- Achse vertikale Untergrundabdichtung
- horizontale Untergrundabdichtung
- gebäudeintegrierter HW-Schutz
- Integration bestehender mobiler Verschluss
- P PKW-Stellplatz neu
- ♿ behindertengerecht
- neue Treppenanlage
- Bordstein, neu
- Sitzbank, neu
- Blocksteinquader, neu
- ○ Poller, neu
- Einfriedung, Zaunanlage
- Stützmauer, neu
- Handlauf/ Geländer, neu
- offene Straßenentwässerungsrinne, neu
- Rinne mit Abdeckung, neu
- Straßeneinlauf, neu
- ◯ Schacht, neu

N

Vermerke Genehmigungsbehörde :

Wasserwirtschaftsamt Regensburg

STADT REGENSBURG

Index	Bemerkung	geändert am	Name	geprüft am	Name
c					
b					
a					

Übersichtslageplan :

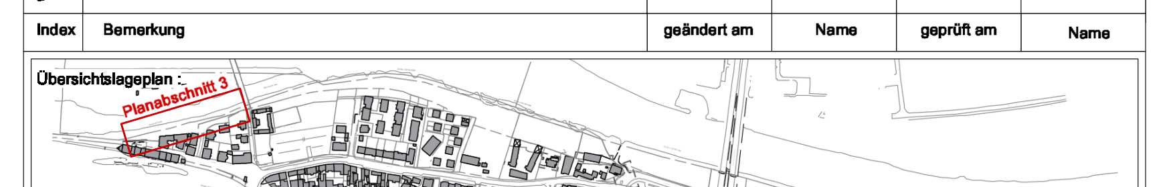

Vorhaben :	Hochwasserschutz Regensburg Abschnitt H Unterer Wöhrd PLANFESTSTELLUNG	Plan-Code :	36200-G-B 3.0.0
		Anlage :	B 3.0.0 — Phase : G
Landkreis/ Stadt :	Regensburg	Plan-Nr. :	RB-H-LP 3-200
Vorhabensträger :	Freistaat Bayern, Wasserwirtschaftsamt Landshuter Straße 59, 9053 Regensburg	Vorhabenskennzeichen:	G1t 3620001015
Maßstab : M 1:200	Planinhalt : Planabschnitt (PA) 3 Lageplanausschnitt Brandner Kanal Proskestr. 5 bis Wöhrdstr. 2	Lagebezug: Höhenbezug:	GK4 (EPSG 31468) Regensburger Höhennetz aus 1927 in m ü.NN (≠ DHHN12/ 92/ 2016 des LDBV)
Planung :	Arbeitsgemeinschaft TEAM 3 schömigplan INGENIEURGESELLSCHAFT mbH archiscape architekten und landschaftsarchitekten gm. Landschafts architekten	entw. : gez. : gepr. :	3/2024 team 3 4/2025 UB 5/2025 WWA

30.04. 2025
Datum

Unterschrift Entwurfsverfasser

26.05. 2025
Datum

Unterschrift Vorhabensträger