


STADT REGENSBURG

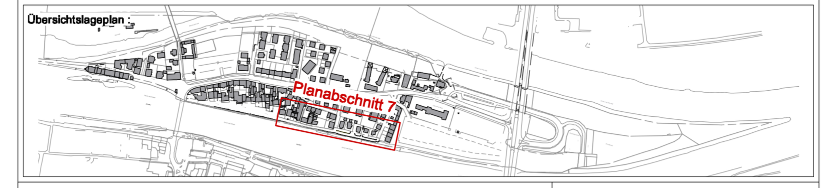

Vorhaben :	Hochwasserschutz Regensburg Abschnitt H Unterer Wöhrd PLANFESTSTELLUNG	Plan-Code :	36200-G-B 7.0
		Anlage : B 7.0	Phase : G
Landkreis/ Stadt :	Regensburg	Plan-Nr. :	RB-H- LP 7-200
Vorhabensträger :	Freistaat Bayern, Wasserwirtschaftsamt Landshuter Straße 59, 9053 Regensburg	Vorhabenskennzeichen:	G1t 3620001015
Maßstab : M 1:200	Planinhalt : Planabschnitt (PA) 7 Lageplanausschnitt Östliche Werftstraße Werftstr. 17 bis Am Winterhafen 14	Lagebezug:	GK4 (EPSG 31468)
		Höhenbezug:	Regensburger Höhennetz aus 1927 in m ü.NN (≠ DHHN12/ 92/ 2016 des LDBV)
Planung :	Arbeitsgemeinschaft TEAM 3	entw. : 3/2024	team 3
	schömigplan INGENIEURGESELLSCHAFT mbH; archiscape architekten und landschaftsarchitekten; lgm. Landschafts architekten	gez. : 4/2025	UB
		gepr. : 5/2025	WWA

30.04. 2025	[signature]	26.05. 2025	[signature]
Datum	Unterschrift Entwurfsverfasser	Datum	Unterschrift Vorhabensträger