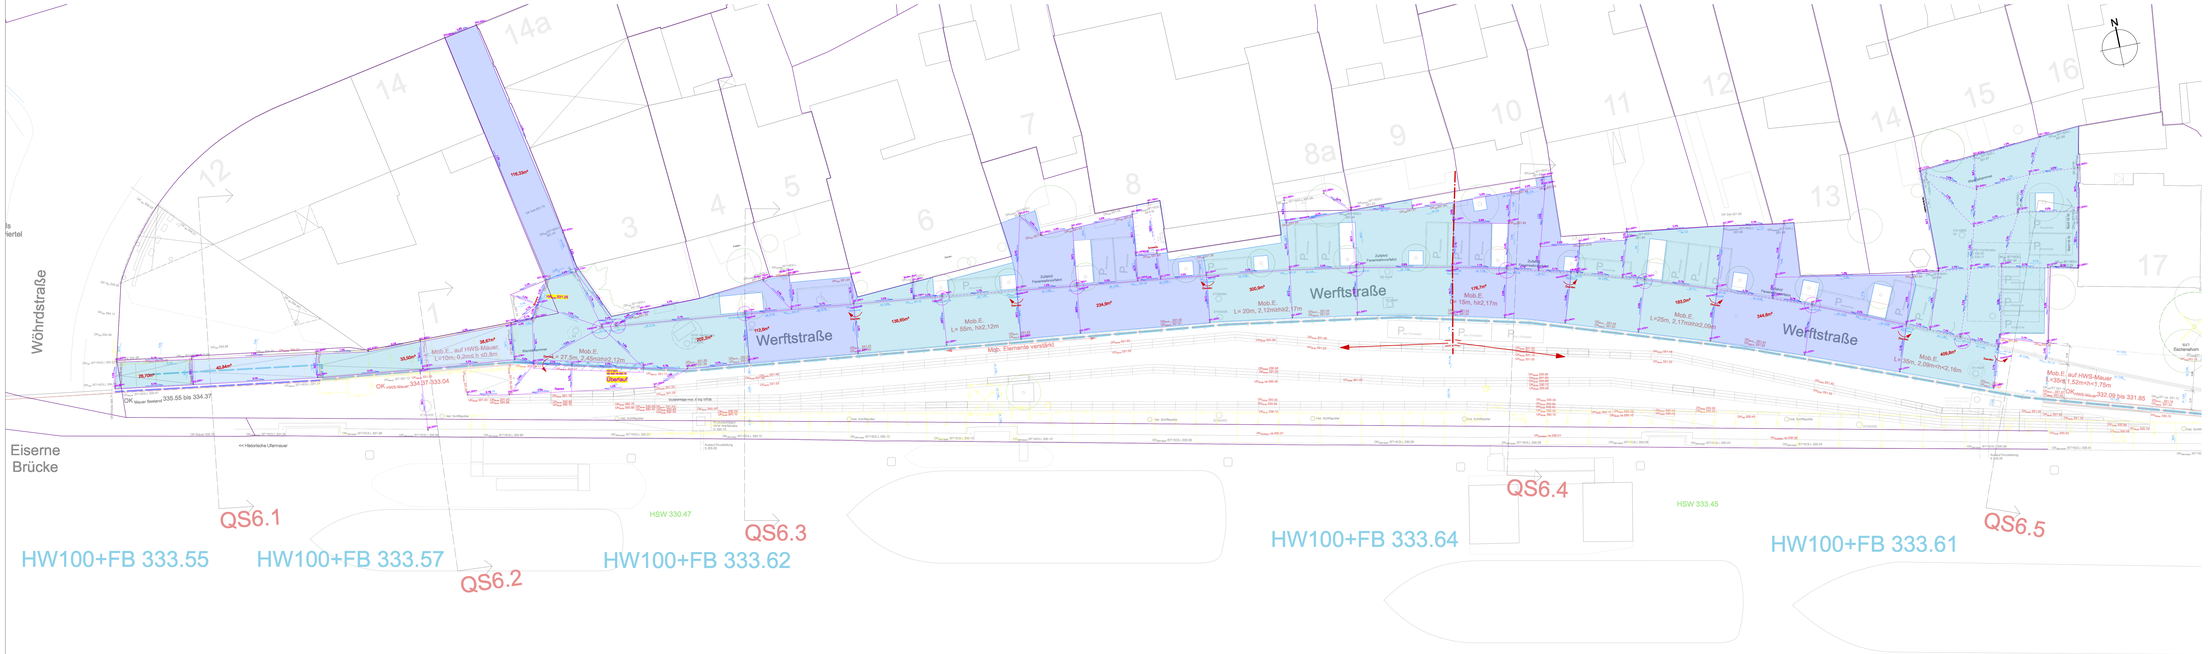


Vermerke Genehmigungsfreistellung :

Wasserwirtschaftsamt Regensburg

STADT REGENSBURG

Index	Bemerkung	gezeichnet am	Name	geprüft am	Name
a					
b					
c					

Übersichtslageplan :



Vorhaben:	Hochwasserschutz Regensburg Abschnitt H Unterer Wöhrd PLANFESTSTELLUNG	Plan-Code:	36200-GI-1.2
		Anlage: I 1.2	Plan-Nr.: G
Landkreis/ Stadt:	Regensburg	Plan-Nr.:	RB-H-GP 6-200
Vorhabenträger:	Freistaat Bayern, Wasserwirtschaftsamt Landshuter Straße 59, 9053 Regensburg	Vorhabenkennzeichnung:	SYLIB0300101S
Maßstab: M 1:200	Planinhalt: Planabschnitt (PA) 6	Lagebezug:	GKH (EPSG 31468)
	Gefällelieferung Westliche Werftstraße	Höhenbezug:	Regenburger Höhennetz, aus 1927 in m ü.Ü.NHN (1HN1912) bzw. 1985 (1DN1)
Planung:	Arbeitsgemeinschaft TEAM 3	erste.:	30334 Item 3
		gen.:	40028 UB
		gepr.:	50026 WWA
30.04.2026 Datum:	Unterschrift Entwurfsverfasser	06.05.2026 Datum:	Unterschrift Vorhabenträger