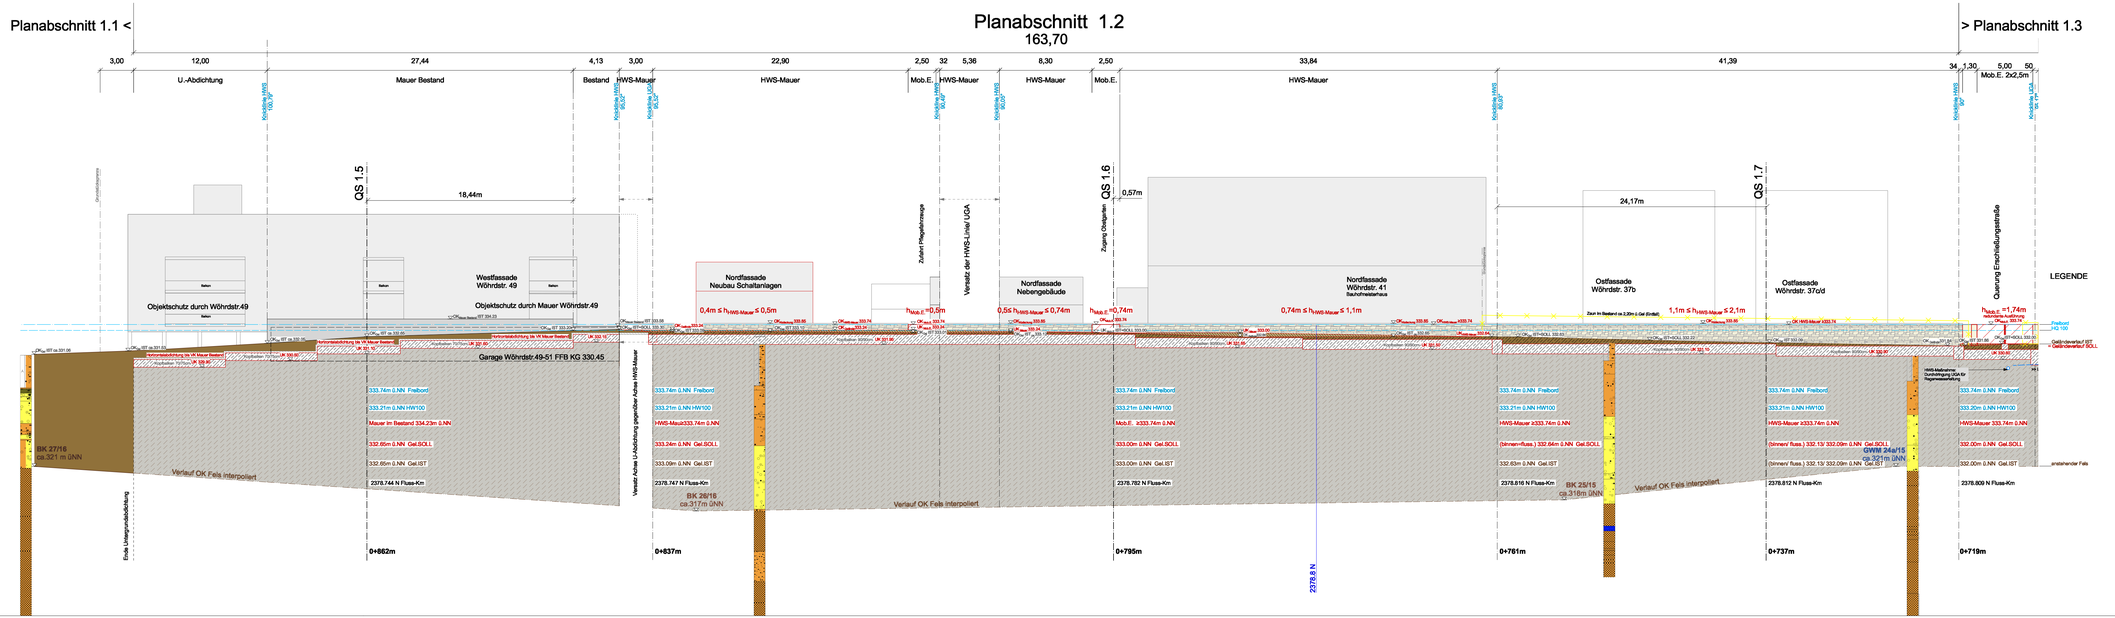

LEGENDE

- Höhe im Bestand
- Höhe in der Planung
- Mob.E. ø 2,5m
- HWS-Mauer
- Geländeauftrag
- Geländeabtrag
- Boden im Bestand/ Wiedereinbau
- Untergrundabdichtung
- Gründung
- Abbruchmaßnahmen

Legende zu den Bohrprofilen

	Kurzzeichen nach DIN 4023	Zeichen nach DIN 4023 und DIN 21920	Farbe nach DIN 4023
Kies	G		
Sand	S		
Schluff	U		
Ton	T		

Die schematische Darstellung der eingezeichneten Fassaden erfolgte auf Grundlage der Fotoauswertung aus dem VOF-Verfahren und dient allein der Veranschaulichung ohne Anspruch auf Vollständigkeit und Maßhaltigkeit.

- Integration mobiler Objektschutz im Bestand
- neues mobiles Element in Fensterlüftung
- neues druckdichtes Fenster/ Tür

Vermerke Genehmigungsbehörde :

Wasserwirtschaftsamt Regensburg

STADT REGENSBURG

Index	Bemerkung	geändert am	Name	geprüft am	Name
c					
b					
a					

Übersichtslageplan

Vorhaben : Hochwasserschutz Regensburg Abschnitt H Unterer Wöhrd

PLANFESTSTELLUNG

Landkreis/ Stadt : Regensburg

Vorhabenträger : Freistaat Bayern, Wasserwirtschaftsamt Landshuter Straße 59, 9053 Regensburg

Plan-Code : 36200-G-B 1.2.2

Anlage : B 1.2.2 Phase : G

Plan-Nr. : RB-H-PA1.2 LA-200

Vorhabenkennziffern: G1:3620000/1015

Maßstab : M 1:200

Planinhalt : Planabschnitt (PA) 1.2 Längsabwicklung Nordufer Wöhrddstr. 49 bis 37d/e

Legebezug : GK4 (EPSG 31468)

Höhenbezug : Regensburger Höhennetz aus 1927 (= ü.NN)/ DHHN12 (ab 2016 des LDBV)

Planung : Arbeitsgemeinschaft TEAM 3

Schönig Stahr Ingenieurgesellschaft mbH | Architekten | Landschaftsarchitekten

erst.:	3/2024	team 3	
gez.:	4/2025	LR	
gepr.:	5/2025	WWA	

30.04. 2025 Datum — Unterschrift Entwurfsverfasser

26.05. 2025 Datum — Unterschrift Vorhabenträger