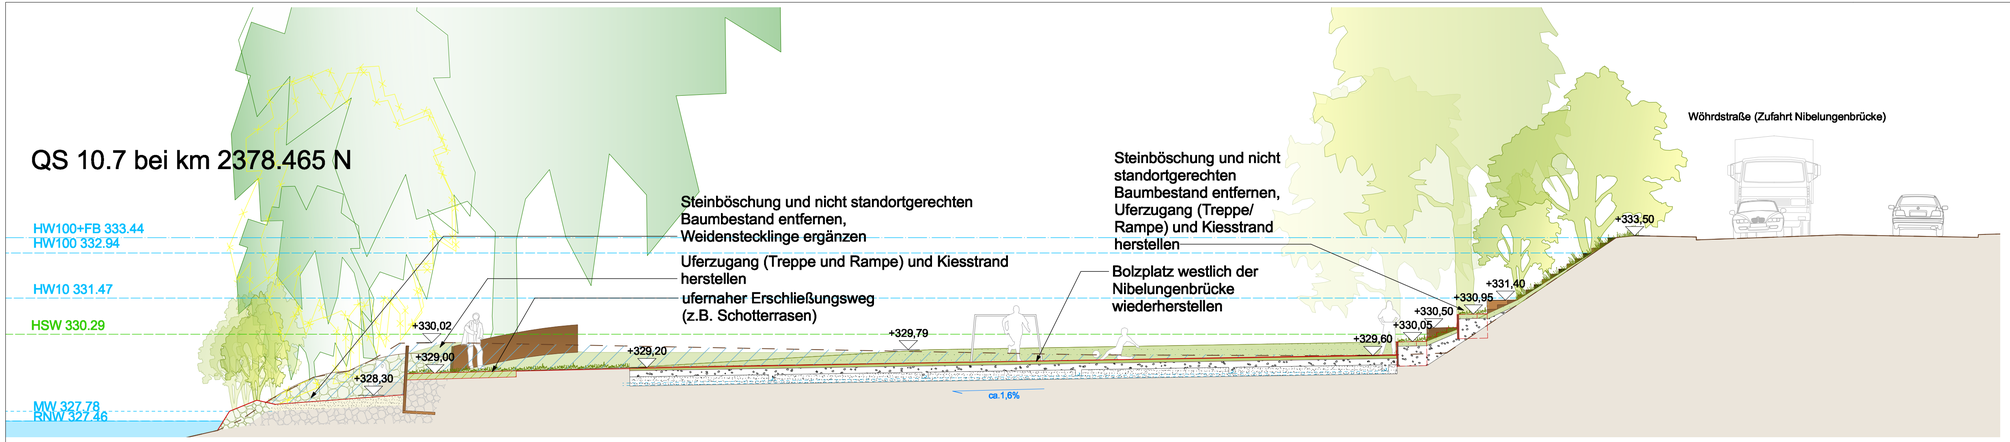

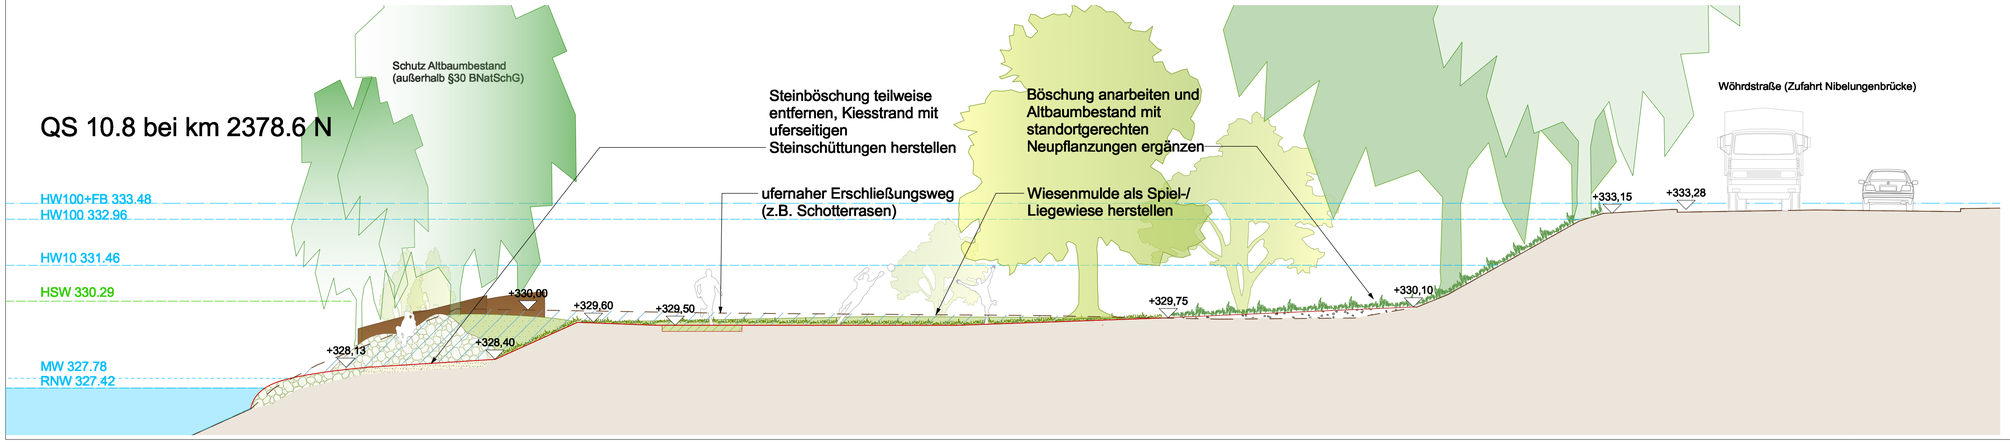

Legende

- +326,53 Höhenkote in müNN
- Mittelwasserlinie/ Röhrrichtzone
- Niedrigwasserzone
- Geländeverlauf im Bestand
- geplanter Geländeverlauf unterhalb Bestand (Abtrag)
- Geplanter Geländeverlauf oberhalb Bestand (Auftrag)
- Räumung
- geschotterter Erschließungsweg
- Sand-/ Kiesschüttung
- Steinschüttung/ Steinschlag
- Böschung im Bestand/ neu
- Baumbestand/ Neupflanzung

Vermerke Genehmigungsbehörde :

Wasserwirtschaftsamt Regensburg

STADT REGENSBURG

Index	Bemerkung	geändert am	Name	geprüft am	Name
c					
b					
a					

Übersichtslageplan

Vorhaben :	Hochwasserschutz Regensburg Abschnitt H Unterer Wöhrd PLANFESTSTELLUNG	Plan-Code :	36200-G-10.1.4
		Anlage : B10.1.4	Phase : G
Landkreis/ Stadt :	Regensburg	Plan-Nr. :	RB-H-QS10.7/8_100
Vorhabenträger :	Freistaat Bayern, Wasserwirtschaftsamt Landshuter Straße 59, 9053 Regensburg	Vorhabenkennzeichen:	G11 3620001015
Maßstab : 1:100	Planinhalt : Planabschnitt (PA)10 Querschnitte 10.7/ 10.8.	Lagebezug:	GK4 (EPSG 31468)
		Höhenbezug:	Regensburger Höhennetz aus 1927 in m ü.NN (# DHHN12/ 92/ 2016 des LVermV)
Planung :	Arbeitsgemeinschaft TEAM 3	erstw. : 3/2024	team 3
		gez. : 4/2025	UB
		gepr. : 5/2025	WWA

schönig plan INGENIEURGESELLSCHAFT mbH · archiscape architekten und landschaftsarchitekten · tgm. Landschaftsarchitekten

30.04. 2025		28.05. 2025	
Datum	Unterschrift Entwurfsverfasser	Datum	Unterschrift Vorhabenträger