Planabschnitt 3

199,60

Planabschnitt 2 <

> Planabschnitt 4

9,03 HWS-Mauer | 9,22 Brückenanschlüsse Grieser Steg | 13,66 HWS-Mauer | 19,05 HWS-Mauer | 21,84 HWS-Mauer | 9,04 HWS-Mauer | 2,50 Mob.E. h=1,1m | 14,62 HWS-Mauer | 27,08 HWS-Mauer | 5,00 Sx Mob.E. h=0,8m | 28,65 HWS-Mauer | 18,00 HWS-Mauer | 8,13 HWS-Mauer überdeckt | 31,41 HWS-Mauer überdeckt | 62 | 2,50 Sonderf. | 5,00 Sx Mob.E.a 2,5m | 5,74 HWS-Mauer | 11,82 Dichtwand

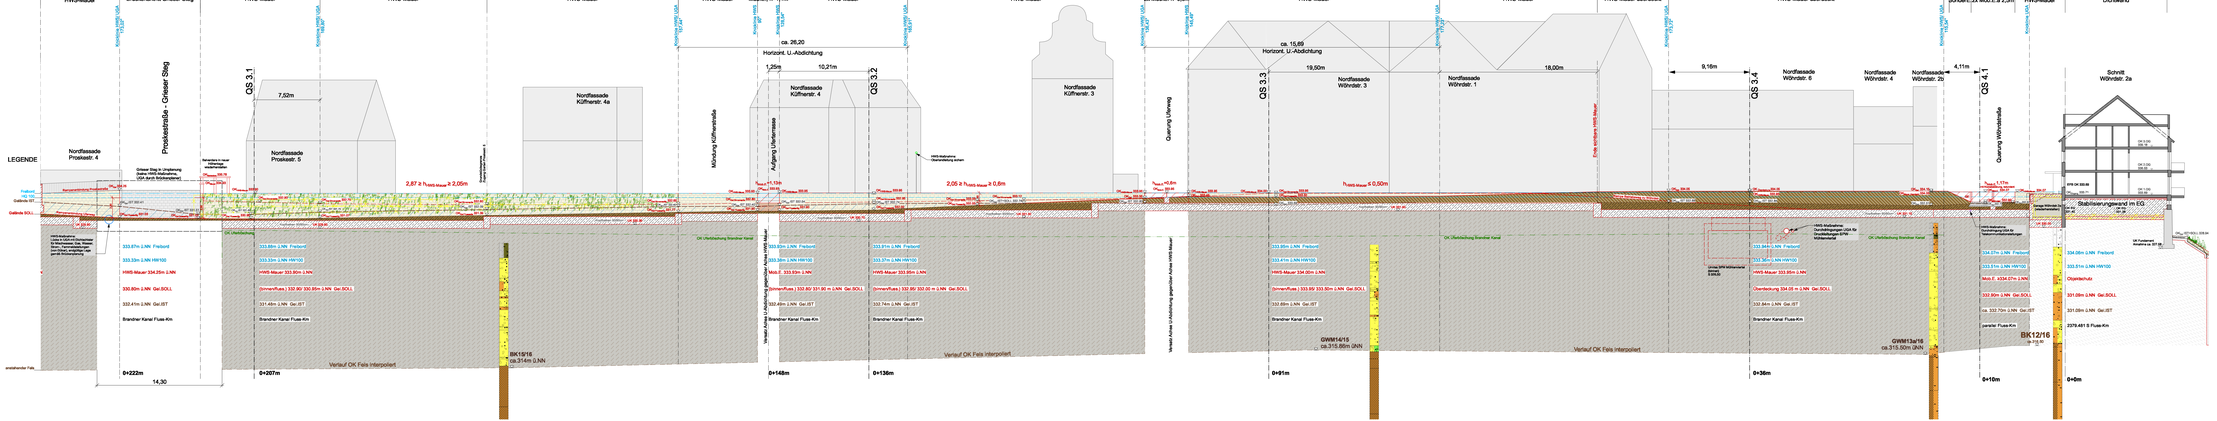
LEGENDE
Prosteststraße – Grieser Steg
Nordfassade Prostestr. 4
Grieser Steg in Umplombung (Ausbau Bestandsplatten UZR durch Stahlbetonplatte)
Verrohrung in neuer Anbindung Grieser Steg
Freiland
Gelände IST
Gelände SOLL
Bestandsmauerwerk
Bestandsfundament
Lückige Kalkhaltige Ziegelsteinmauer, Fundamentsgrundung, Mauerwerk, Fachwerkbauten, Fundamentsgrundung, ganzlich Mörtelzerspreng.
HWS-Mauer Ausbau Stahlbetonplatte
Verlauf OK Fels interpoliert
Nordfassade Prostestr. 5
7,52m
2,87 ≥ h_bess.Mauer ≥ 2,05m
QS 3.1
Nordfassade Käffnerstr. 4a
Münzburg Käffnerstraße
Nordfassade Käffnerstr. 4
Aufgang Käffnerstraße
Horizont. U.-Abdichtung
ca. 26,20
1,25m
10,21m
QS 3.2
2,05 ≥ h_bess.Mauer ≥ 0,6m
Nordfassade Käffnerstr. 3
Querung Käffnerweg
ca. 15,69
Horizont. U.-Abdichtung
19,50m
Nordfassade Wörndstr. 3
QS 3.3
Nordfassade Wörndstr. 1
18,00m
Feste Anbindung HWS-Mauer
h_bess.Mauer ≤ 0,50m
9,16m
QS 3.4
Nordfassade Wörndstr. 5
Nordfassade Wörndstr. 4
Nordfassade Wörndstr. 2b
4,11m
QS 4.1
Querung Wörndstraße
Schnitt Wörndstr. 2a
Stabilisierungswand im EG
Dichtwand
Ausbau Bestandsmauerwerk
Ausbau Bestandsfundament