Planabschnitt 4

134,40

Planabschnitt 3 <

> Planabschnitt 5

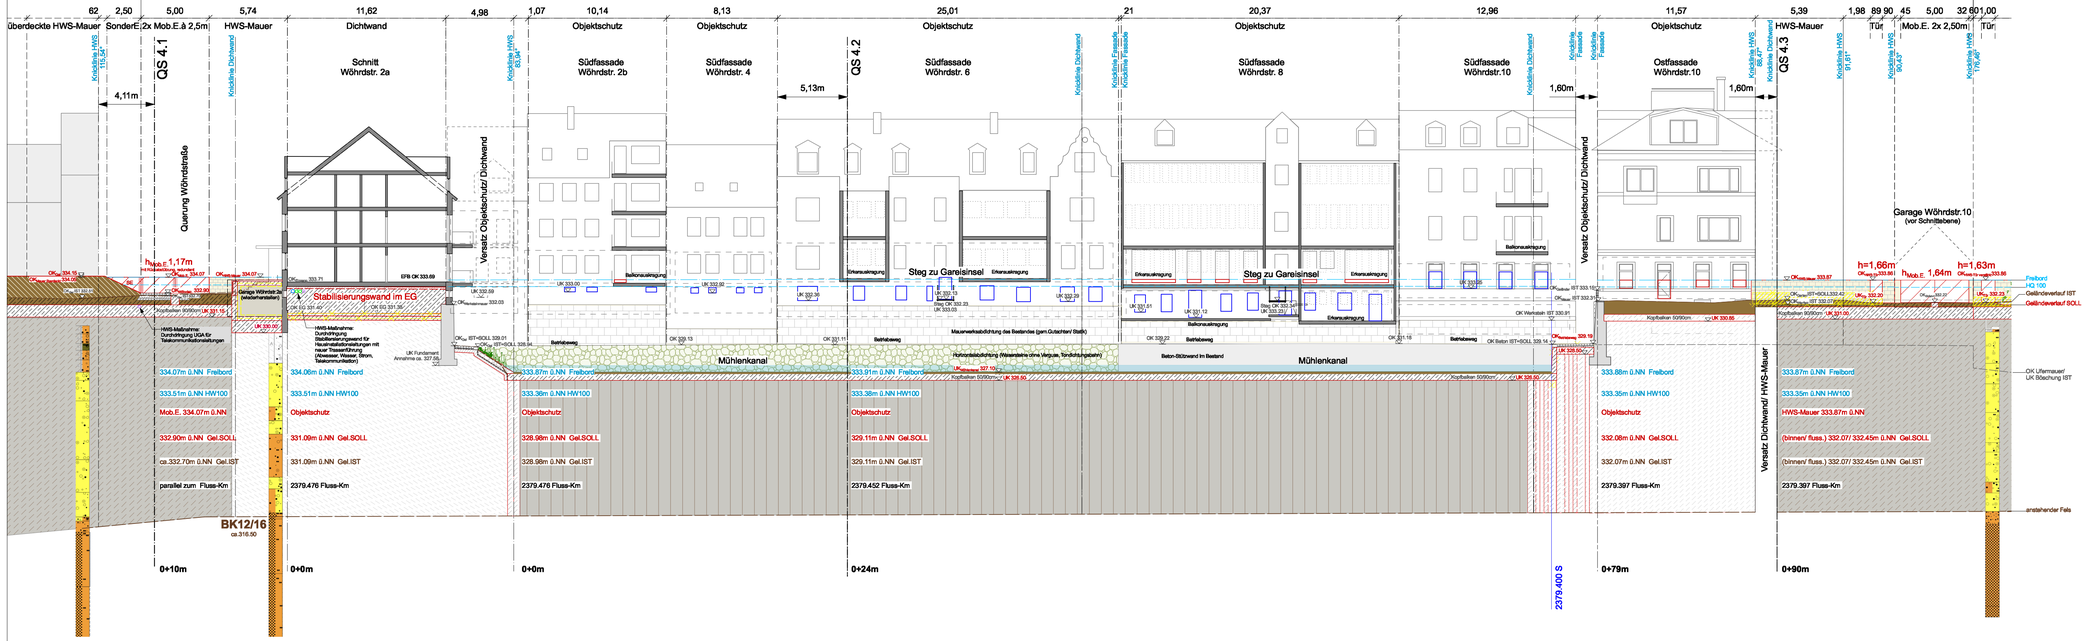

LEGENDE

- 32 OK$_{Best.}$ 334.35 — Höhe im Bestand
- 32 OK$_{Plan}$ 333.88 — Höhe in der Planung
- Mob.E. à 2,5m
- HWS-Mauer
- Geländeauftrag
- Geländeabtrag
- Boden im Bestand/ Wiederauftrag
- Untergrundabdichtung
- Gründung
- Abbruchmaßnahmen

Legende zu den Bohrprofilen

	Kurzzeichen nach DIN 4023	Zeichen nach DIN 4023 und DIN 21920	Farbe nach DIN 4023
Kies	G		
Sand	S		
Schluff	U		
Ton	T		

Die schematische Darstellung der abgewickelten Fassaden erfolgte auf Grundlage der Fotoabwicklung aus dem VOF-Verfahren und dient allein der Veranschaulichung ohne Anspruch auf Vollständigkeit und Maßhaltigkeit.

- Integration mobiler Objektschutz im Bestand
- neues mobiles Element in Fensteröffnung
- neues druckdichtes Fenster/ Tür

Vermerke Genehmigungsbehörde :

Wasserwirtschaftsamt Regensburg

STADT REGENSBURG

Index	Bemerkung	geändert am	Name	geprüft am	Name
c					
b					
a					

Übersichtslageplan

Vorhaben :	Hochwasserschutz Regensburg Abschnitt H Unterer Wöhrd PLANFEESTSTELLUNG	Plan-Code :	36200-G-B 4.2.0
		Anlage : B 4.2.0	Phase : G
Landkreis/ Stadt :	Regensburg	Plan-Nr. :	RB-H-LA 4-200
Vorhabensträger :	Freistaat Bayern, Wasserwirtschaftsamt Landshuter Straße 59, 9053 Regensburg	Vorhabenskennzeichen:	G1t:3620001015
Maßstab : M 1:200	Planinhalt : Planabschnitt (PA) 4 Längsabwicklung Mühlenviertel Wöhrdstr. 2, 4, 6, 8, 10	Lagebezug:	GK4 (ETRS G 31468)
		Höhenbezug:	Regensburger Höhennetz aus 1927 in m ü.NN (# DHHN12/ 92/ 2016 des LSBV)
Planung :	Arbeitsgemeinschaft TEAM 3 schömigplan INGENIEURGESELLSCHAFT mbH · archiscape architekten und landschaftsarchitekten · ym. Landschaftsarchitekten	erstw. : 3/2024	team 3
		gez. : 4/2025	UB
		gepr. : 5/2025	WWA
30.04. 2025 Datum	Unterschrift Entwurfsverfasser	26.05. 2025 Datum	Unterschrift Vorhabensträger