Planabschnitt 5

170,50

Planabschnitt 4 <

> Planabschnitt 6

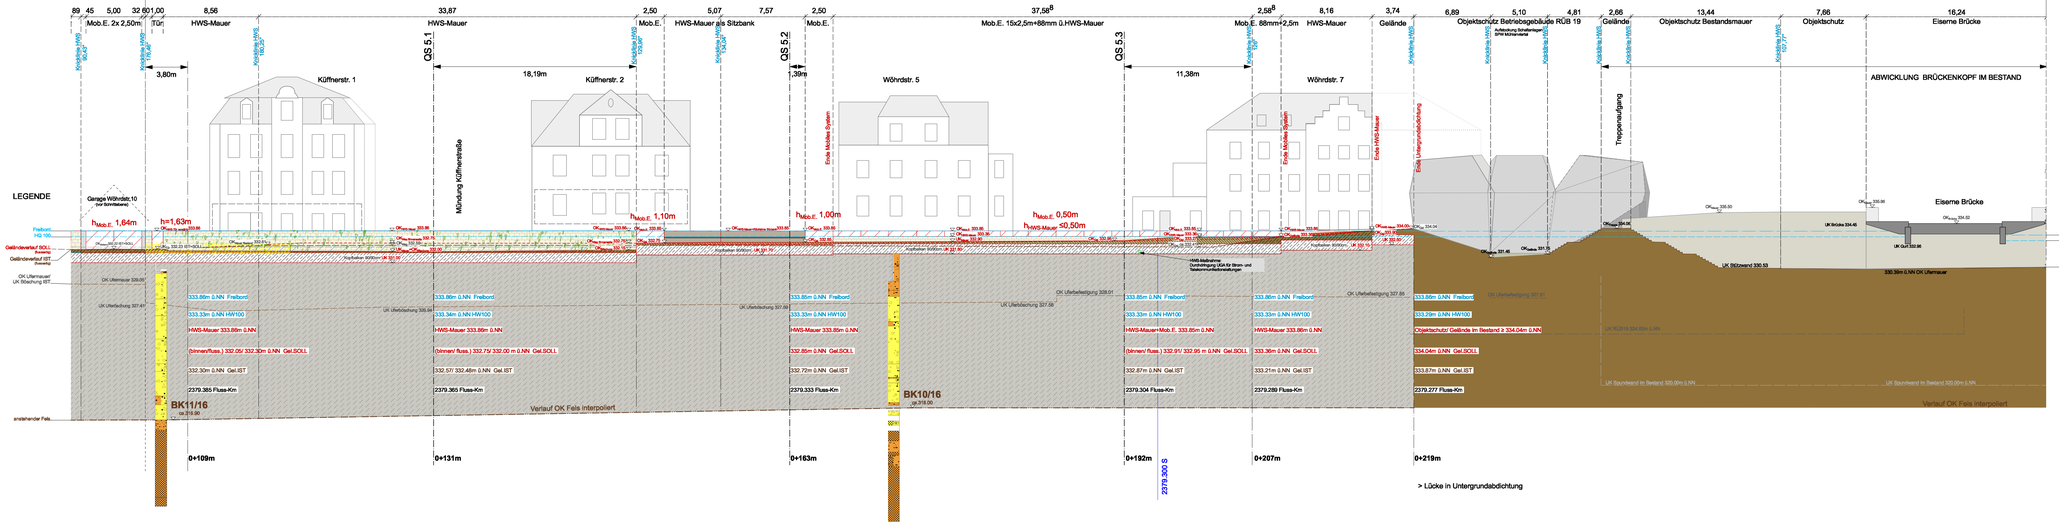

LEGENDE

- Höhe im Bestand
- Höhe in der Planung
- Mob.E. ≥ 2,5m
- HWS-Mauer
- Geländeoeffnung
- Geländeabtrag
- Boden im Bestand Wiederauftrag
- Untergrundabdichtung
- Gründung
- Abbruchmaßnahmen

Legende zu den Bohrprofilen

	Kurzzeichen nach DIN 4023	Zeichen nach DIN 4023 und DIN 21920	Farbe nach DIN 4023
Kies	G		
Sand	S		
Schluff	U		
Ton	T		

Die schematische Darstellung der abgewickelten Fassaden erfolgte auf Grundlage der Fotoaufnahmen aus dem VOF-Verfahren und dient allein der Veranschaulichung ohne Anspruch auf Vollständigkeit und Maßhaltigkeit.

- Integration mobiler Objektschutz im Bestand
- neues mobiles Element in Fensteröffnung
- neues druckdichtes Fenster/ Tür

Vermerke Genehmigungsbehörde :

Wasserwirtschaftsamt Regensburg

STADT REGENSBURG

Index	Bemerkung	geändert am	Name	geprüft am	Name
c					
b					
a					

Übersichtslageplan

Vorhaben : Hochwasserschutz Regensburg
Abschnitt H Unterer Wöhrd
PLANFESTSTELLUNG

Landkreis/ Stadt : Regensburg

Vorhabenträger : Freistaat Bayern, Wasserwirtschaftsamt Landshuter Straße 59, 9053 Regensburg

Plan-Code: 36200-G-B 5.2.0

Anlage : B 5.2.0 Phase : G

Plan-Nr. : RB-H-LA 5-200

Vorhabenkennzeichen: G31.36200001015

Maßstab : M 1:200

Planinhalt : Planabschnitt (PA) 5
Längsabwicklung Westliche Wöhrdstraße
Küffnerstr.1 bis Eiserne Brücke

Lagebezug: GK4 (EPSG:31468)

Höhenbezug: Regensburger Höhennetz: aus 1927 in m (LNN)/ DHHN12 (ab 2016 das LDBV)

Planung : Arbeitsgemeinschaft TEAM 3

schönig plan INGENIEURGESELLSCHAFT mbH
archiscape architekten und ingenieure
tyr. landschaftsarchitekten

erst. :	3/2024	team 3
gez. :	4/2025	LB
gecr. :	5/2025	WWA

30.04. 2025 Datum — Unterschrift Entwurfsverfasser

26.05. 2025 Datum — Unterschrift Vorhabenträger