Planabschnitt 6

223,50

Planabschnitt 5 <

> Planabschnitt 7

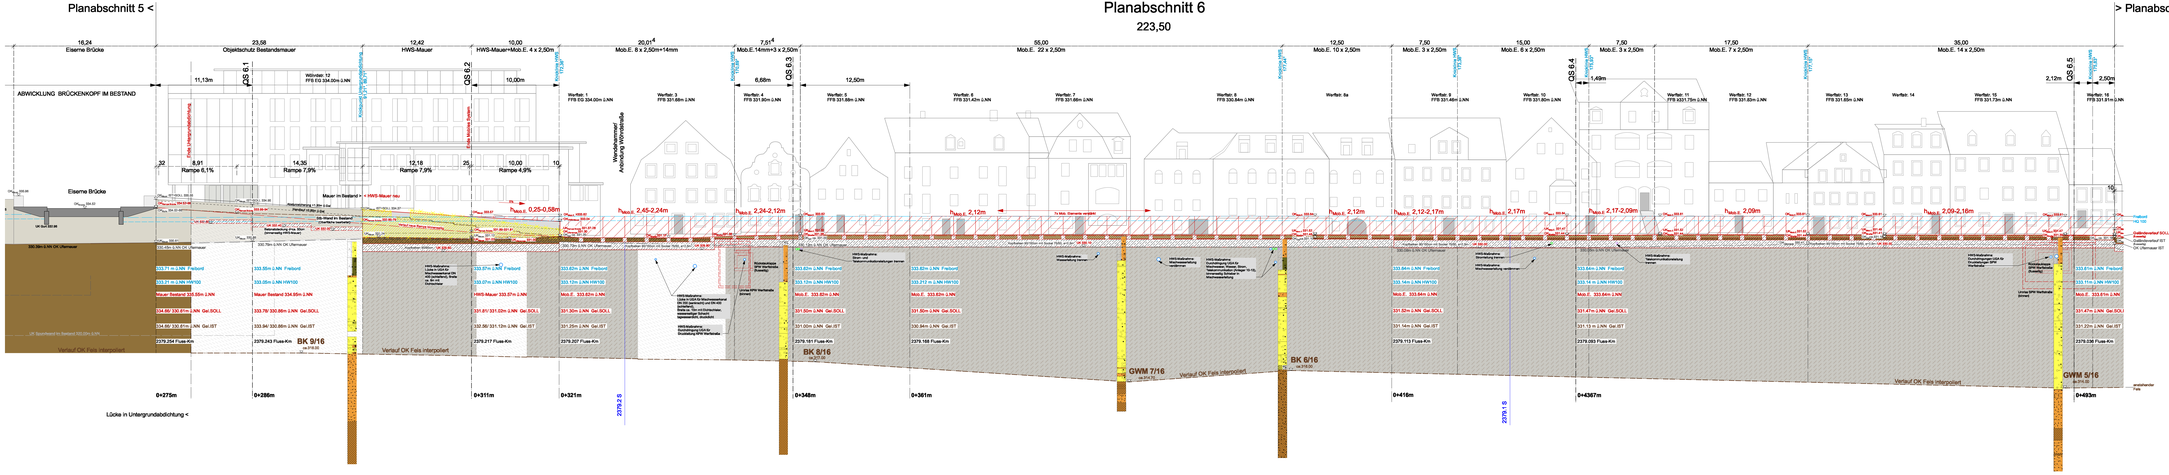

LEGENDE

- Höhe im Bestand
- Höhe in der Planung
- Mob.E. ü 2.5m
- HWS-Mauer
- Gebäudeabriß
- Gabionabriß
- Boden im Bestand Wiedereinbau
- Untergrundabdichtung
- Gründung
- Altlastenuntersuchungen

Legende zu den Bohrprofilen

	Kurzzeichen nach DIN 4023	Zeichen nach DIN 4023 und DIN 21920	Farbe nach DIN 4023
Kies	G		
Sand	S		
Schluff	U		
Ton	T		

Die schematische Darstellung der abgestuften Dataeinträge erfolgte auf Grundlage der Bohrprofile und der Bestandsplanung. Es wird deshalb der Vorbehalt einer Abweichung ohne Anspruch auf Vollständigkeit und Richtigkeit.

- Integration mobiler Objektschutz im Bestand
- neues mobiles Element in Fundamentfüllung
- neues drucklöschbares Fundament Typ

Vorrauche Genehmigungsbehörde :

Wasserwirtschaftsamt Regensburg

STADT REGENSBURG

Index	Bemerkung	gezeichnet am	Name	geprüft am	Name
a					
b					
c					
d					
e					

Übersichtslageplan

Vorhaben :	Hochwasserschutz Regensburg Abschnitt H Unterer Wöhrd PLANFESTSTELLUNG
Plan-Codiz:	36200-G-B 6.2.0
Anlage:	B 6.2.0
Plan-Nr.:	RB-H-L.6-200
Landkreis/ Stadt :	Regensburg
Vorhabensträger:	Freistaat Bayern, Wasserwirtschaftsamt Landshuter Straße 59, 9053 Regensburg
Vorhabenbezeichnet:	5/1.9000001016
Maßstab:	M 1:200
Planinhalt :	Planabschnitt (PA) 6 Längsbebauung Westliche Wörthstraße Werfter: 1-15
Lageplan:	GKK (EPSG:31468)
Höhensystem:	Regensburger Höhensystem, aus 1927 in m (LAN) in DHHN12 SD 2016 aus LGRC)
Planung:	Arbeitsgemeinschaft TEAM 3 schlichting+partner architekten partnerschaft mbb SPZ116 GBR Landschaftsarchitekten TM. Landschaftsarchitekten
erst.:	3/2024	bearb.:	
gez.:	4/2026	ÜB:	
gep.:	5/2026	WWA:	
Datum: 30.04. 2026	Unterschrift Entwurfsverfasser	Datum: 30.05. 2026	Unterschrift Vorhabensträger