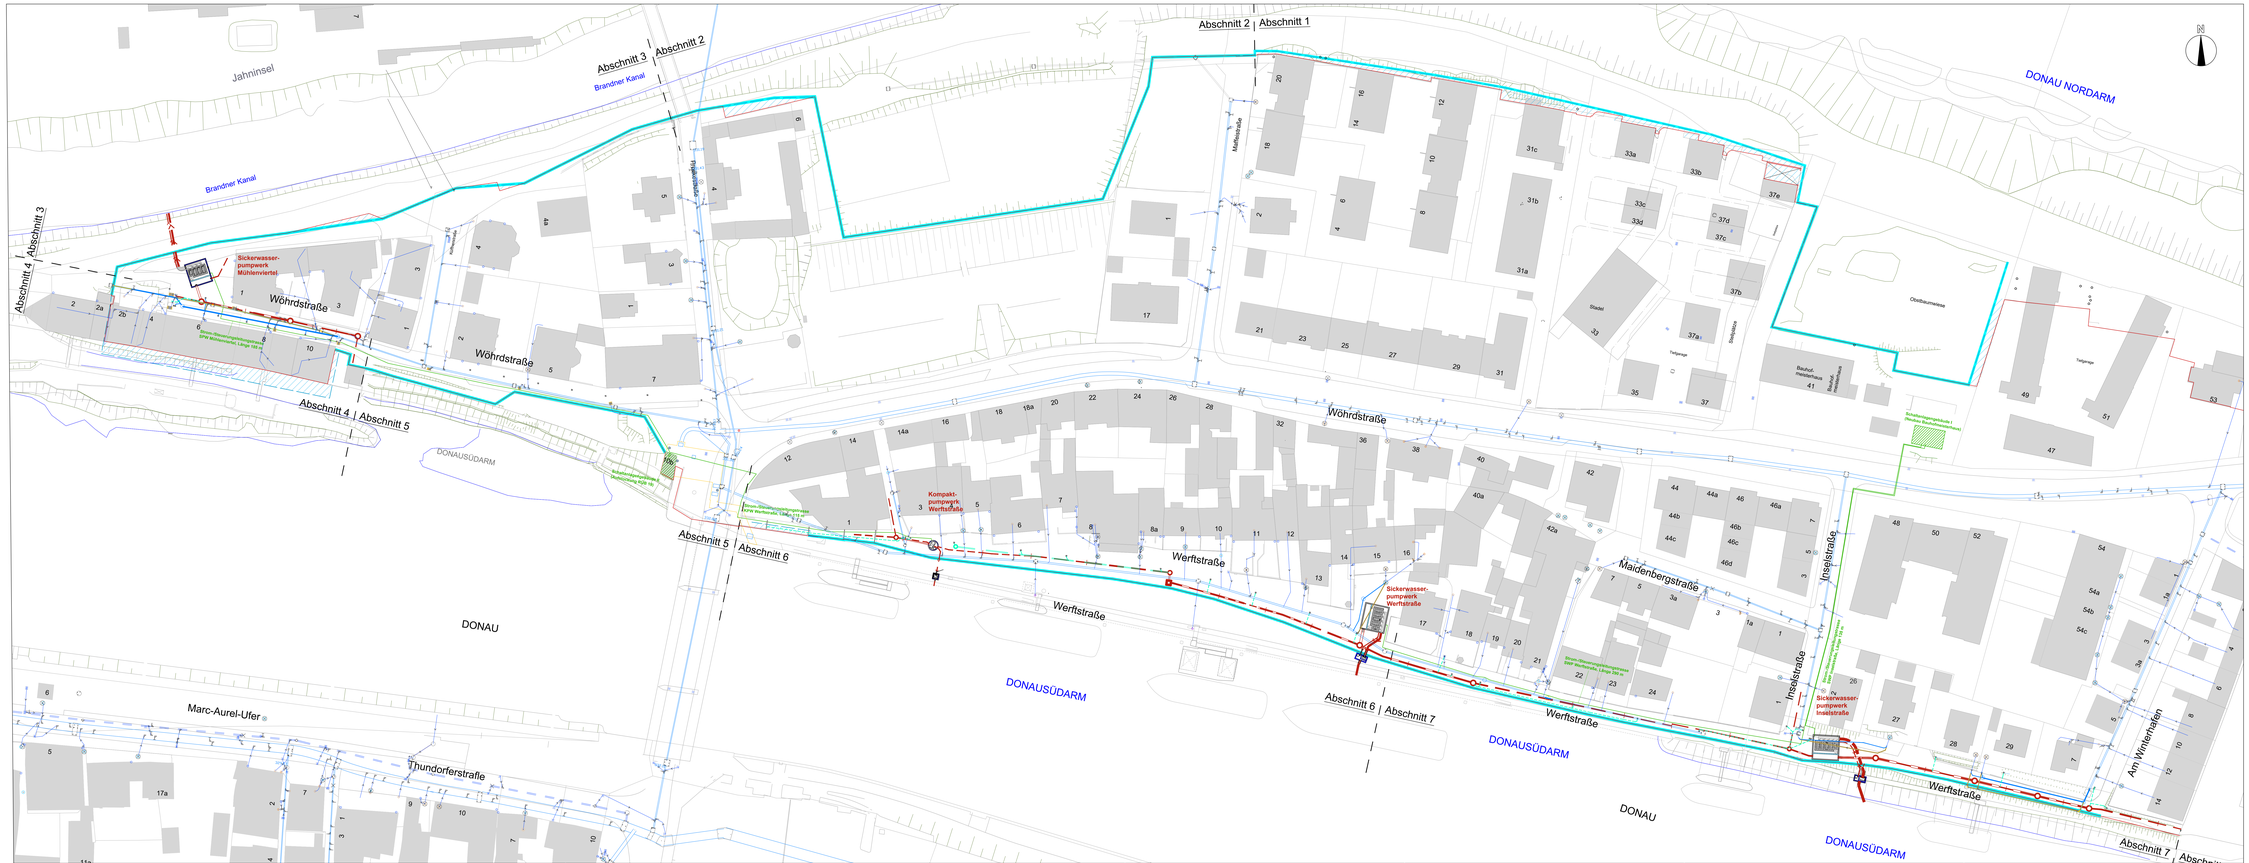
Abschnitt 1
Abschnitt 2
Abschnitt 3
Abschnitt 4
Abschnitt 5
Abschnitt 6
Abschnitt 7
Jahninsel
Brandner Kanal
DONAU NORDARM
DONAUSÜDARM
DONAU
Sickerwasser-pumpwerk Mühlenviertel
Wöhrdstraße
Müllerstraße
Müllerstraße
Kompakt-pumpwerk Wöhrdstraße
Sickerwasser-pumpwerk Wöhrdstraße
Werftstraße
Sickerwasser-pumpwerk Werftstraße
Maidenbergstraße
Inselstraße
Sickerwasser-pumpwerk Inselstraße
Ann Winterhafen
Marc-Aurel-Ufer
Thundorferstraße
Obstbaumwiese
Stadel
Stellplätze
Garagen
Bauhof, Gewächshaus
Bauhof, Verwaltung
Bauhof, Werkstätten
Bauhof, Lagerhalle
Bauhof, Lagerhalle
Bauhof, Lagerhalle