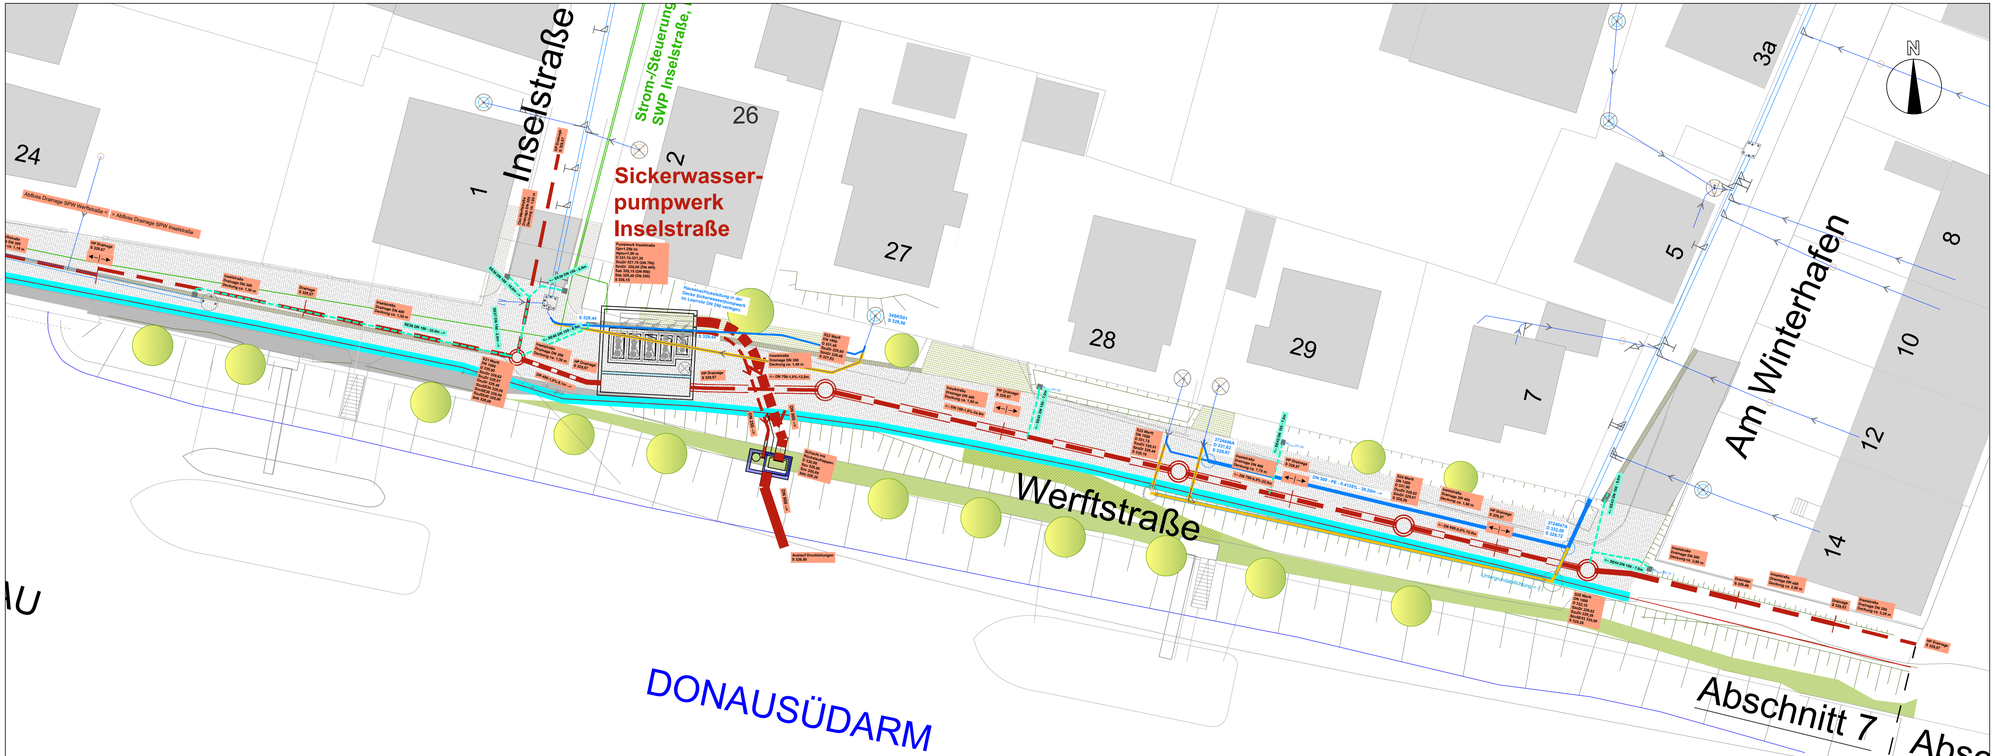

ZEICHENERKLÄRUNG

Planung

- Hochwasserschutzlinie
- Untergrundabdichtung (vertikal und horizontal)
- Kopfbalken
- DN 1200 — Drainagerohr mit Schacht, teilweise mit Transportkanal
- Sickerwasser-/Kompaktpumpwerk mit Druckleitung
- Straßenablauf mit Muldenrinne
- <-- SE40 — Anschlussleitungen Straßenabläufe
- Umlegung Abwasserkanal mit Anschlussleitung
- Umlegung Kanalhausanschlussleitung
- bestehender Abwasserkanal entfällt
- bestehende Kanalhausanschlussleitung entfällt

Bestand

- Abwasserkanal
- Kanalhausanschlussleitungen

Vermerke Genehmigungsbehörde :

Wasserwirtschaftsamt Regensburg

STADT REGENSBURG

Index	Bemerkung	geändert am	Name	geprüft am	Name
c					
b					
a					

Übersichtslageplan

Vorhaben :	Hochwasserschutz Regensburg Abschnitt H Unterer Wöhrd PLANFESTSTELLUNG	Plan-Code :	36200-E- C 1.1.4
		Anlage : C 1.1.4	Phase : G
Landkreis/ Stadt :	Regensburg	Plan-Nr. :	RB-H- PA7 LP 250
Vorhabensträger :	Freistaat Bayern, Wasserwirtschaftsamt Landshuter Straße 59, 9053 Regensburg	Vorhabenskennzeichen:	GTI:3620001015
Maßstab : 1:250	Planinhalt : Planabschnitt (PA) 7 Lageplan Inselstraße	Lagebezug:	GK4 (EPSG:31468)
		Höhenbezug:	Regensburger Höhennetz: aus 1927 in m (LfNN LV DHHN12/ 92/ 2016 des LDBV)
Planung :	Arbeitsgemeinschaft TEAM 3	erbw. :	3/2024 — team 3
		gez. :	3/2024 — Nikolai, SP
		gepr. :	5/2025 — WWA

Datum	Unterschrift Entwurfsverfasser	Datum	Unterschrift Vorhabenträger
30.04.2025		26.05.2025	