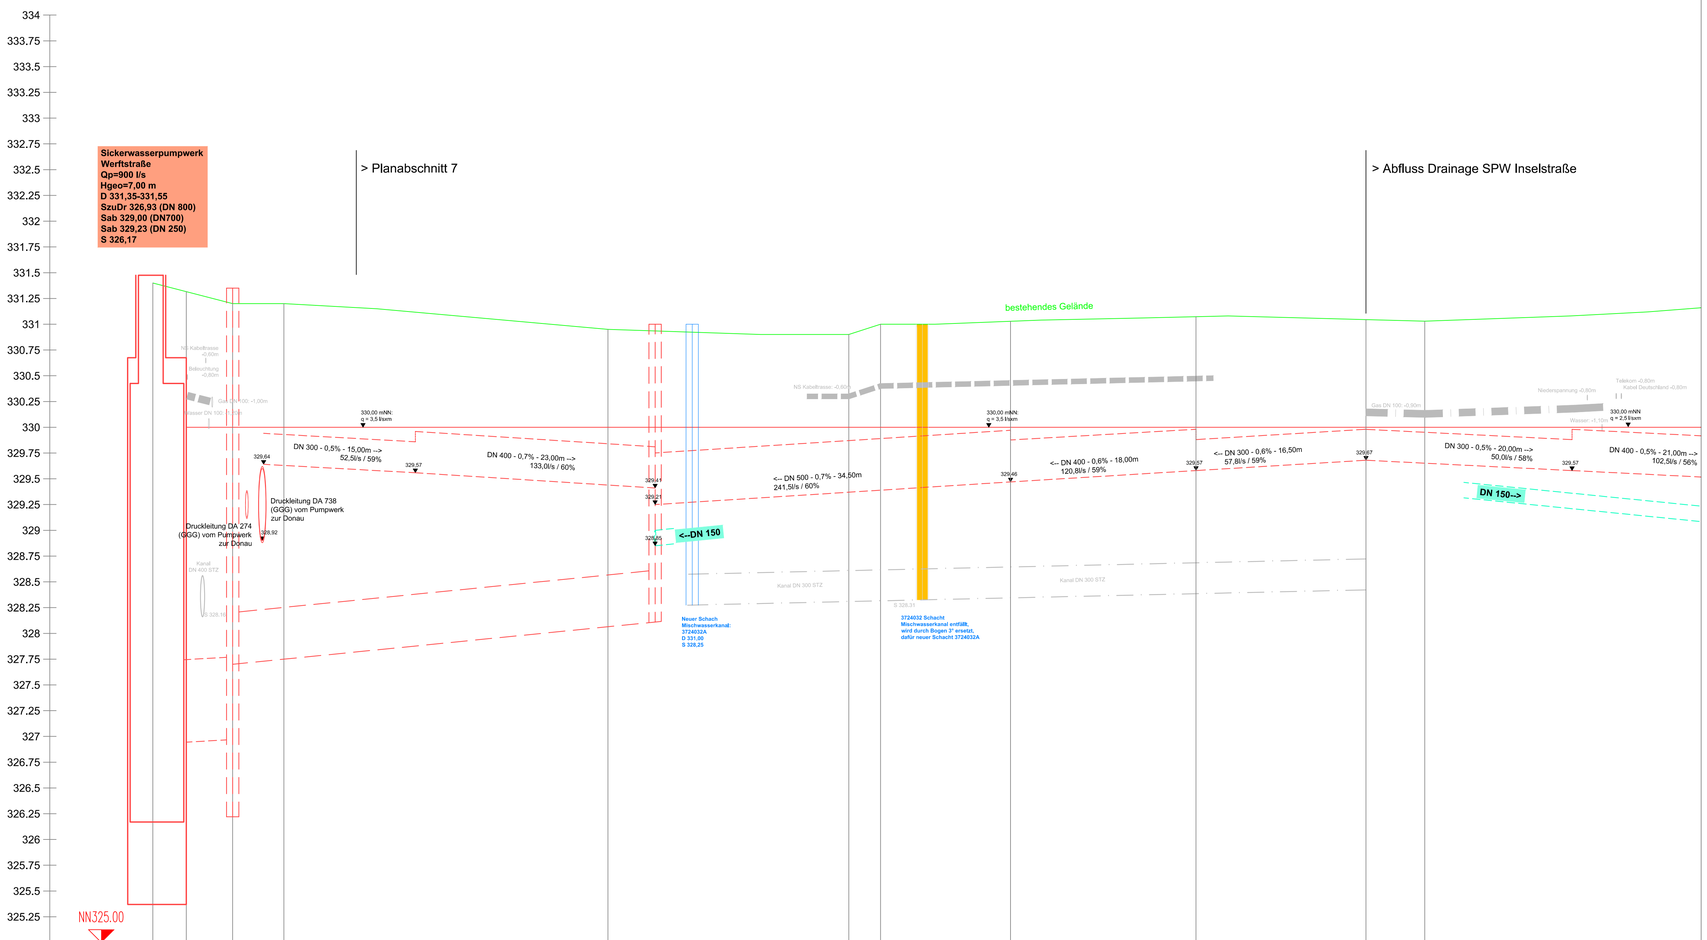

Schacht-Nr.			S1 Werft (Sandfang)		S11 Werft		
Straße			Werftstraße			Werftstraße	
Haltungslänge	m		4,50	41,00			
Gesamtlänge	m		4,50	41,00			
Querschnitt / Material	mm		DN 800	DN 500			
Abflußmenge / Abfluß bei Vollfüllung	l/s	838,3 / 1.006,1		374,5 / 414,6			
Geländehöhe geplant / (bestehend)	mNN	331,350 (331,300)	331,350 (331,200)		331,000 (330,900)		
Sohlhöhe	mNN	326,93	326,97 327,70		328,11		
Sohlgefälle	‰		5,0	10,0			
Stationierung	m	114,50	110,00		69,00	34,50	16,50 0,00

Transportkanal

ZEICHENERKLÄRUNG

Planung

- Sickerwasserspenden
- Drainagerohr mit Querschnitt in mm, Sohl- gefälle, Länge, Abflussmenge und Fließtiefe in Prozent des Querschnitts, Angabe Sohlhöhe
- Transportkanal
- Anschlussleitung für Straßenoberflächenentwässerung

Bestand

- querende Leitungen im Grabenbereich
- Leitungen in Fließrichtung rechts im Grabenbereich
- Leitungen in Fließrichtung links im Grabenbereich
- Höhenangaben der Versorgungsleitungen beziehen sich auf das bestehende Gelände und sind Schätzangaben

Vermerke Genehmigungsbehörde :

Wasserwirtschaftsamt Regensburg

STADT REGENSBURG

Index	Bemerkung	geändert am	Name	geprüft am	Name
c					
b					
a					

Übersichtslageplan

Vorhaben :	Hochwasserschutz Regensburg Abschnitt H Unterer Wöhrd PLANFESTSTELLUNG	Plan-Code :	36200-E- C 1.2.3
		Anlage : C 1.2.3	Phase : G
Landkreis/ Stadt :	Regensburg	Plan-Nr. :	RB-H- PA6/7 LS 250
Vorhabensträger :	Freistaat Bayern, Wasserwirtschaftsamt Landshuter Straße 59, 9053 Regensburg	Vorhabenskennzeichen:	G1t 3620001015
Maßstab : 1:250/25	Planinhalt : Planabschnitt (PA) 6/7 Längsschnitt Werftstraße-Ost	Lagebezug:	GK4 (EPSG 31468)
		Höhenbezug:	Regensburger Höhennetz: aus 1927 in m ü.NN (# DHHN12/ 92/ 2016 des LDBV)
Planung :	Arbeitsgemeinschaft TEAM 3	erstw. :	3/2024 team 3
		gez. :	4/2025 Nikolai, SP
		gepr. :	5/2025 WWA
30.04.2025 Datum	Unterschrift Entwurfsverfasser	26.05.2025 Datum	Unterschrift Vorhabenträger