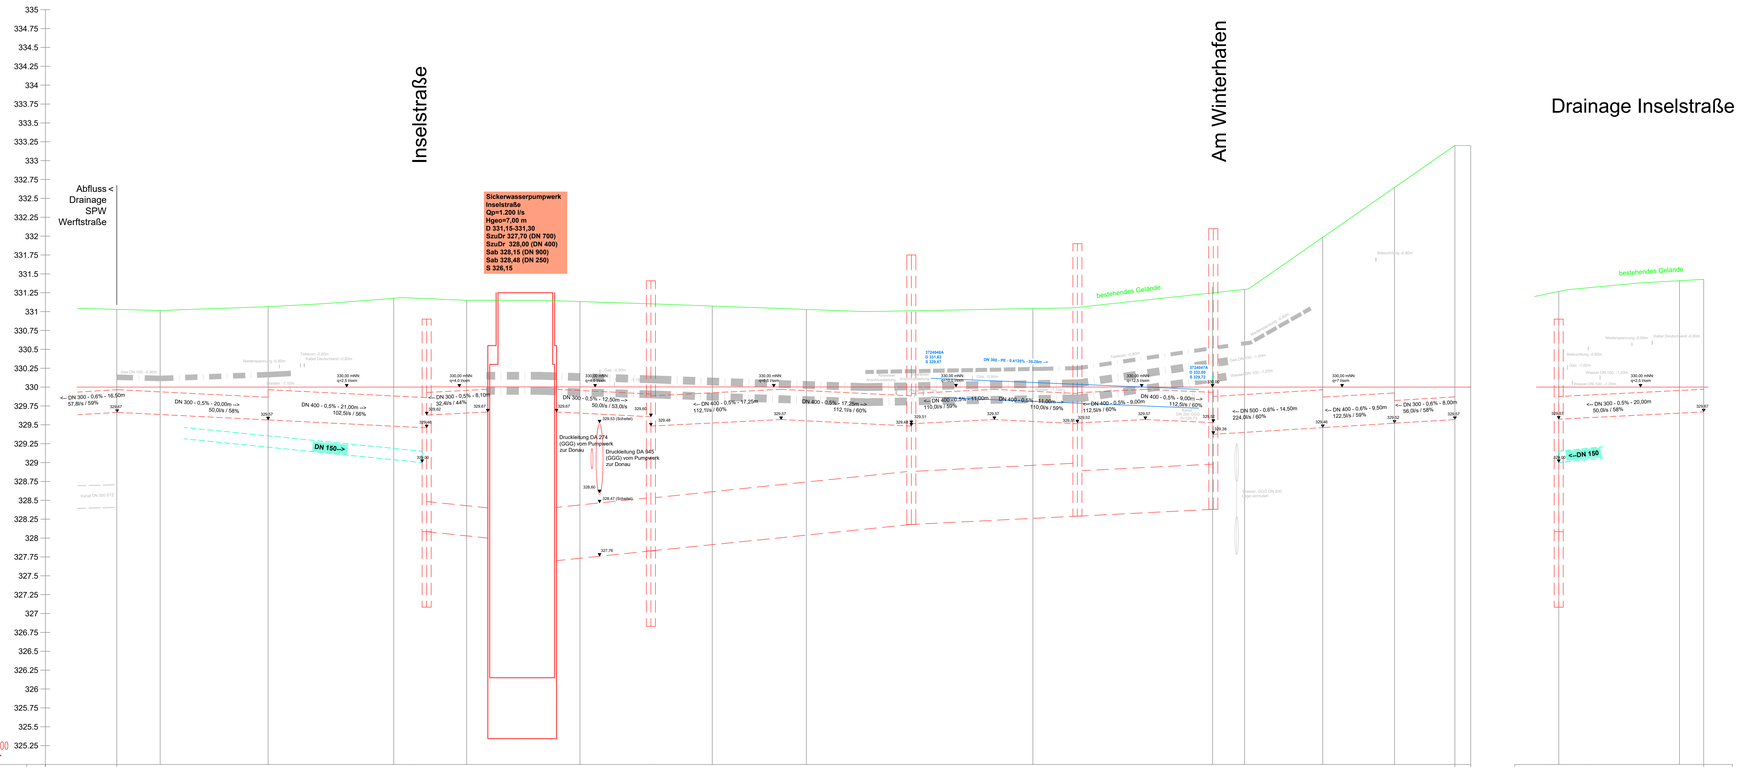

MAßSTAB 1:250/25

Transportkanal

| Schacht-Nr. | | S21 Werft (Sandfang) | | S22 Werft (Sandfang) | | S23 Werft | | S24 Werft | | S25 Werft | | |