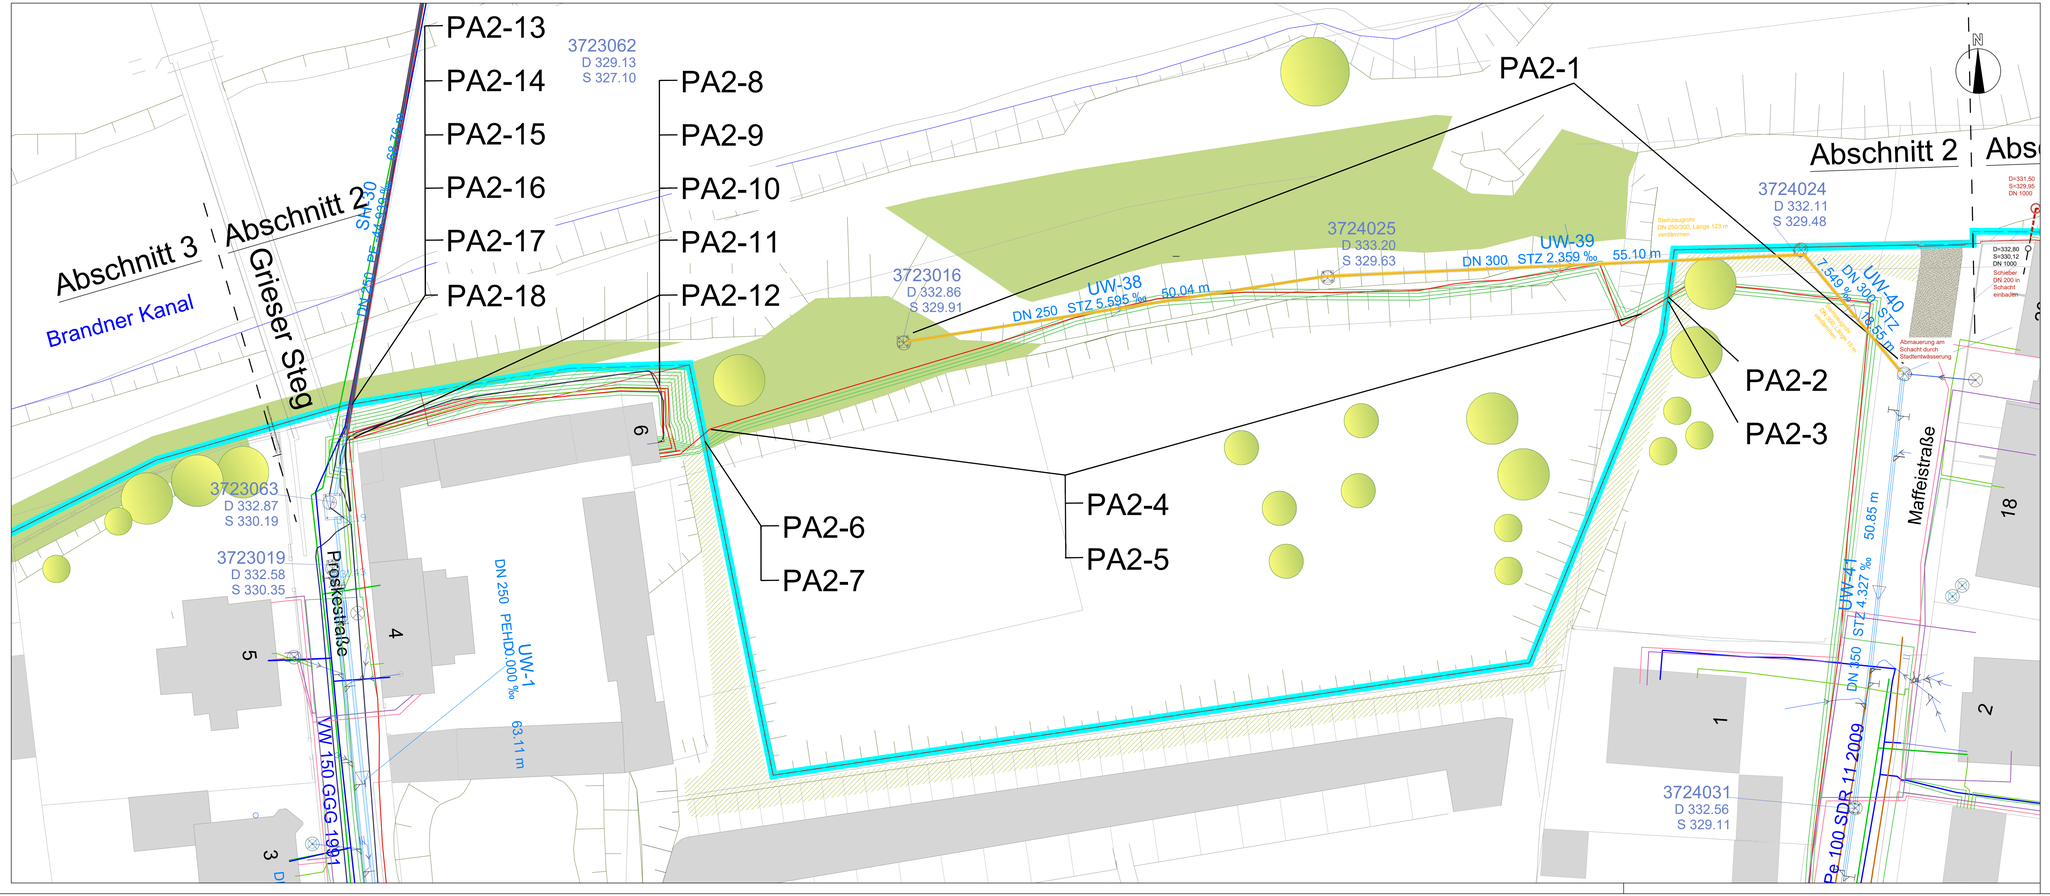

ZEICHENERKLÄRUNG

Planung

- Hochwasserschutzlinie
- Untergrundabdichtung (vertikal und horizontal)
- Kopfbalken
- Drainagerohr mit Schacht, teilweise mit Transportkanal
- Sickerwasser-/Kompaktpumpwerk mit Druckleitung
- Strom-/ Steuerleitungstrasse mit Schaltanlage
- Straßenablauf mit Muldenrinne
- Anschlussleitungen Straßenablaufe
- Regenwasserkanal für Oberflächenentwässerung
- Umlegung Abwasserkanal mit Anschlussleitung
- Umlegung Kanalhausanschlussleitung
- bestehender Abwasserkanal entfällt
- bestehende Kanalhausanschlussleitung entfällt
- bestehender Straßenablauf entfällt
- Vorschlag Trasse Umlegung Versorgungsleitung

Bestand

- Abwasserkanal
- Kanalhausanschlussleitungen
- Wasserleitung
- Gasleitung
- Stromkabel - Mittelspannung
- Stromkabel - Niederspannung
- Stromkabel - Hausanschluss Niederspannung
- Lichtwellenleiterkabel - Leerrohr
- Telekomkabel (graphisch entnommen)
- Kabel Deutschland (graphisch entnommen)
- Straßenbeleuchtung (graphisch entnommen)

Vermerke Genehmigungsbehörde :

Wasserwirtschaftsamt Regensburg

STADT REGENSBURG

Index	Bemerkung	geändert am	Name	geprüft am	Name
c					
b					
a					

Übersichtslageplan

Vorhaben : Hochwasserschutz Regensburg
Abschnitt H Unterer Wöhrd
PLANFESTSTELLUNG

Landkreis/ Stadt : Regensburg

Vorhabensträger : Freistaat Bayern, Wasserwirtschaftsamt
Landshuter Straße 59, 9053 Regensburg

Plan-Code : 36200-E- C 8.2.1

Anlage : C 8.2.1 Phase : G

Plan-Nr : RB-H- PA2 KLP 250

Vorhabensbezeichnung : G1-N-36200/1015

Maßstab : 1:250

Planinhalt : Planabschnitt (PA) 2
Lageplan Konflikte Sparten PA 2

Lagebezug : GK4 (EPSG 31468)

Höhenbezug : Regensburger Höhennetz; aus DGM1 (s.LfU) DHHN12 SD 2016 (ex LDBV)

Planung : Arbeitsgemeinschaft TEAM 3

RIGERSBERGER GMBH + KG

ARCHIGROUP architekten und landschaftsarchitekten

LANDSCHAFTSARCHITEKTEN

erst. :	3/2024	team 3
gez. :	3/2024	Nikolai, SP
gepr. :	5/2025	WWA

30.04.2025 Datum — Unterschrift Entwurfsverfasser

26.05.2025 Datum — Unterschrift Vorhabensträger