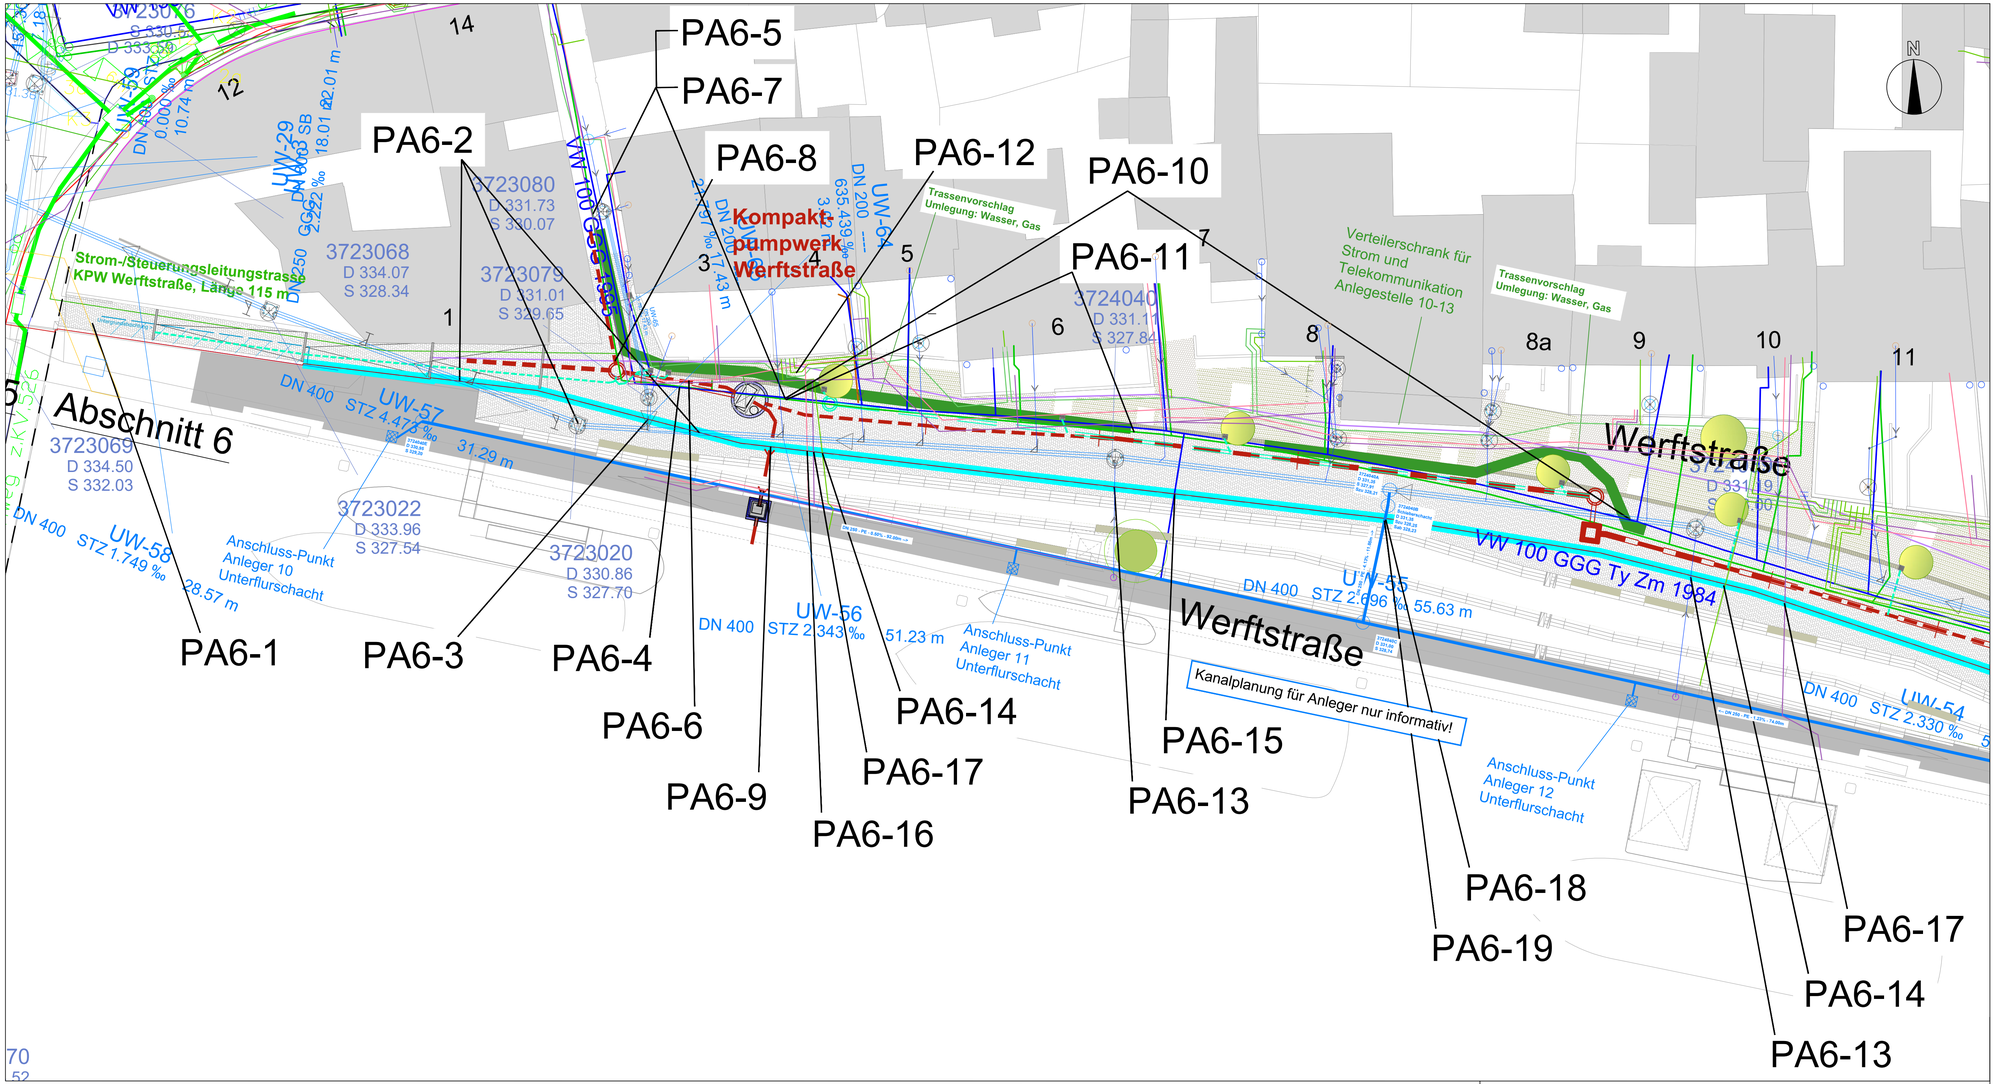

ZEICHENERKLÄRUNG

Planung

- Hochwasserschutzlinie
- Untergrundabdichtung (vertikal und horizontal)
- Kopfbalken
- Drainagerohr mit Schacht, teilweise mit Transportkanal
- Sickerwasser-/Kompaktpumpwerk mit Druckleitung
- Strom-/ Steuerleitungstrasse mit Schaltanlage
- Straßenablauf mit Muldenrinne
- Anschlussleitungen Straßenabläufe
- Regenwasserkanal für Oberflächenentwässerung
- Umlegung Abwasserkanal mit Anschlussleitung
- Umlegung Kanalhausanschlussleitung
- bestehender Abwasserkanal entfällt
- bestehende Kanalhausanschlussleitung entfällt
- bestehender Straßenablauf entfällt
- Vorschlag Trasse Umlegung Versorgungsleitung

Bestand

- Abwasserkanal
- Kanalhausanschlussleitungen
- Wasserleitung
- Gasleitung
- Stromkabel - Mittelspannung
- Stromkabel - Niederspannung
- Stromkabel - Hausanschluss Niederspannung
- Lichtwellenleiterkabel - Leerrohr
- Telekomkabel (graphisch entnommen)
- Kabel Deutchland (graphisch entnommen)
- Straßenbeleuchtung (graphisch entnommen)

Vermerke Genehmigungsbehörde :

Wasserwirtschaftsamt Regensburg

STADT REGENSBURG

Index	Bemerkung	geändert am	Name	geprüft am	Name
c					
b					
a					

Übersichtslageplan

Vorhaben : Hochwasserschutz Regensburg
Abschnitt H Unterer Wöhrd
PLANFESTSTELLUNG

Landkreis/ Stadt : Regensburg

Vorhabensträger : Freistaat Bayern, Wasserwirtschaftsamt Landshuter Straße 59, 9053 Regensburg

Plan-Code : 36200-E- C 8.4.1

Anlage : C 8.4.1 Phase : G

Plan-Nr : RB-H- PA6-W KLP 250

Vorhabenskennzeichen: GN:362000101 5

Maßstab : 1:250

Planinhalt : Planabschnitt (PA) 6
Lageplan Konflikte Sparten PA 6 - West

Lagebezug: GK4 (EPSG 31468)

Höhenbezug: Regensburger Höhennetz ,aus 1927 in m üNN (4 DHHN12/ 92/ 2016 des LDBV)

Planung : Arbeitsgemeinschaft TEAM 3

schönigplan INGENIEURGESELLSCHAFT mbH; ANCHISOBPS architekten und landschaftsarchitekten; tym. Landschaftsarchitekten

entw. :	3/2024	team 3	
gez. :	3/2024	Nikolai, SP	
gepr. :	5/2025	WWA	

30.04.2025 Datum — Unterschrift Entwurfsverfasser

26.05.2025 Datum — Unterschrift Vorhabensträger