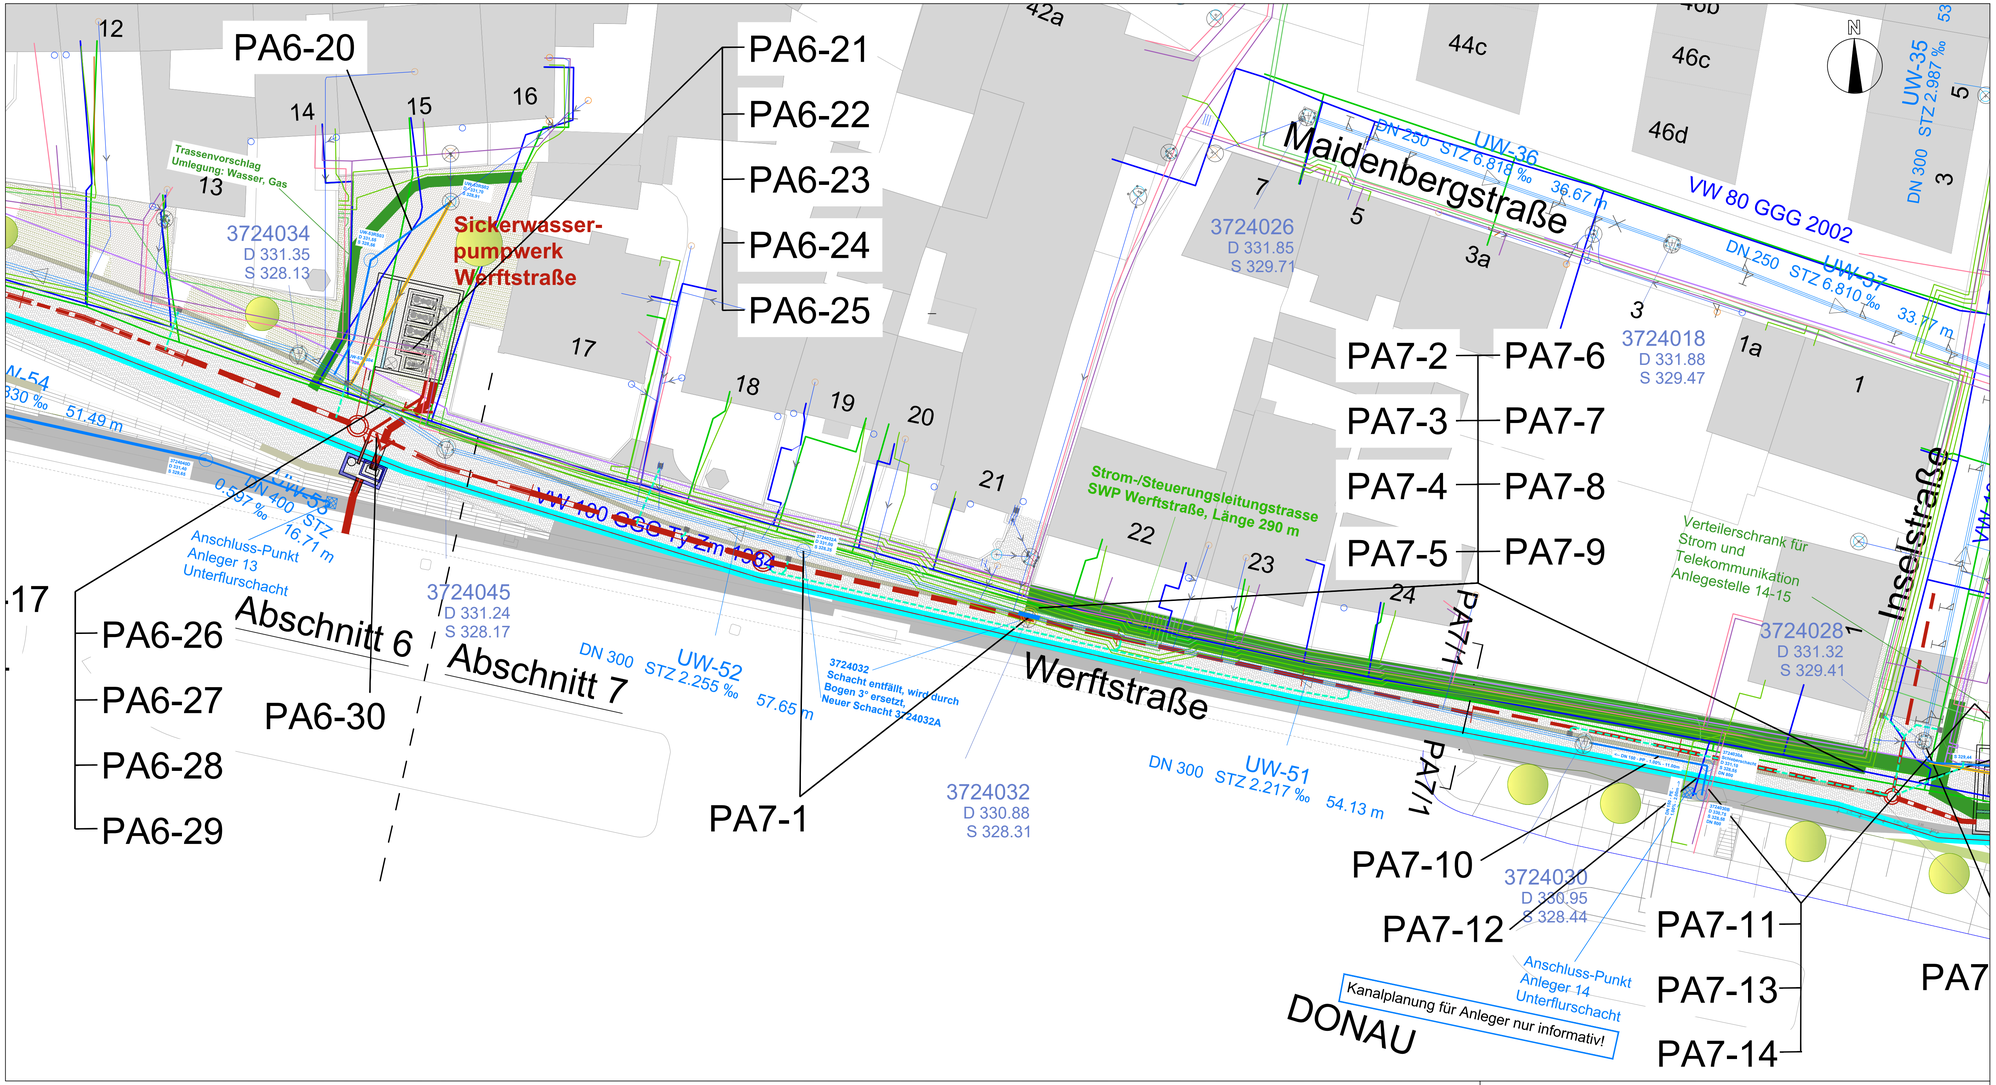

ZEICHENERKLÄRUNG

Planung

- Hochwasserschutzlinie
- Untergrundabdichtung (vertikal und horizontal)
- Kopfbalken
- Drainagerohr mit Schacht, teilweise mit Transportkanal
- Sickerwasser-/Kompaktpumpwerk mit Druckleitung
- Strom-/ Steuerleitungstrasse mit Schaltanlage
- Straßenablauf mit Muldenrinne
- Anschlussleitungen Straßenabläufe
- Regenwasserkanal für Oberflächenentwässerung
- Umlegung Abwasserkanal mit Anschlussleitung
- Umlegung Kanalhausanschlussleitung
- bestehender Abwasserkanal entfällt
- bestehende Kanalhausanschlussleitung entfällt
- bestehender Straßenablauf entfällt
- Vorschlag Trasse Umlegung Versorgungsleitung

Bestand

- Abwasserkanal
- Kanalhausanschlussleitungen
- Wasserleitung
- Gasleitung
- Stromkabel - Mittelspannung
- Stromkabel - Niederspannung
- Stromkabel - Hausanschluss Niederspannung
- Lichtwellenleiterkabel - Leerrohr
- Telekomkabel (graphisch entnommen)
- Kabel Deutchland (graphisch entnommen)
- Straßenbeleuchtung (graphisch entnommen)

Vermerke Genehmigungsbehörde :

Wasserwirtschaftsamt Regensburg

STADT REGENSBURG

Index	Bemerkung	geändert am	Name	geprüft am	Name
c					
b					
a					

Übersichtslageplan

Vorhaben :	Hochwasserschutz Regensburg Abschnitt H Unterer Wöhrd PLANFESTSTELLUNG	Plan-Code:	36200-E- C 8.4.2
		Anlage : C 8.4.2	Phase : G
Landkreis/ Stadt :	Regensburg	Plan-Nr. :	RB-H- PA6/7 KLP 250
Vorhabensträger :	Freistaat Bayern, Wasserwirtschaftsamt Landshuter Straße 59, 9053 Regensburg	Vorhabenskennzeichen:	G1I 3020001015
Maßstab :	1:250	Lagebezug:	GK4 (EPSG 31468)
	Planinhalt : Planabschnitt (PA) 6/7 Lageplan Konflikte Sparten PA 6/7	Höhenbezug:	Regensburger Höhennetz aus 1927 m in o.NN (# DHHN12/ 92/ 2016 des LDBV)
Planung :	Arbeitsgemeinschaft TEAM 3	entw. :	3/2024 team 3
		gez. :	3/2024 Nikolai, SP
		gepr. :	5/2025 WWA

30.04.2025		26.05.2025	
Datum	Unterschrift Entwurfsverfasser	Datum	Unterschrift Vorhabensträger