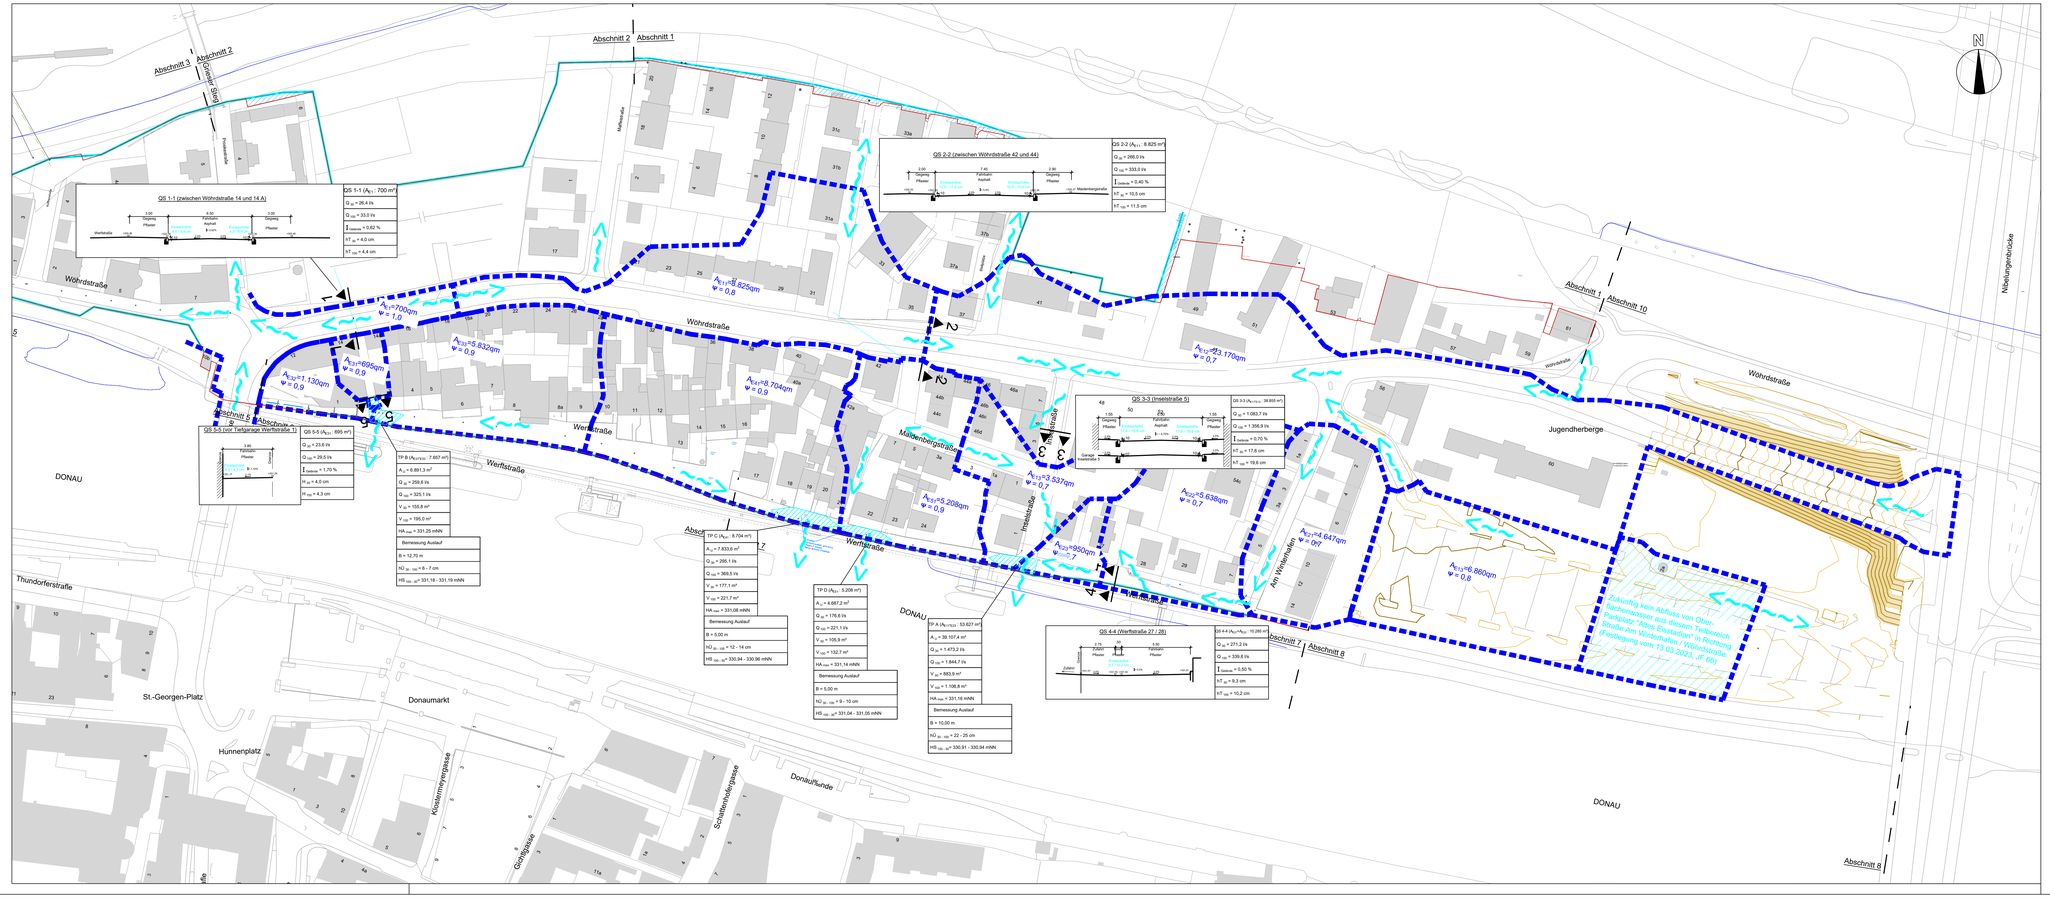

Niederschlagsspenden nach KOSTRA-DWD 2020: Spalte 174, Zeile 183

Bemessungsregen mit Dauerstufe 10 min:

T=30 Jahre: $r_{10,30}$=376,7 l/sxha, T=100 Jahre: $r_{10,100}$=471,7 l/sxha

ZEICHENERKLÄRUNG

- Abgrenzung Teileinzugsgebiete
- $A_{E,U}$=8.825qm, Ψ = 0,8 — Fläche Teileinzugsgebiet in m² mit Abflussbeiwert
- Oberflächiger Hauptfließweg
- Überstaufläche am Tiefpunkt bis zur maximalen Aufstauhöhe

QS 2-2 ($A_{E,U}$: 8.825 m²)	Querschnitt Straße mit Nummer und Einzugsfläche
Q_{ab} = 266,0 l/s	Abflussmenge bei T=30 Jahren
Q_{zu} = 303,0 l/s	Abflussmenge bei T=100 Jahren
$I_{Gelände}$ = 0,40 %	Längsgefälle Straße
h^T_{ab} = 10,5 cm	Fließtiefe für Abflussmenge bei T=30 Jahren
h^T_{zu} = 11,5 cm	Fließtiefe für Abflussmenge bei T=100 Jahren
TP A ($A_{E,U(n.a.)}$: 53.627 m²)	Tiefpunkt der Einzugsfläche
$A_{E,u}$ = 39.107,4 m²	Versiegelte Fläche
Q_{ab} = 1.473,2 l/s	Abflussmenge bei T=30 Jahren
Q_{zu} = 1.844,7 l/s	Abflussmenge bei T=100 Jahren
V_{ab} = 883,9 m³	Überstauvolumen bei T=30 Jahren
V_{zu} = 1.106,8 m³	Überstauvolumen bei T=100 Jahren
HA_{max} = 331,16 mNN	maximale Aufstauhöhe ohne Überlauf in private Grundstücke
Bemessung Auslauf	Auslauf in Donau
B = 10,00 m	Breite des Überlaufs / Auslaufs
$NÖ_{30-100}$ = 22 - 25 cm	Überlaufhöhe (Überfallhöhe bzw. Fließtiefe) bei T=30 bzw 100 Jahren
$HS_{100-µT}$ 330,91 - 330,94 mNN	Schwellenhöhe des Auslaufs bei T=100 bzw. 30 Jahren

Vermerke Genehmigungsbehörde :

Wasserwirtschaftsamt Regensburg

STADT REGENSBURG

Index	Bemerkung	geändert am	Name	geprüft am	Name
c					
b					
a					

Übersichtslageplan

Vorhaben : Hochwasserschutz Regensburg
Abschnitt H Unterer Wöhrd
PLANFEststellung

Landkreis/ Stadt : Regensburg

Vorhabenträger : Freistaat Bayern, Wasserwirtschaftsamt
Landshuter Straße 59, 9053 Regensburg

Plan-Code : 36200-E- I 1.0

Anlage : I 1.0 | Phase : G

Plan-Nr. : RB-H- PA6/7 SR 1000

Vorhabenkennzeichen : D1 36200101015

Maßstab : 1:1.000

Planinhalt : Planabschnitt (PA) 6-7
Übersichtsplan Starkregenuntersuchung

Lagebezug : GK4 (EPSG 31468)

Höhenbezug : Regensburger Höhennetz: aus 150? m ü.NN,(1 DHHN (2 SD 2016 des LDBV)

Planung : Arbeitsgemeinschaft TEAM 3

RÖDERPLAN INGENIEURGESELLSCHAFT mbH · ARCHIGRAM architekten und landschaftsarchitekten · IFT Institut für Landschaftsarchitektur

erstellt : 3/2024 | team 3

geä. : 3/2024 | Nikolai, SP

gepr. : 5/2025 | WWA

30.04.2025 Datum | Unterschrift Ersteller/Verfasser

26.05.2025 Datum | Unterschrift Vorhabenträger